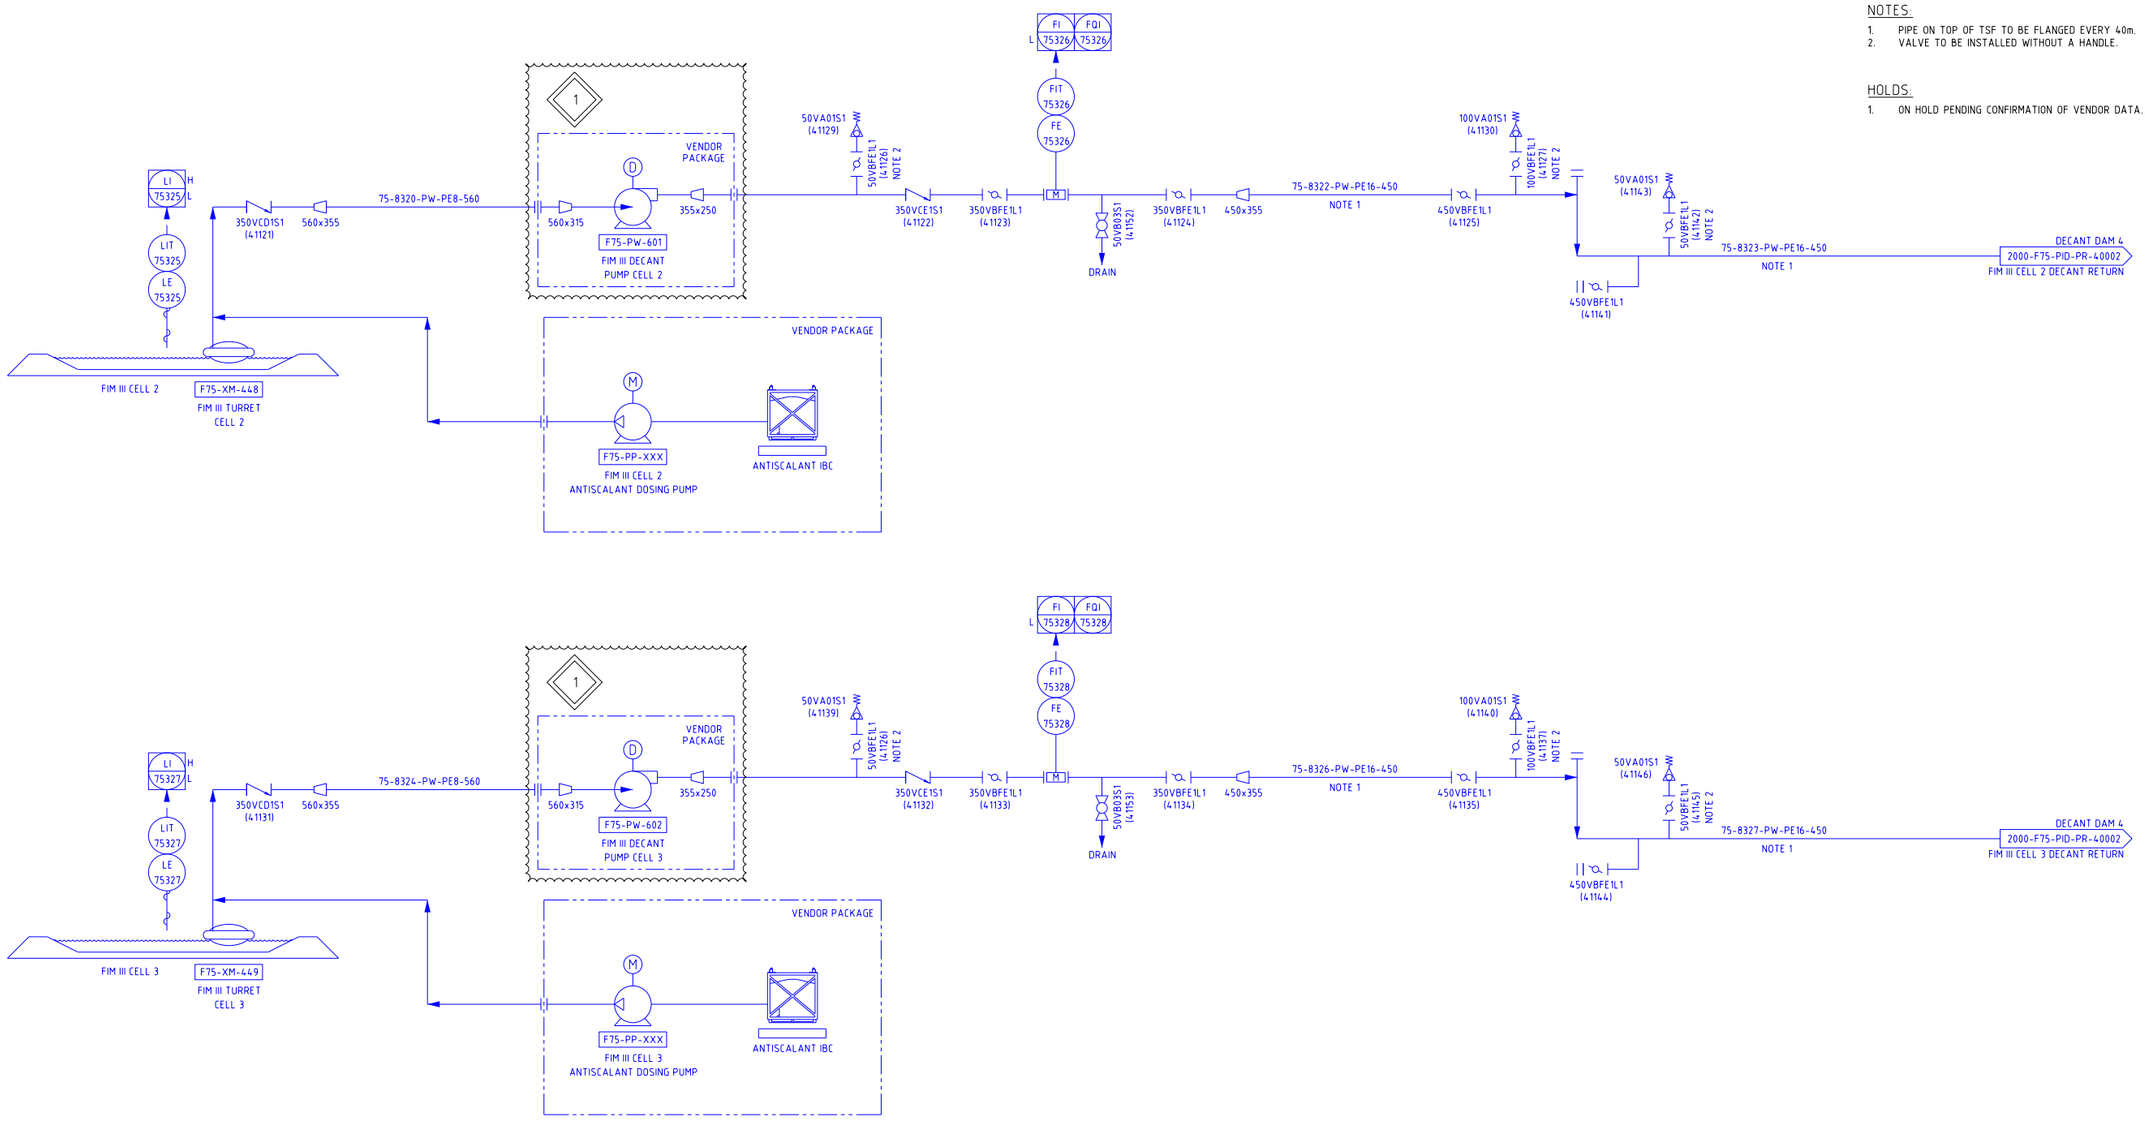



APPROVED FOR CONSTRUCTION