


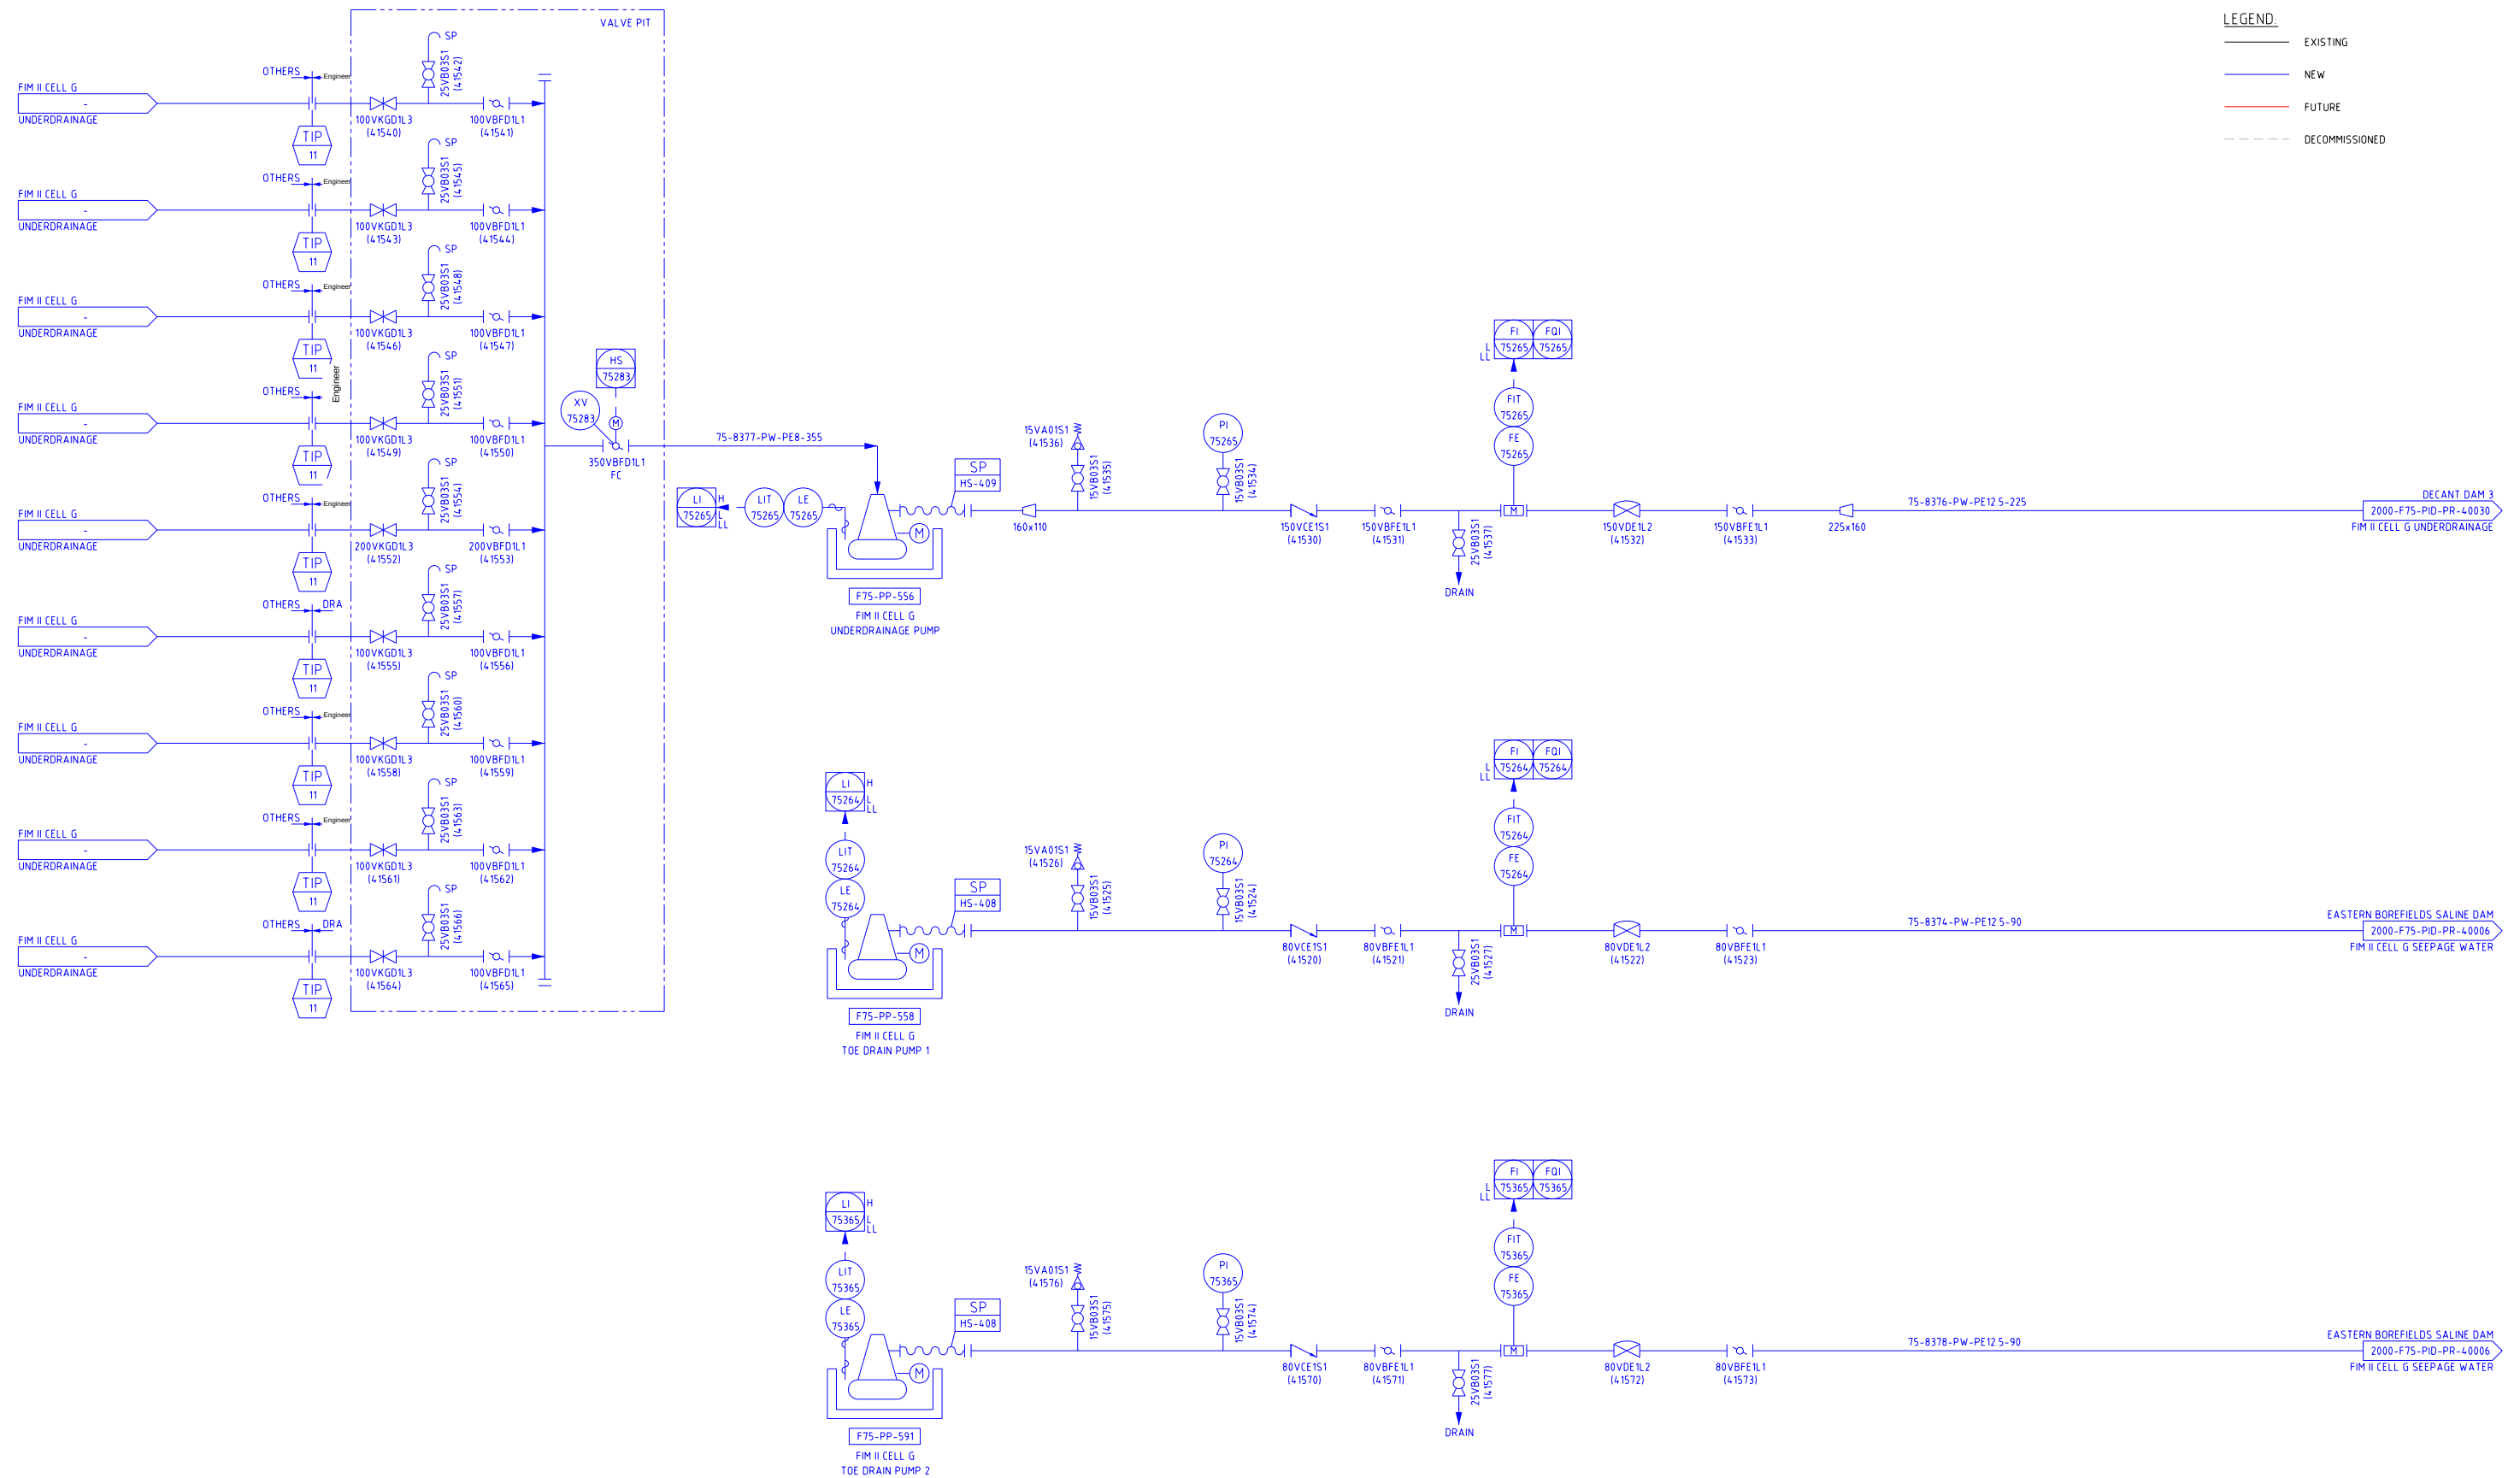

APPROVED FOR
CONSTRUCTION