


LEGEND:

EXISTING

NEW

FUTURE

DECOMMISSIONED

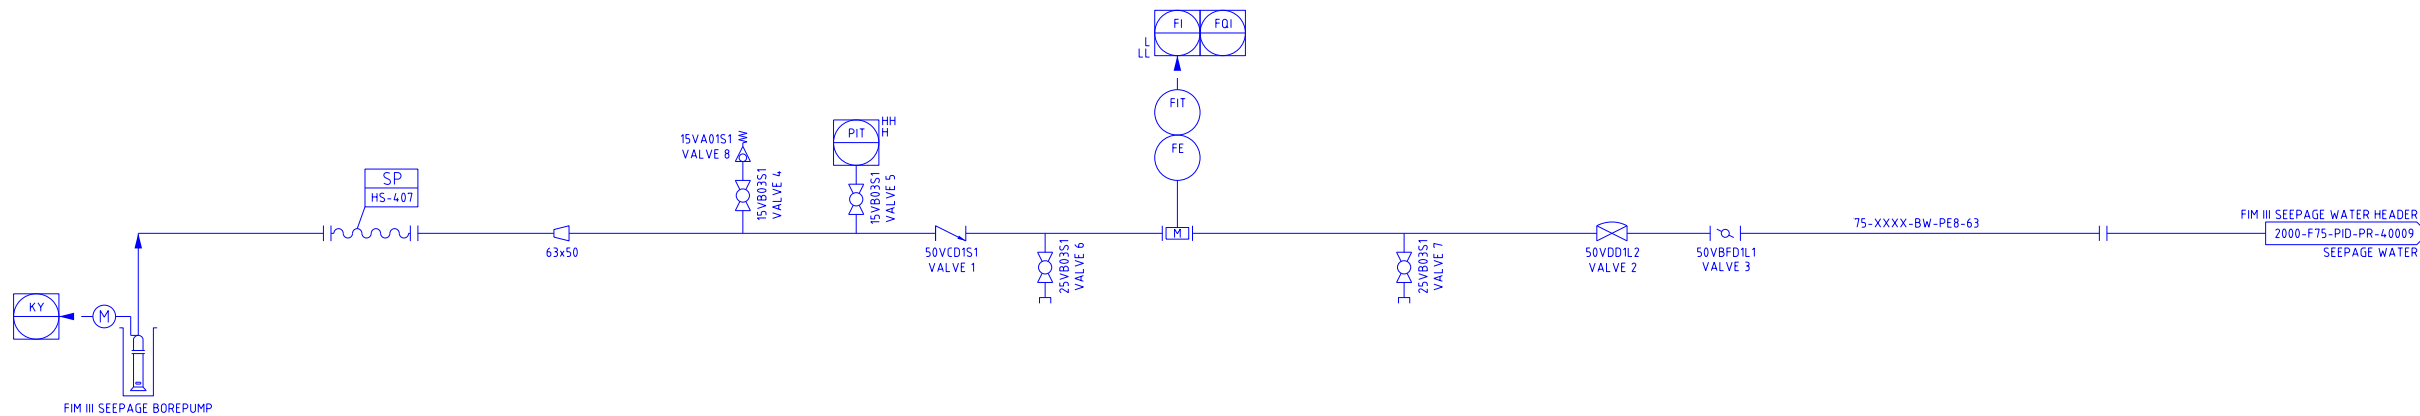

INSTRUMENT TAG LIST

				LINE AND VALVE UNIQUE NUMBERS								
PUMP	KY-	FT-	PIT-	LINE #	VALVE 1	VALVE 2	VALVE 3	VALVE 4	VALVE 5	VALVE 6	VALVE 7	VALVE 8
F75-PW-501	75730	75730	75730	8379	42001	42002	42003	42004	42006	42007	42008	42009
F75-PW-502	75731	75731	75731	8380	42011	42012	42013	42014	42016	42017	42018	42019
F75-PW-503	75732	75732	75732	8381	42021	42022	42023	42024	42026	42027	42028	42029
F75-PW-504	75733	75733	75733	8382	42031	42032	42033	42034	42036	42037	42038	42039

APPROVED FOR
CONSTRUCTION