


LEGEND:

—	EXISTING
—	NEW
—	FUTURE
- - - -	DECOMMISSIONED

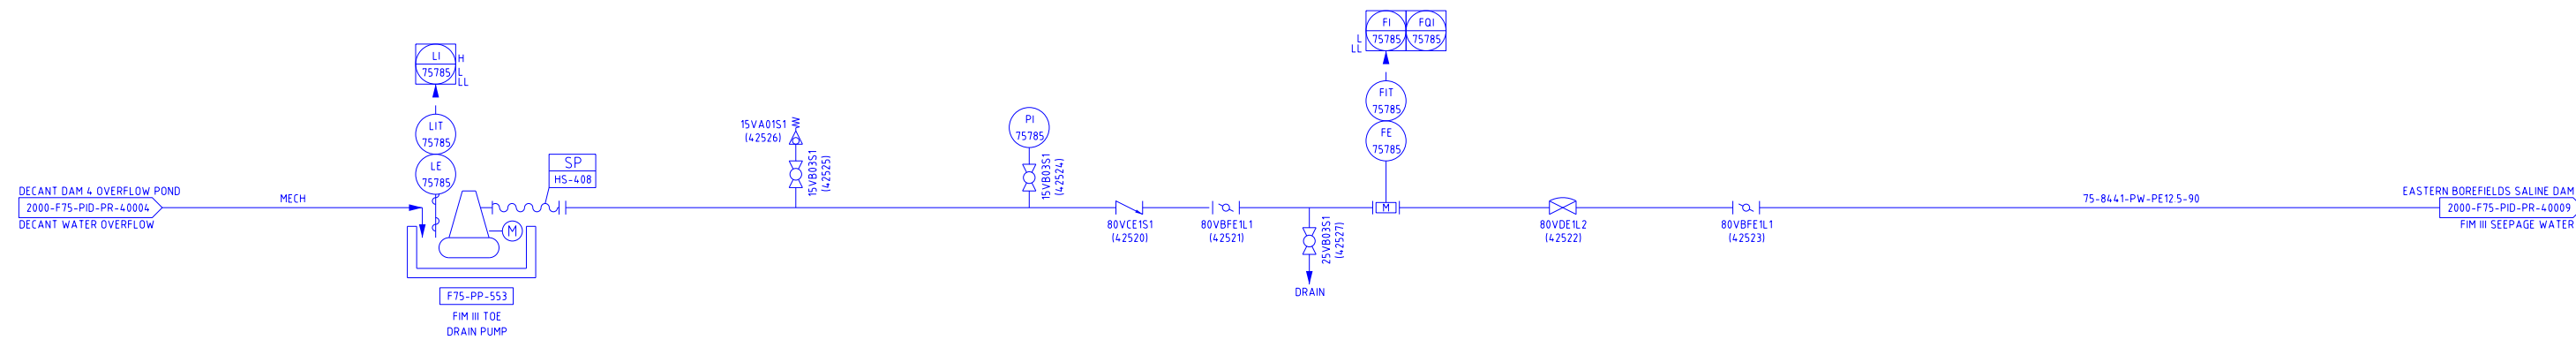

APPROVED FOR
CONSTRUCTION