


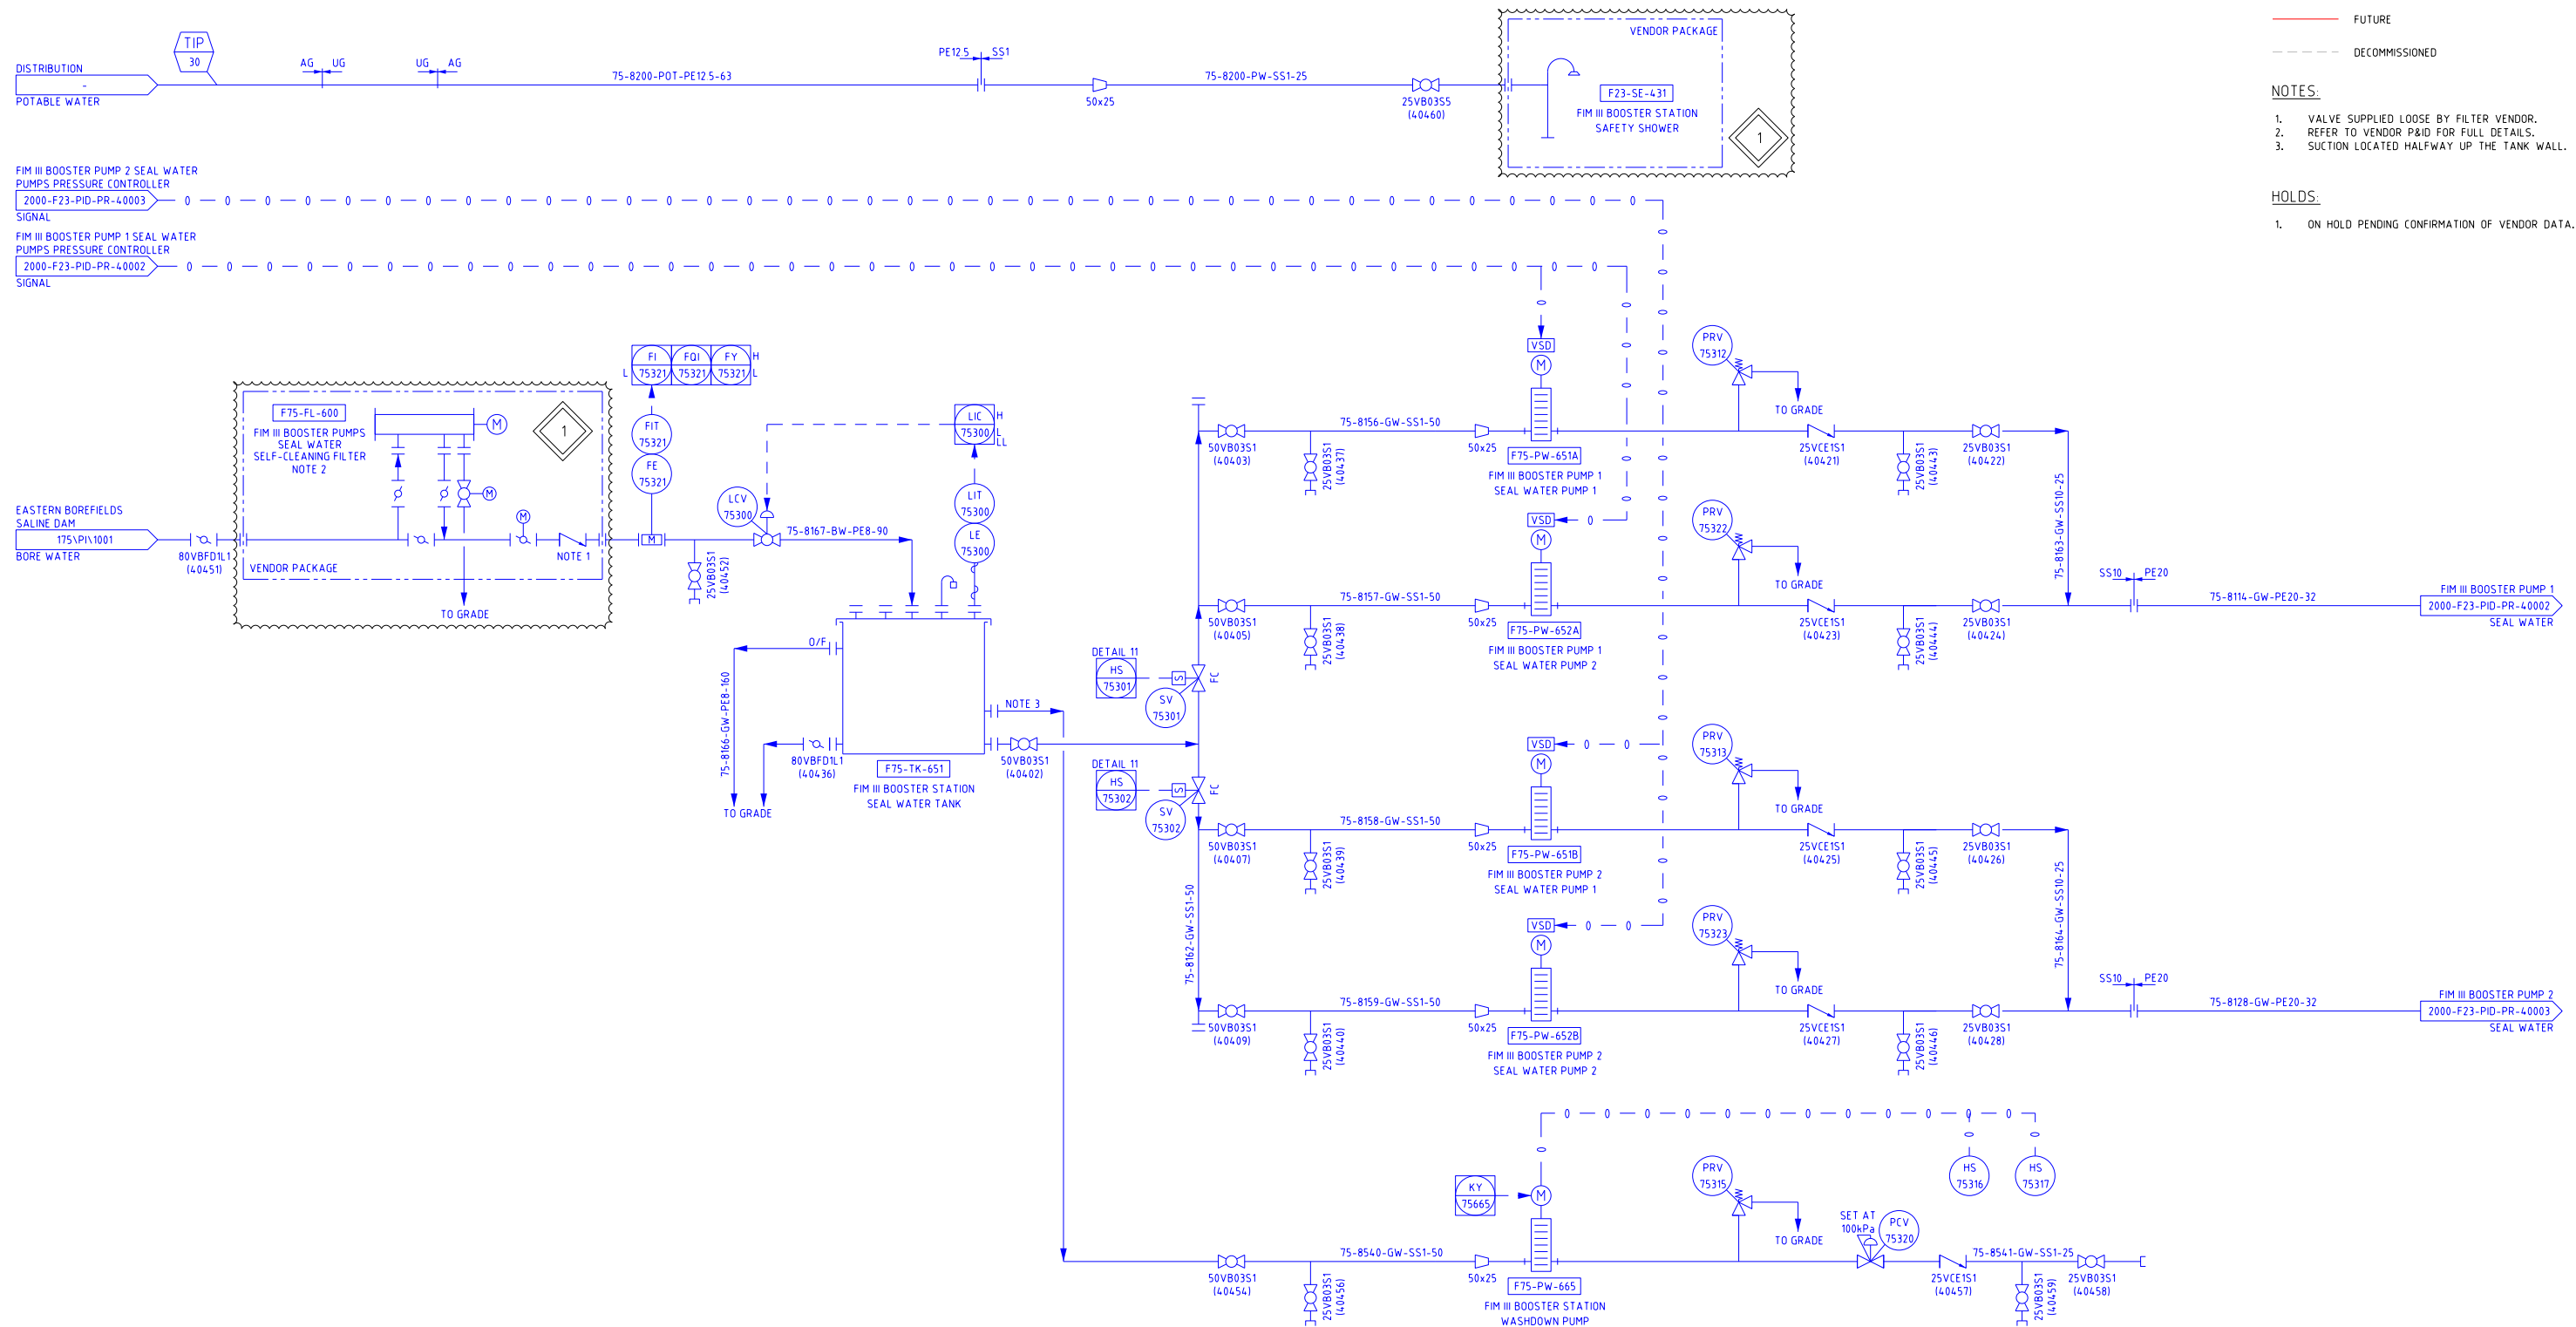

- LEGEND:**
- EXISTING
 - NEW
 - FUTURE
 - DECOMMISSIONED
- NOTES:**
1. VALVE SUPPLIED LOOSE BY FILTER VENDOR.
 2. REFER TO VENDOR P&ID FOR FULL DETAILS.
 3. SUCTION LOCATED HALFWAY UP THE TANK WALL.
- HOLDS:**
1. ON HOLD PENDING CONFIRMATION OF VENDOR DATA.

APPROVED FOR
CONSTRUCTION