


NOTES:

1. PIPING ON TSF EMBANKMENT TO BE FLANGED AT 40m CENTRES.

LEGEND:

- EXISTING
NEW
FUTURE
DECOMMISSIONED

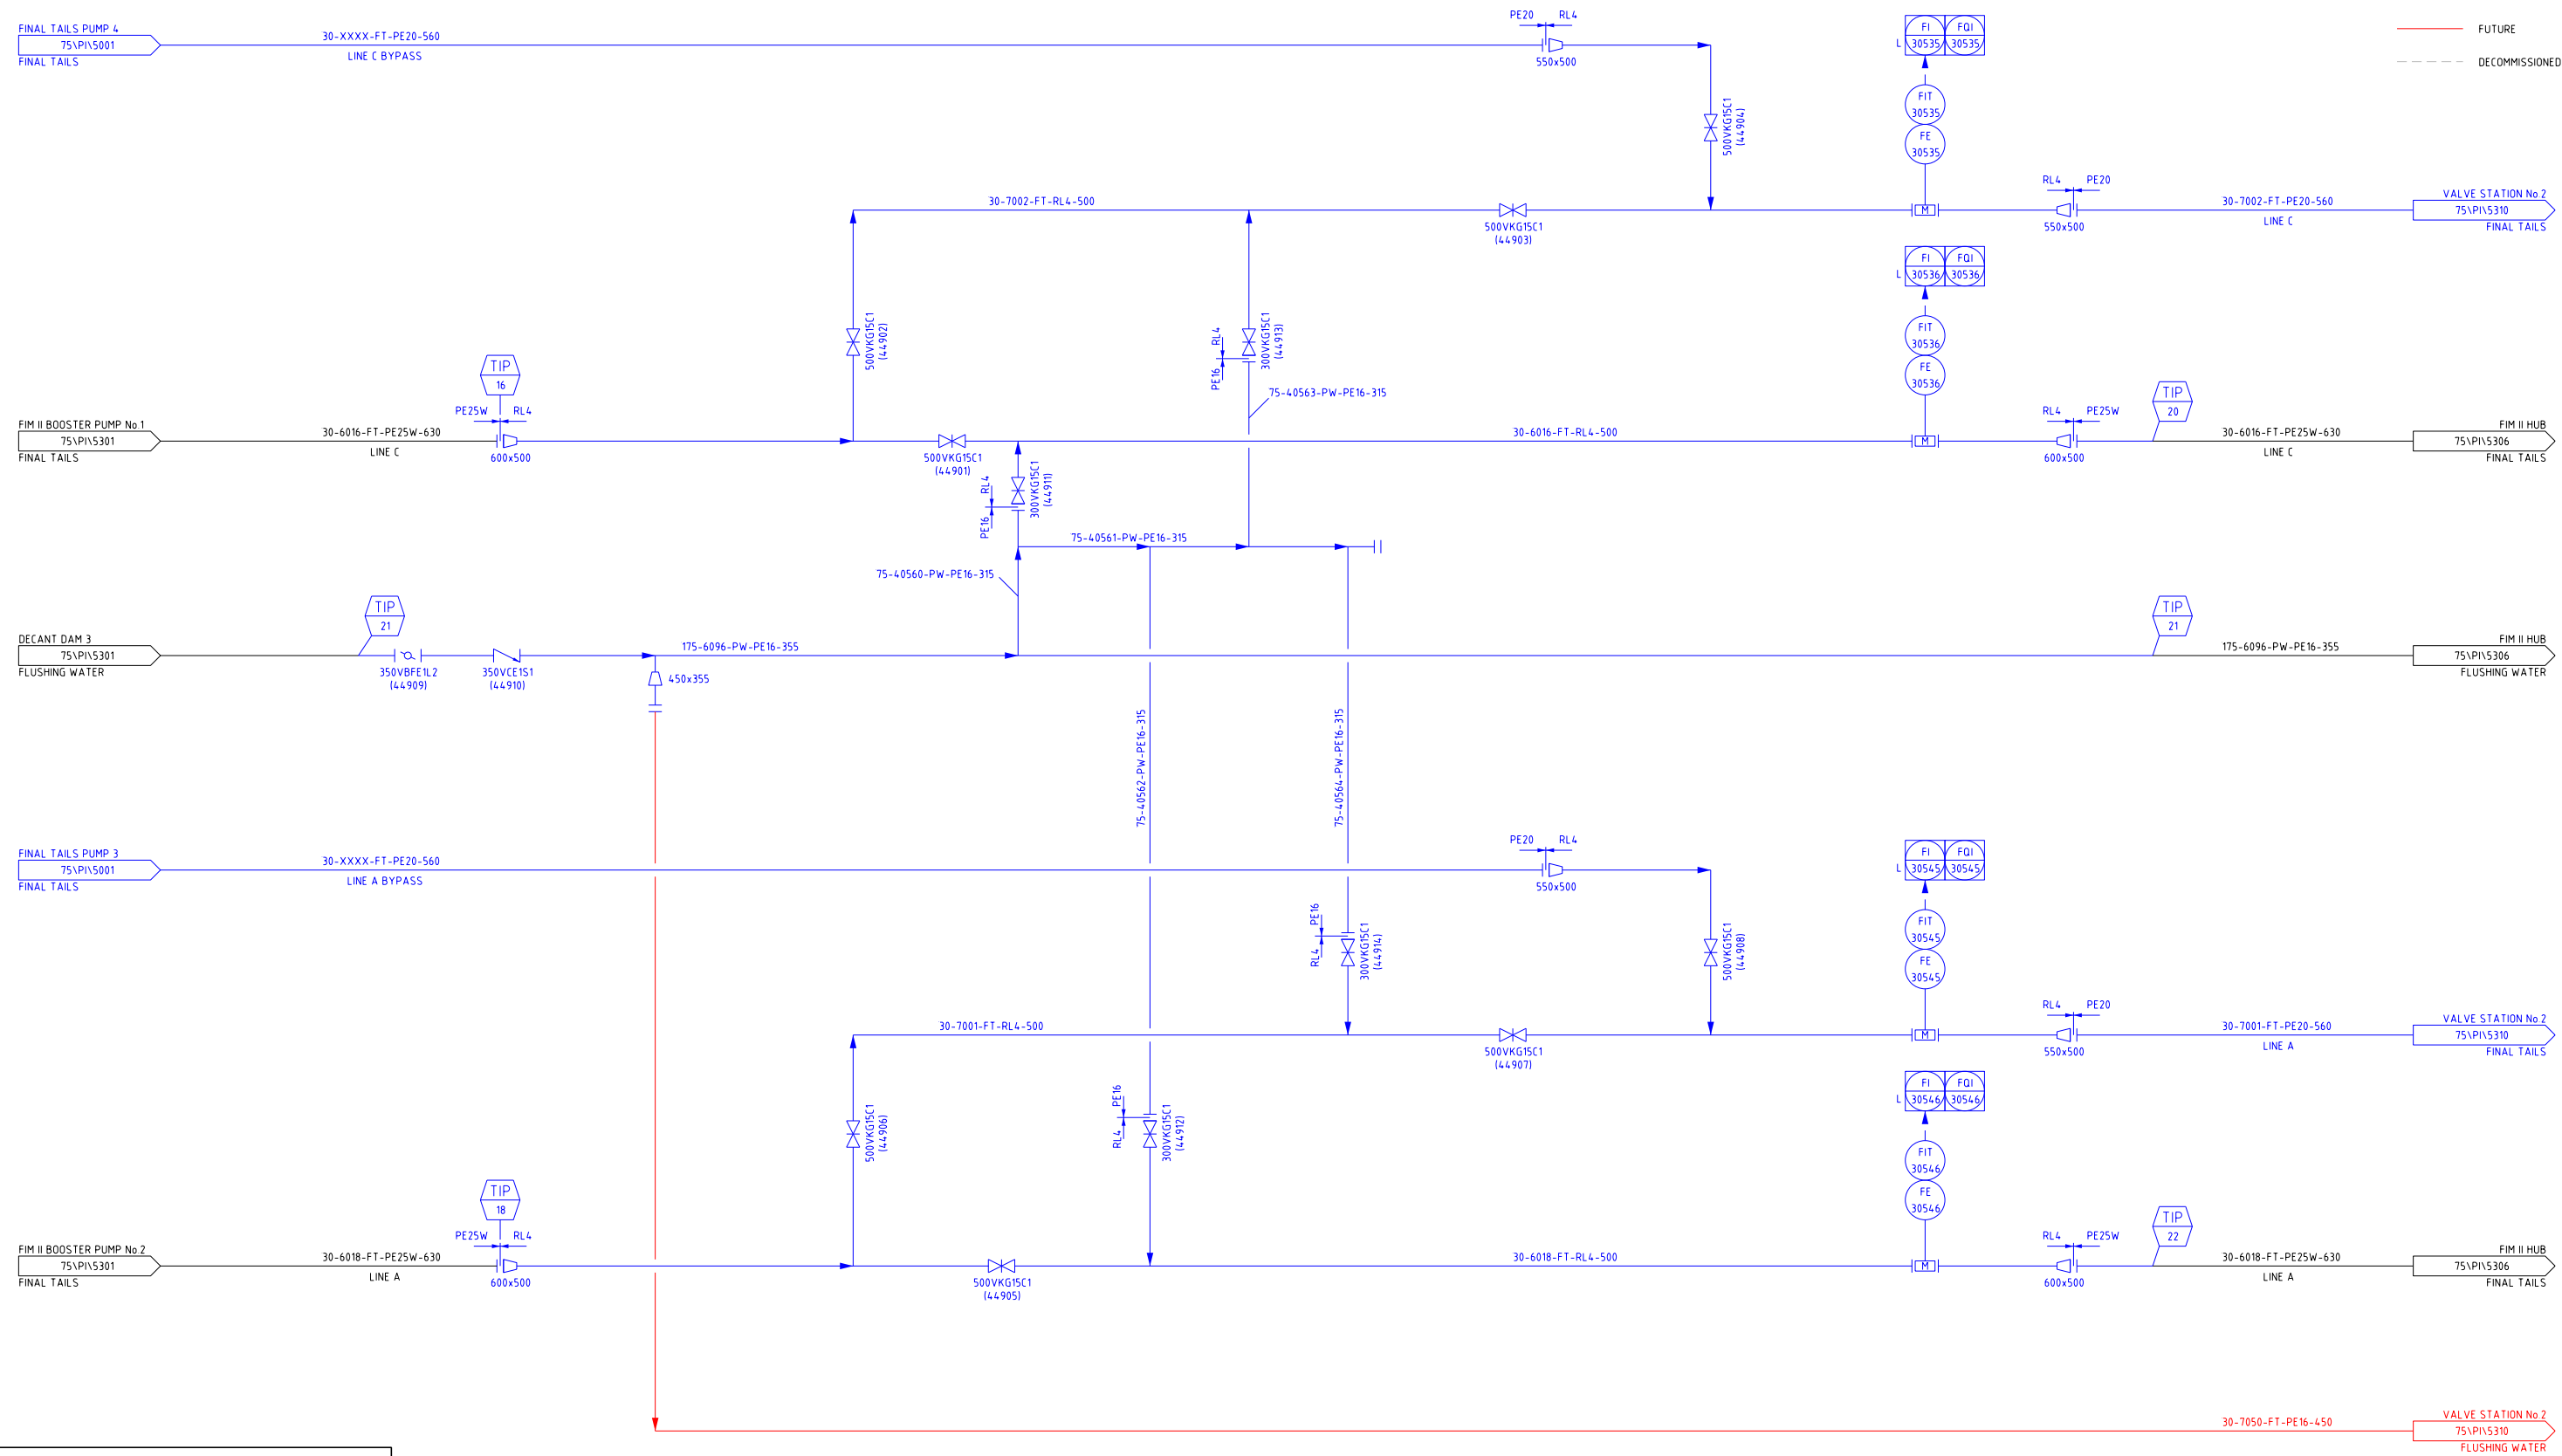

APPROVED FOR
CONSTRUCTION