


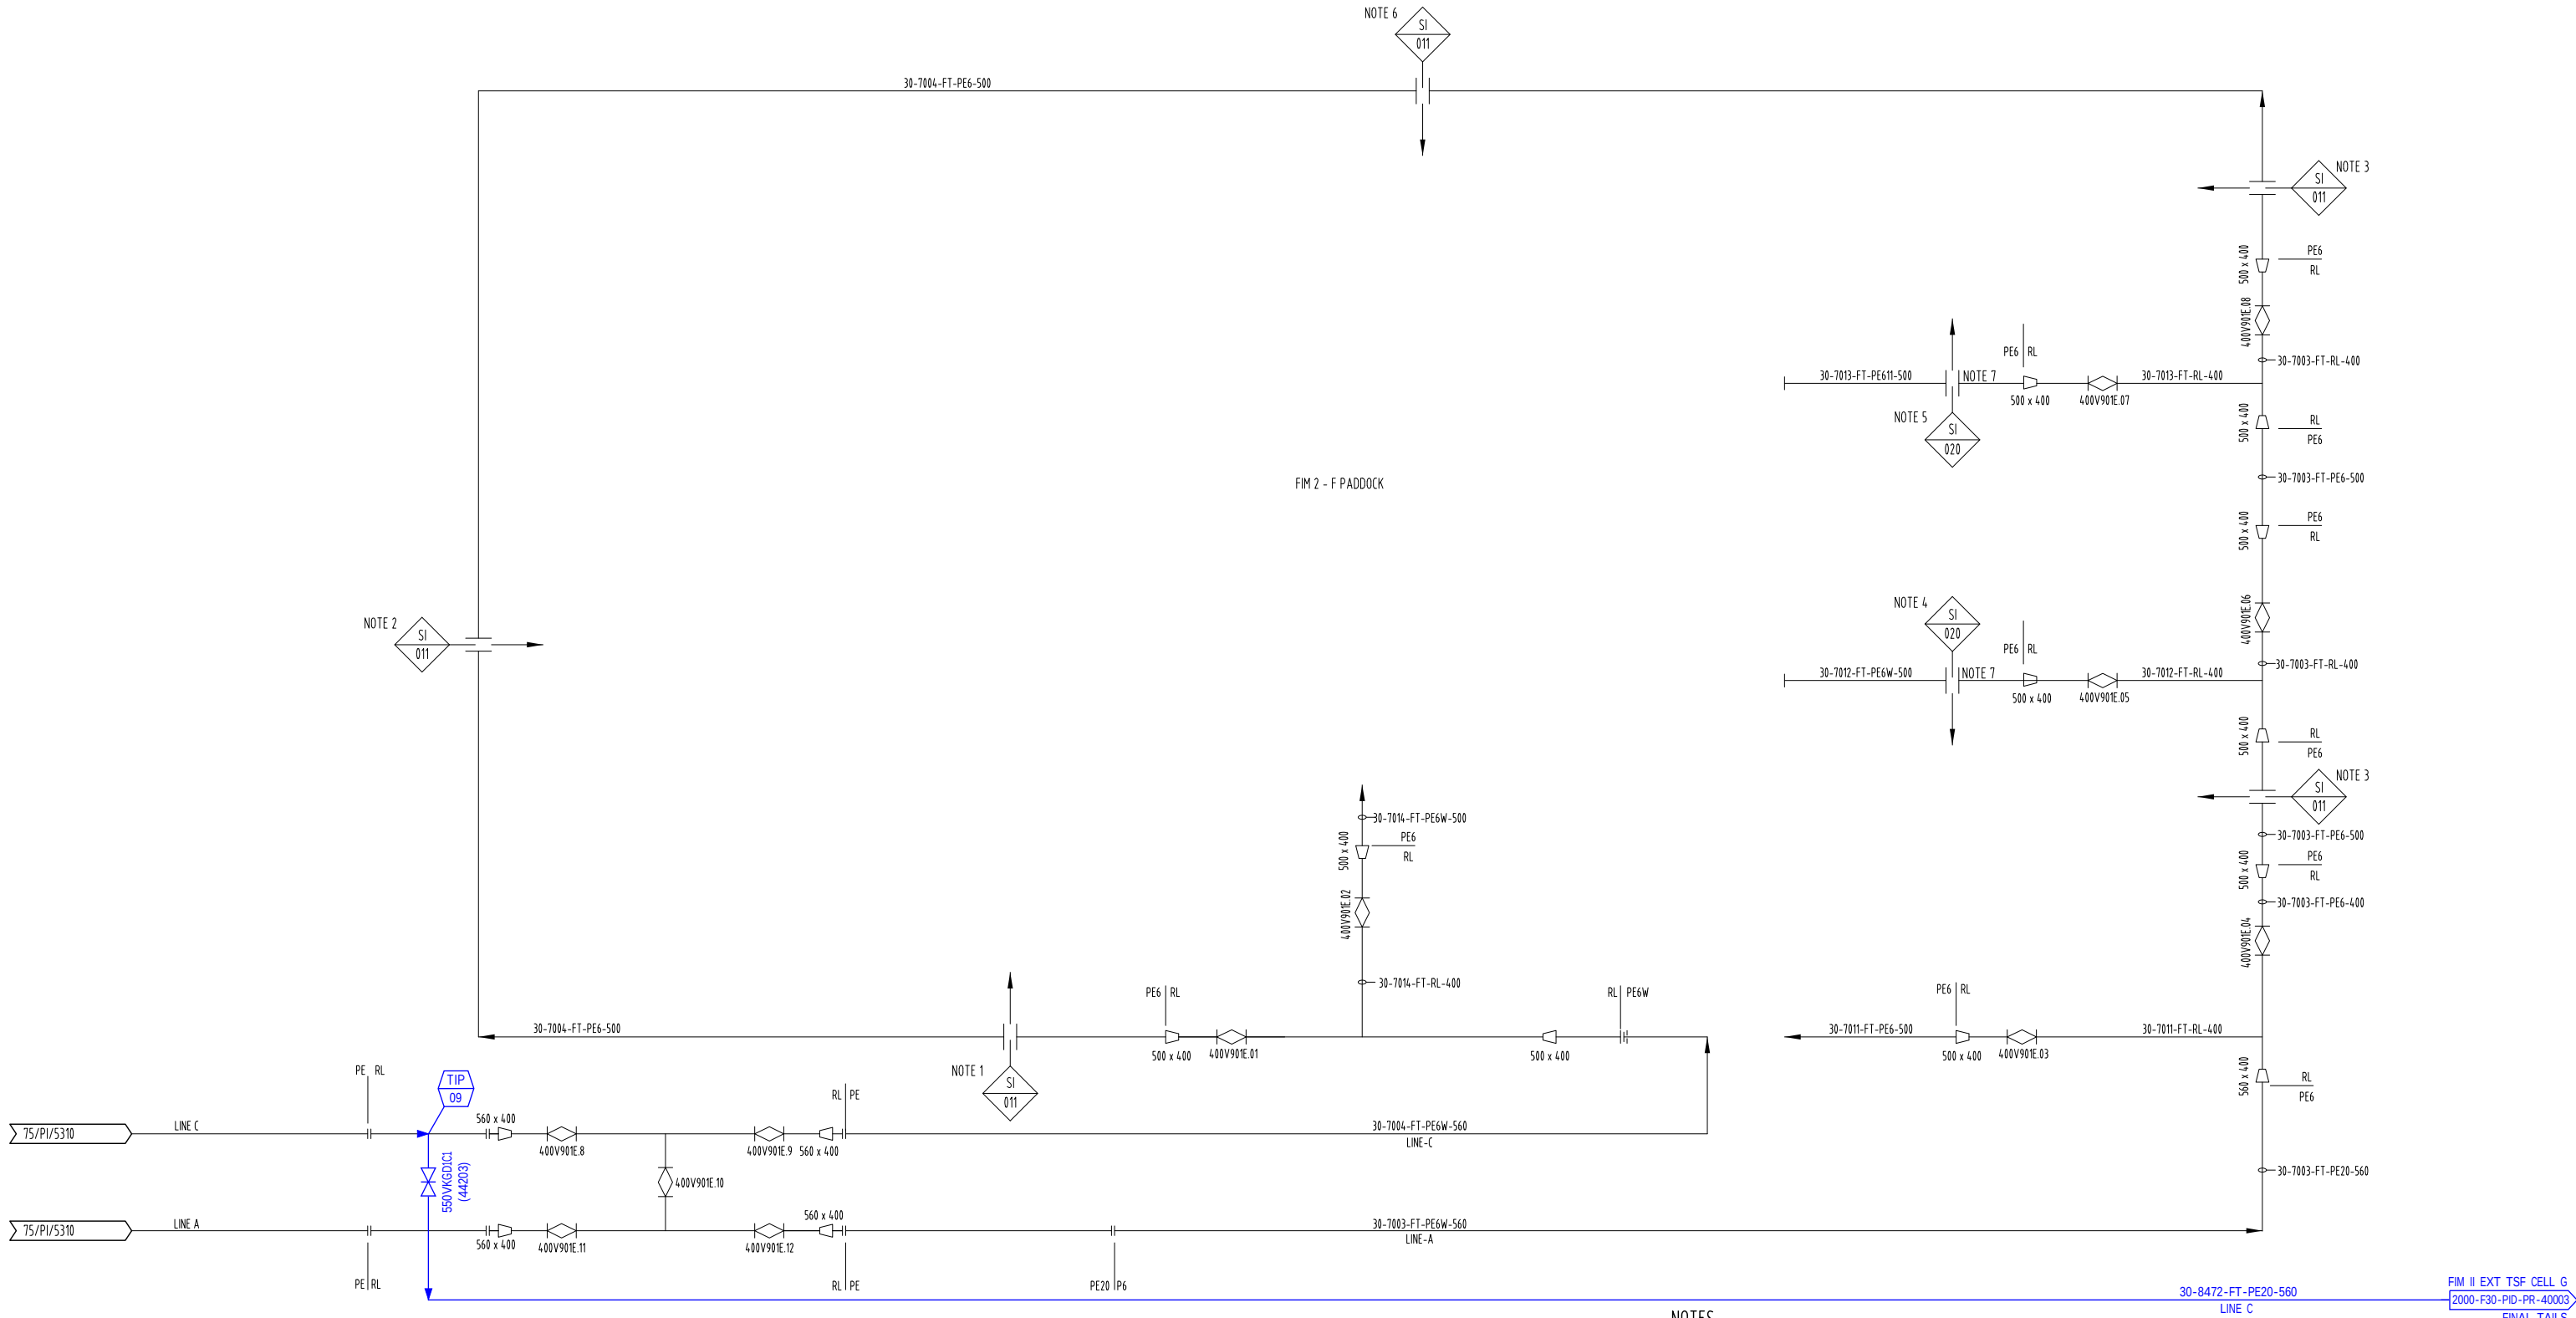

FIM 2 - F PADDOCK

LEGEND:

EXISTING

NEW

NOTES

1. SPIGOTS SPACED AT 40m CENTRES DISCHARGING ON THE SOUTHERN WALL
2. SPIGOTS SPACED AT 40m CENTRES DISCHARGING ON THE WESTERN WALL
3. SPIGOTS SPACED AT 40m CENTRES DISCHARGING ON THE WESTERN SIDE OF THE CENTRAL WALL
4. OUTLETS SPACED AT 15m CENTRES DISCHARGING ON THE SOUTHERN SIDE OF THE CAUSEWAY
5. OUTLETS SPACED AT 15m CENTRES DISCHARGING ON THE NORTHERN SIDE OF THE CAUSEWAY
6. SPIGOTS SPACED AT 40m CENTRES DISCHARGING ON THE NORTHER
7. CAUSEWAY PIPING TO BE FLANGED EVERY 40m