


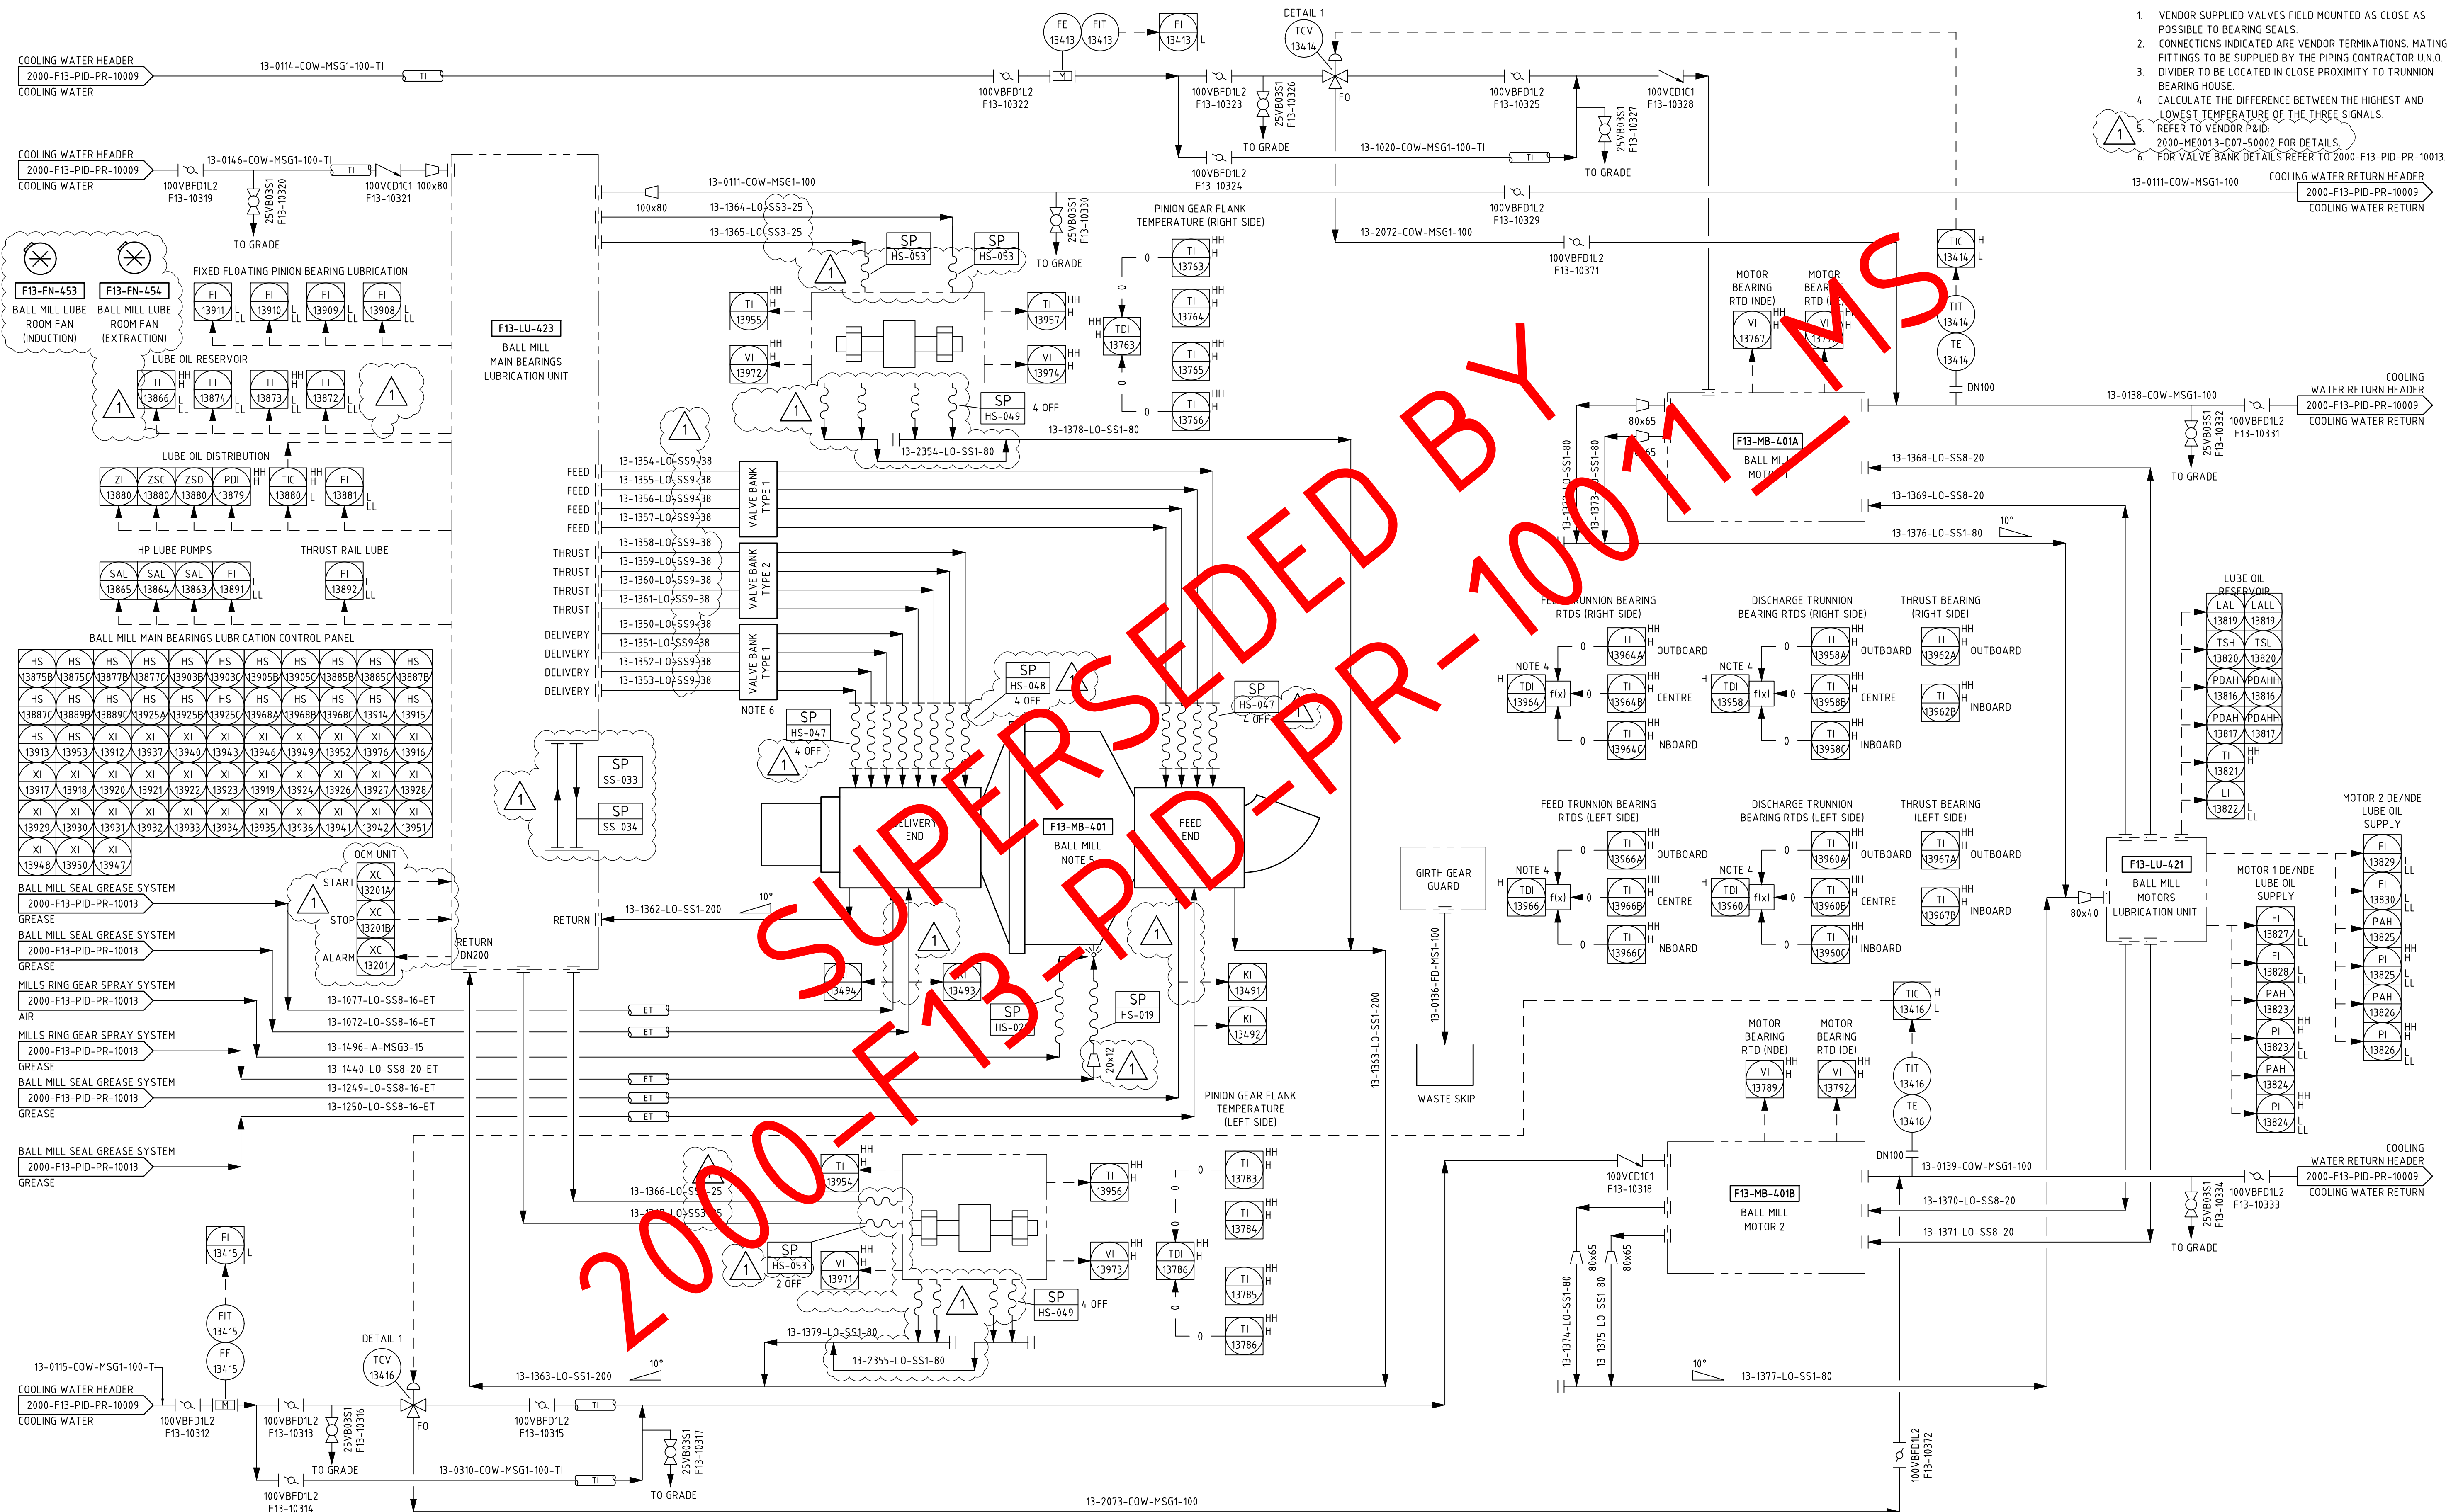

NOTES:

1. VENDOR SUPPLIED VALVES FIELD MOUNTED AS CLOSE AS POSSIBLE TO BEARING SEALS.
2. CONNECTIONS INDICATED ARE VENDOR TERMINATIONS. MATING FITTINGS TO BE SUPPLIED BY THE PIPING CONTRACTOR U.N.O.
3. DIVIDER TO BE LOCATED IN CLOSE PROXIMITY TO TRUNNION BEARING HOUSE.
4. CALCULATE THE DIFFERENCE BETWEEN THE HIGHEST AND LOWEST TEMPERATURE OF THE THREE SIGNALS.
5. REFER TO VENDOR P&ID:
2000-ME011-3-DP-50002 FOR DETAILS.
6. FOR VALVE BANK DETAILS REFER TO 2000-F13-PID-PR-10013.