


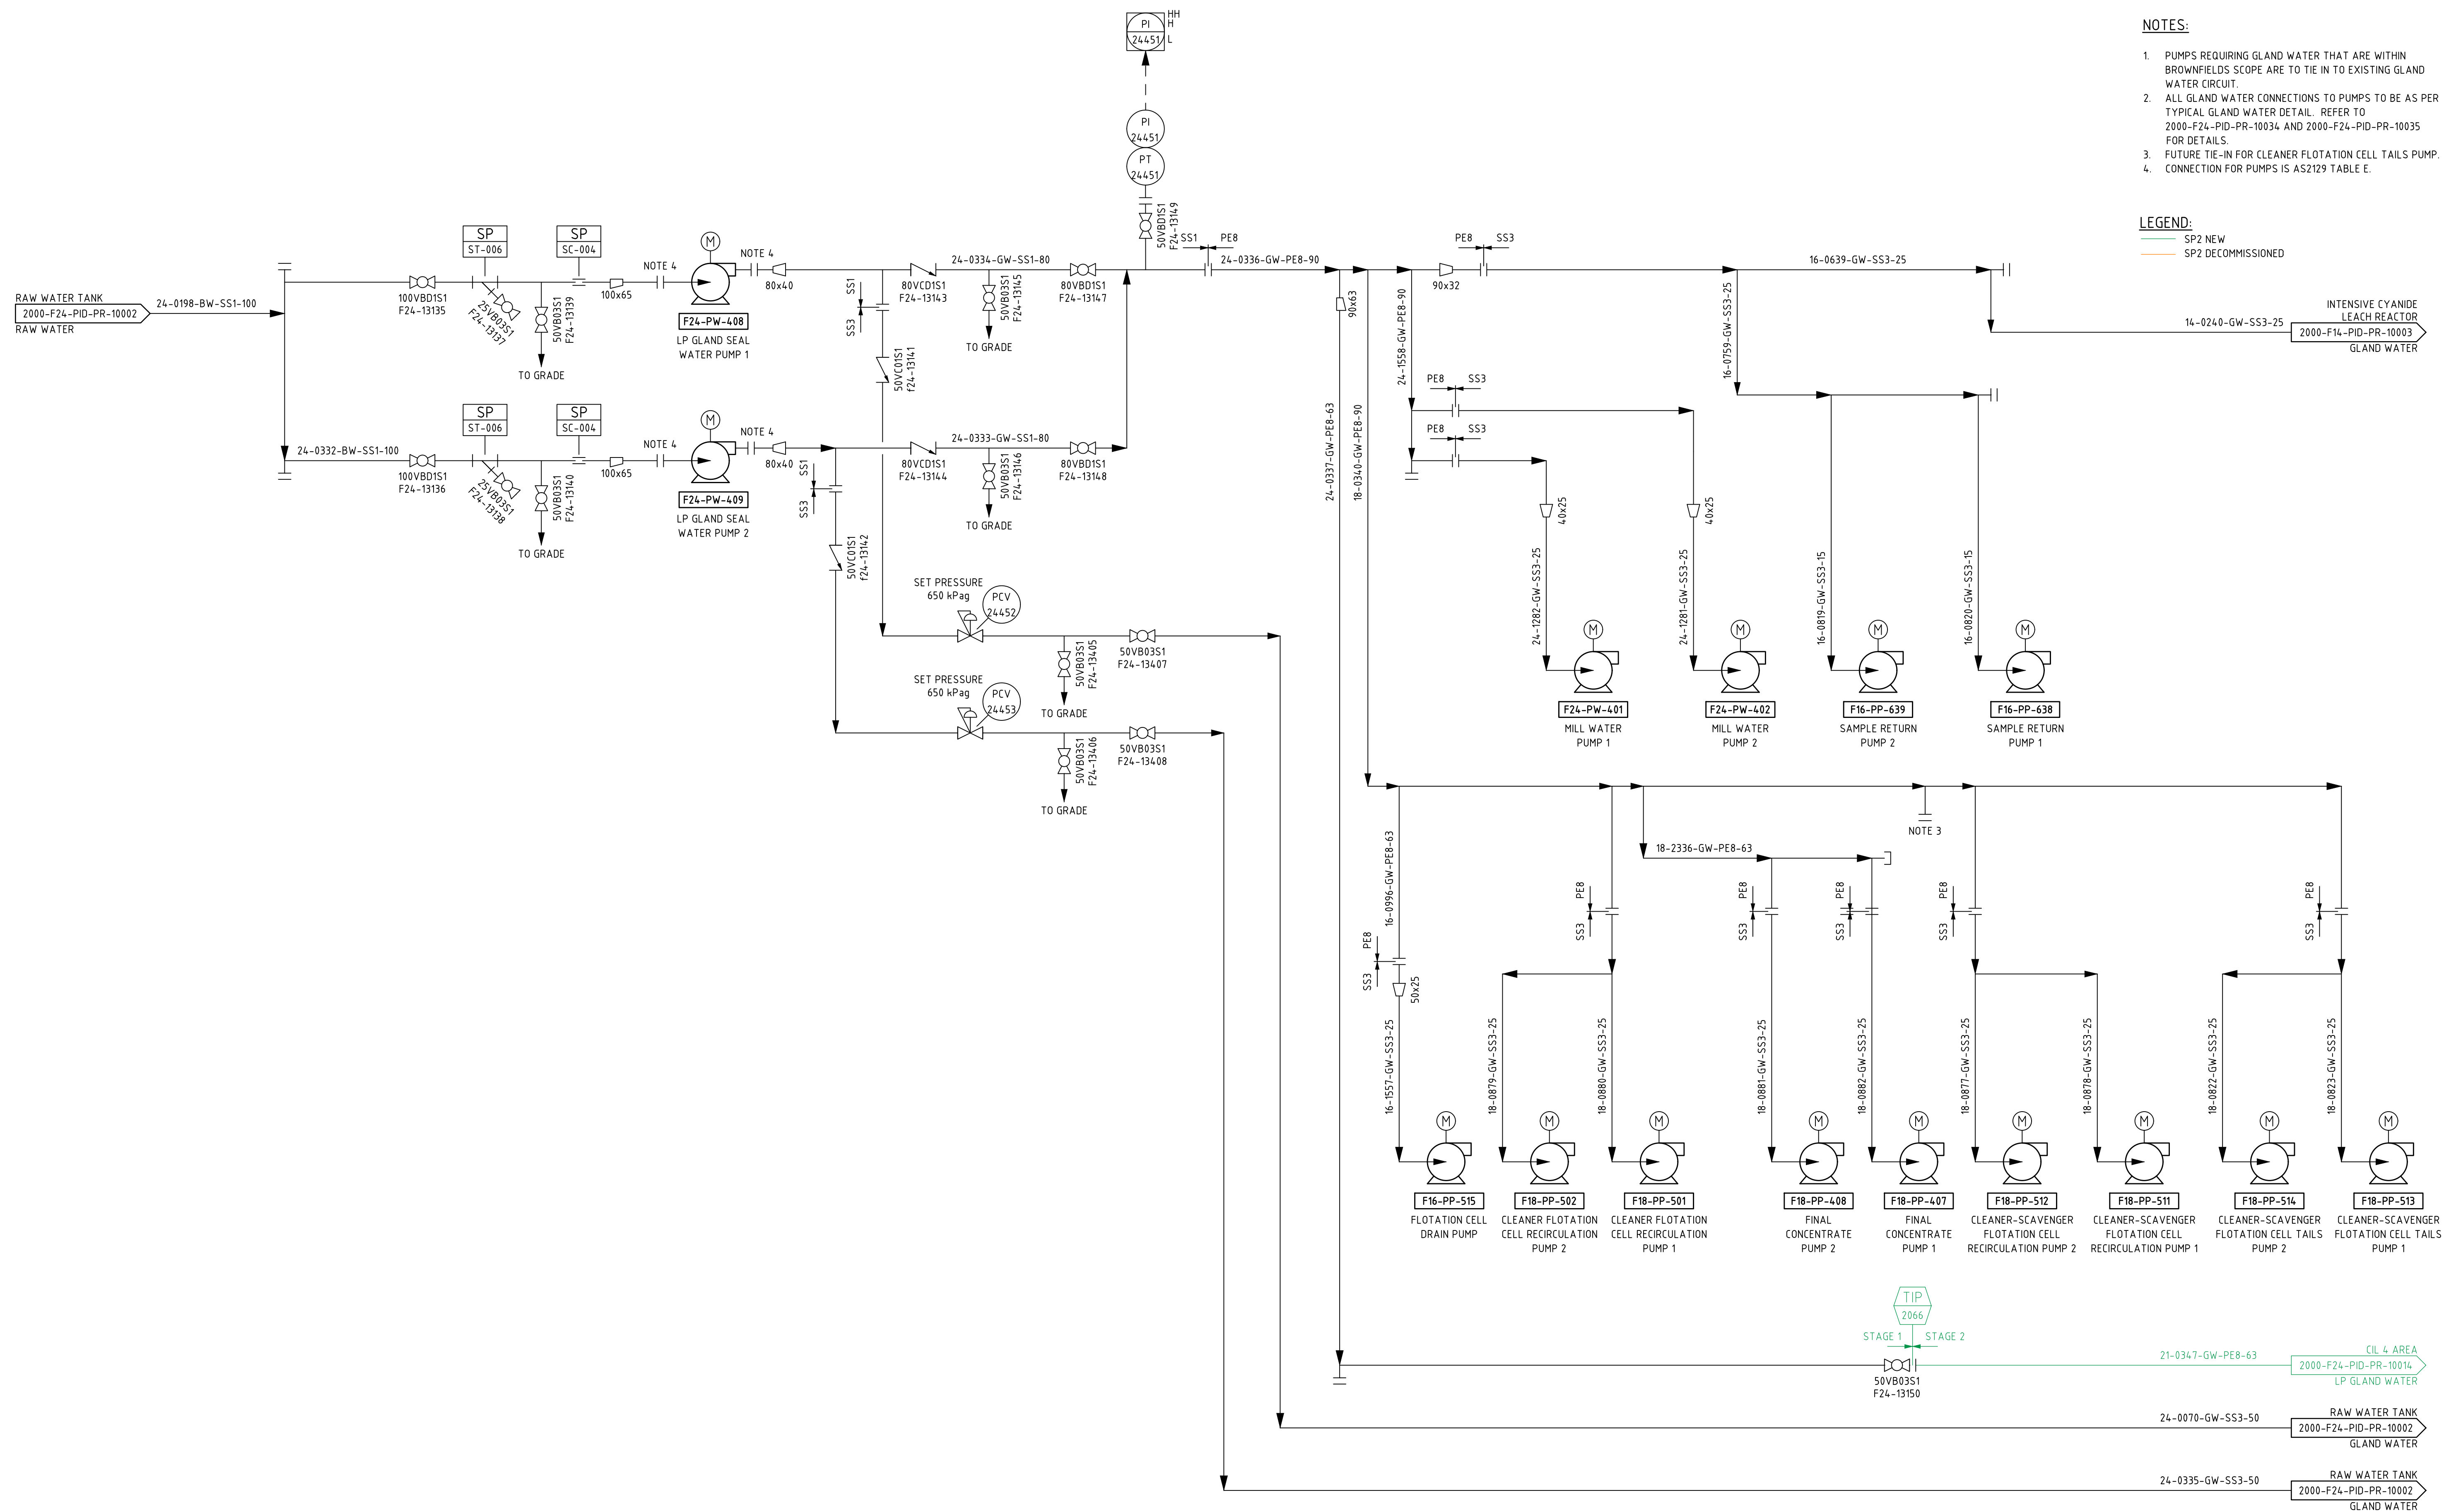

NOTES:

1. PUMPS REQUIRING GLAND WATER THAT ARE WITHIN BROWNFIELDS SCOPE ARE TO TIE IN TO EXISTING GLAND WATER CIRCUIT.
2. ALL GLAND WATER CONNECTIONS TO PUMPS TO BE AS PER TYPICAL GLAND WATER DETAIL. REFER TO 2000-F24-PID-PR-10034 AND 2000-F24-PID-PR-10035 FOR DETAILS.
3. FUTURE TIE-IN FOR CLEANER FLOTATION CELL TAILS PUMP.
4. CONNECTION FOR PUMPS IS AS2129 TABLE E.

LEGEND:

- SP2 NEW
- SP2 DECOMMISSIONED