


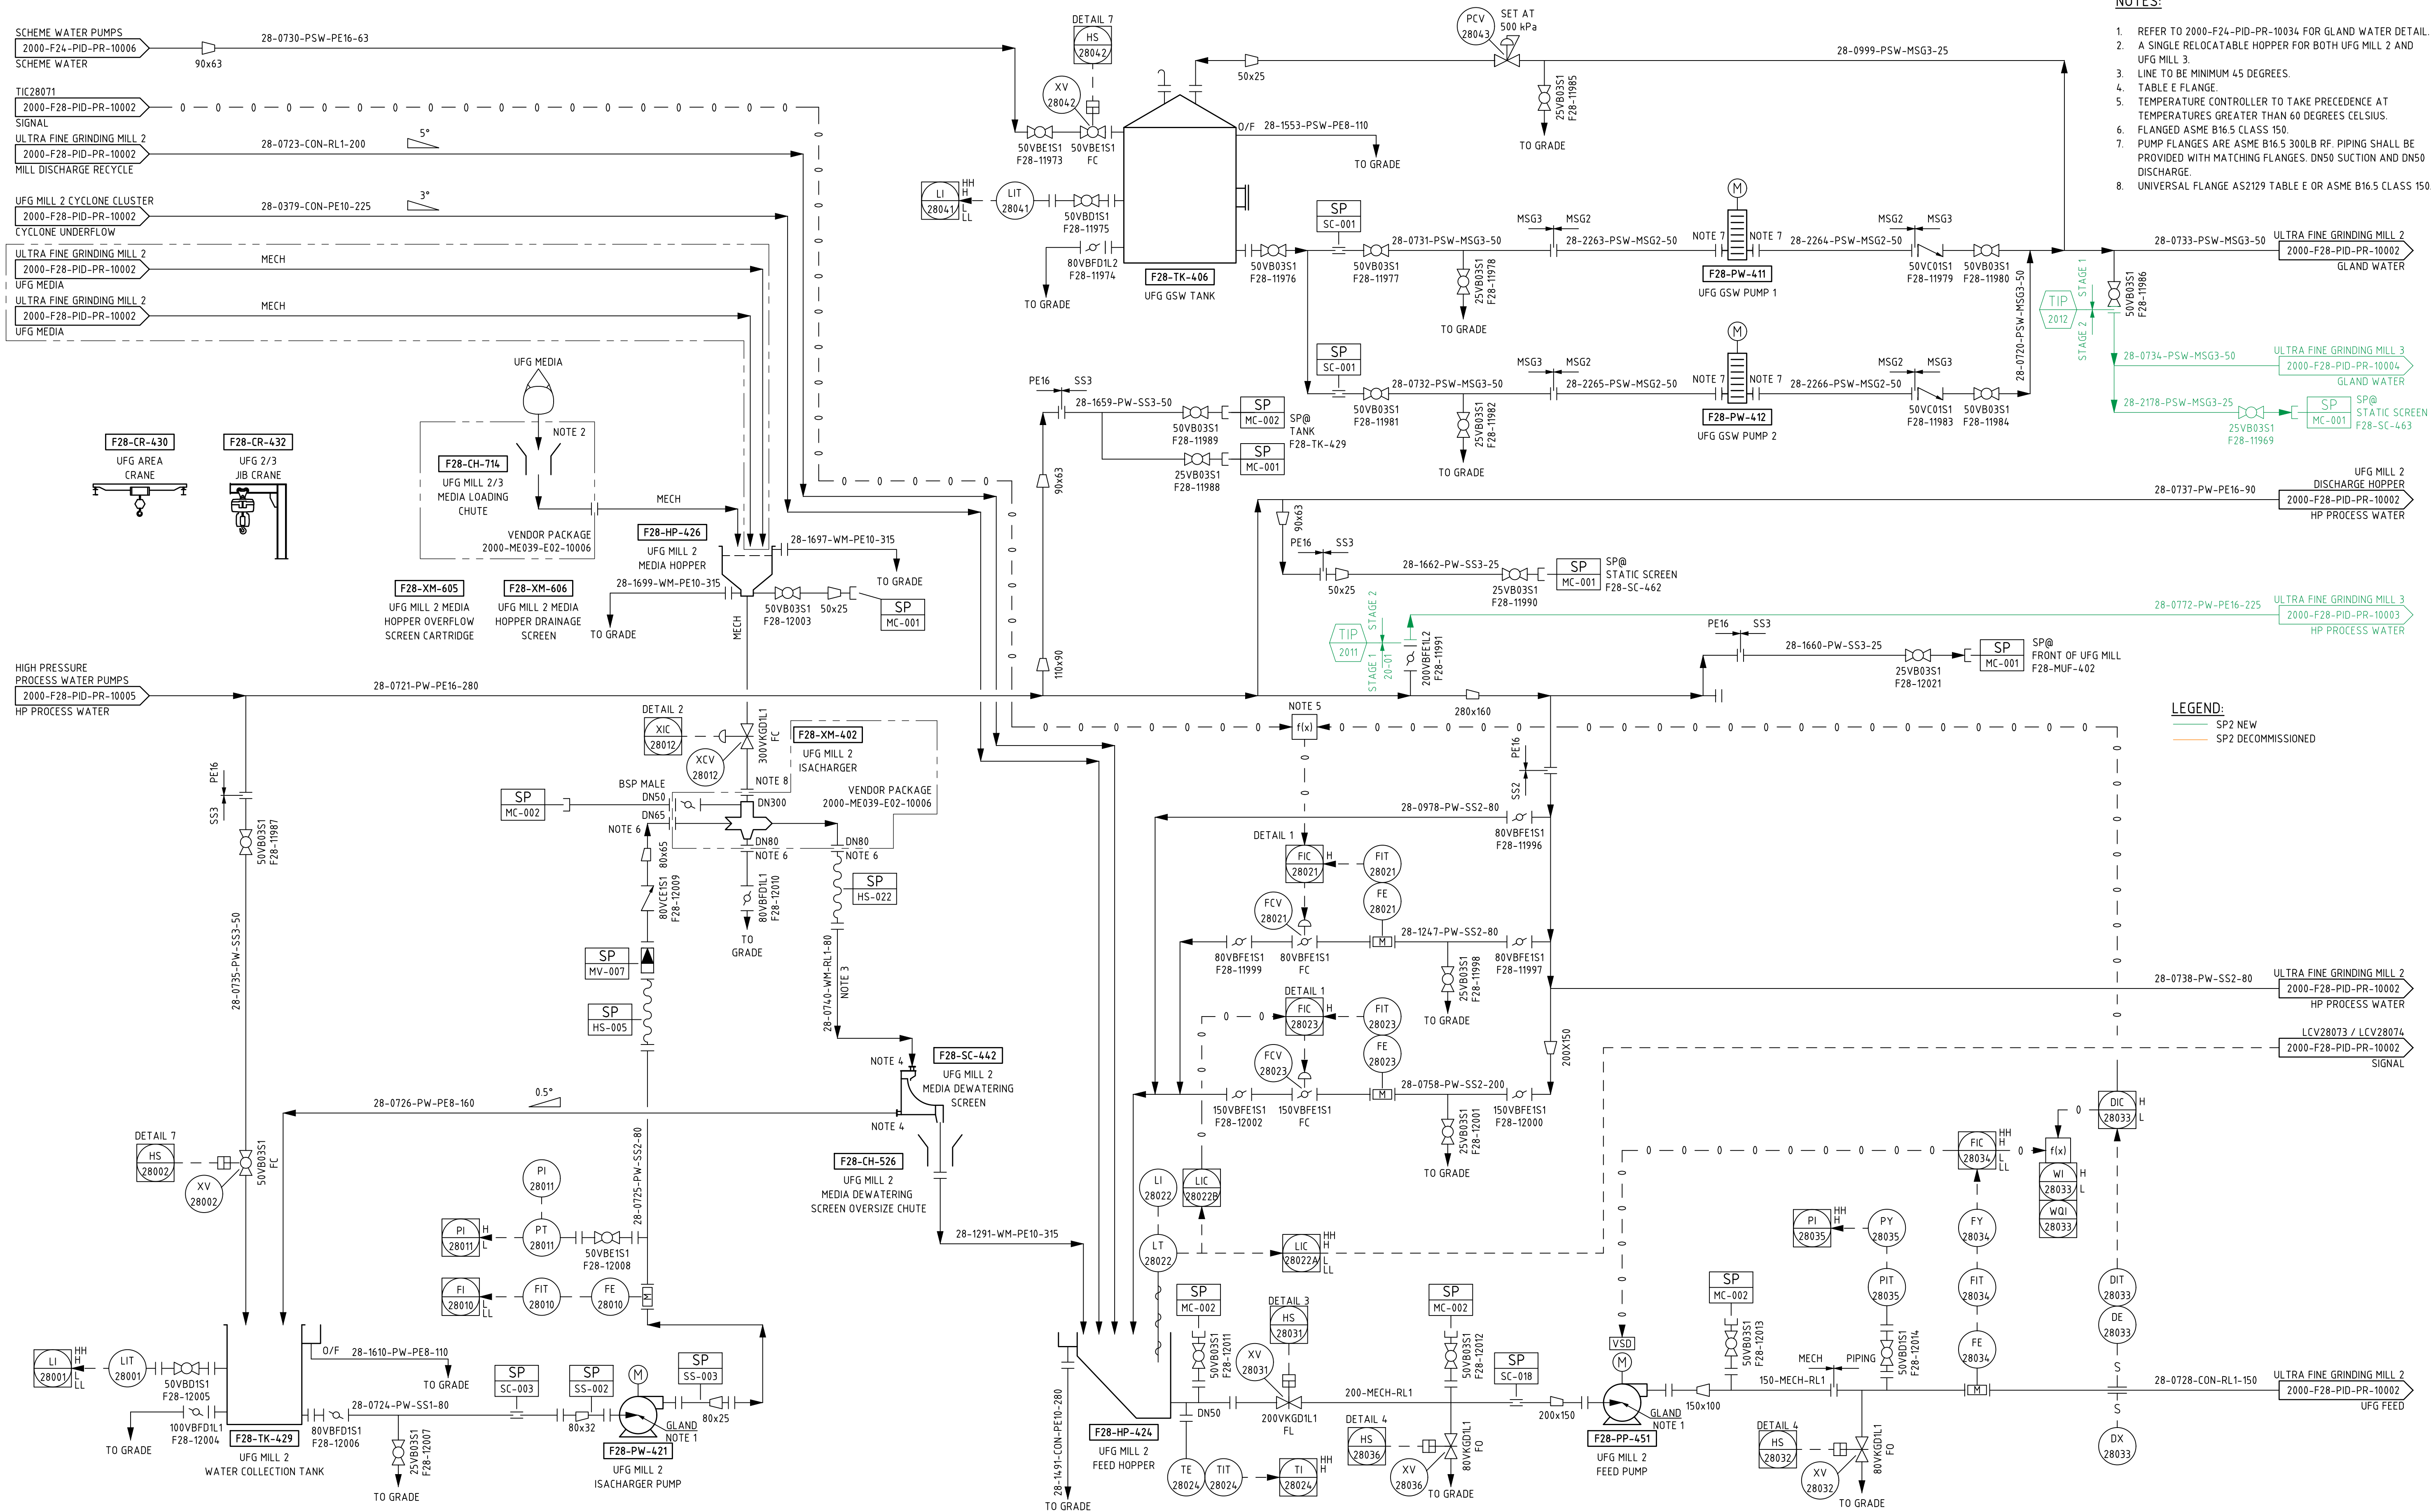

NOTES:

1. REFER TO 2000-F24-PID-PR-10034 FOR GLAND WATER DETAIL.
2. A SINGLE RELOCATABLE HOPPER FOR BOTH UFG MILL 2 AND UFG MILL 3.
3. LINE TO BE MINIMUM 45 DEGREES.
4. TABLE E FLANGE.
5. TEMPERATURE CONTROLLER TO TAKE PRECEDENCE AT TEMPERATURES GREATER THAN 60 DEGREES CELSIUS.
6. FLANGED ASME B16.5 CLASS 150.
7. PUMP FLANGES ARE ASME B16.5 300LB RF. PIPING SHALL BE PROVIDED WITH MATCHING FLANGES. DN50 SUCTION AND DN50 DISCHARGE.
8. UNIVERSAL FLANGE AS2129 TABLE E OR ASME B16.5 CLASS 150.

LEGEND:

- SP2 NEW
- SP2 DECOMMISSIONED