


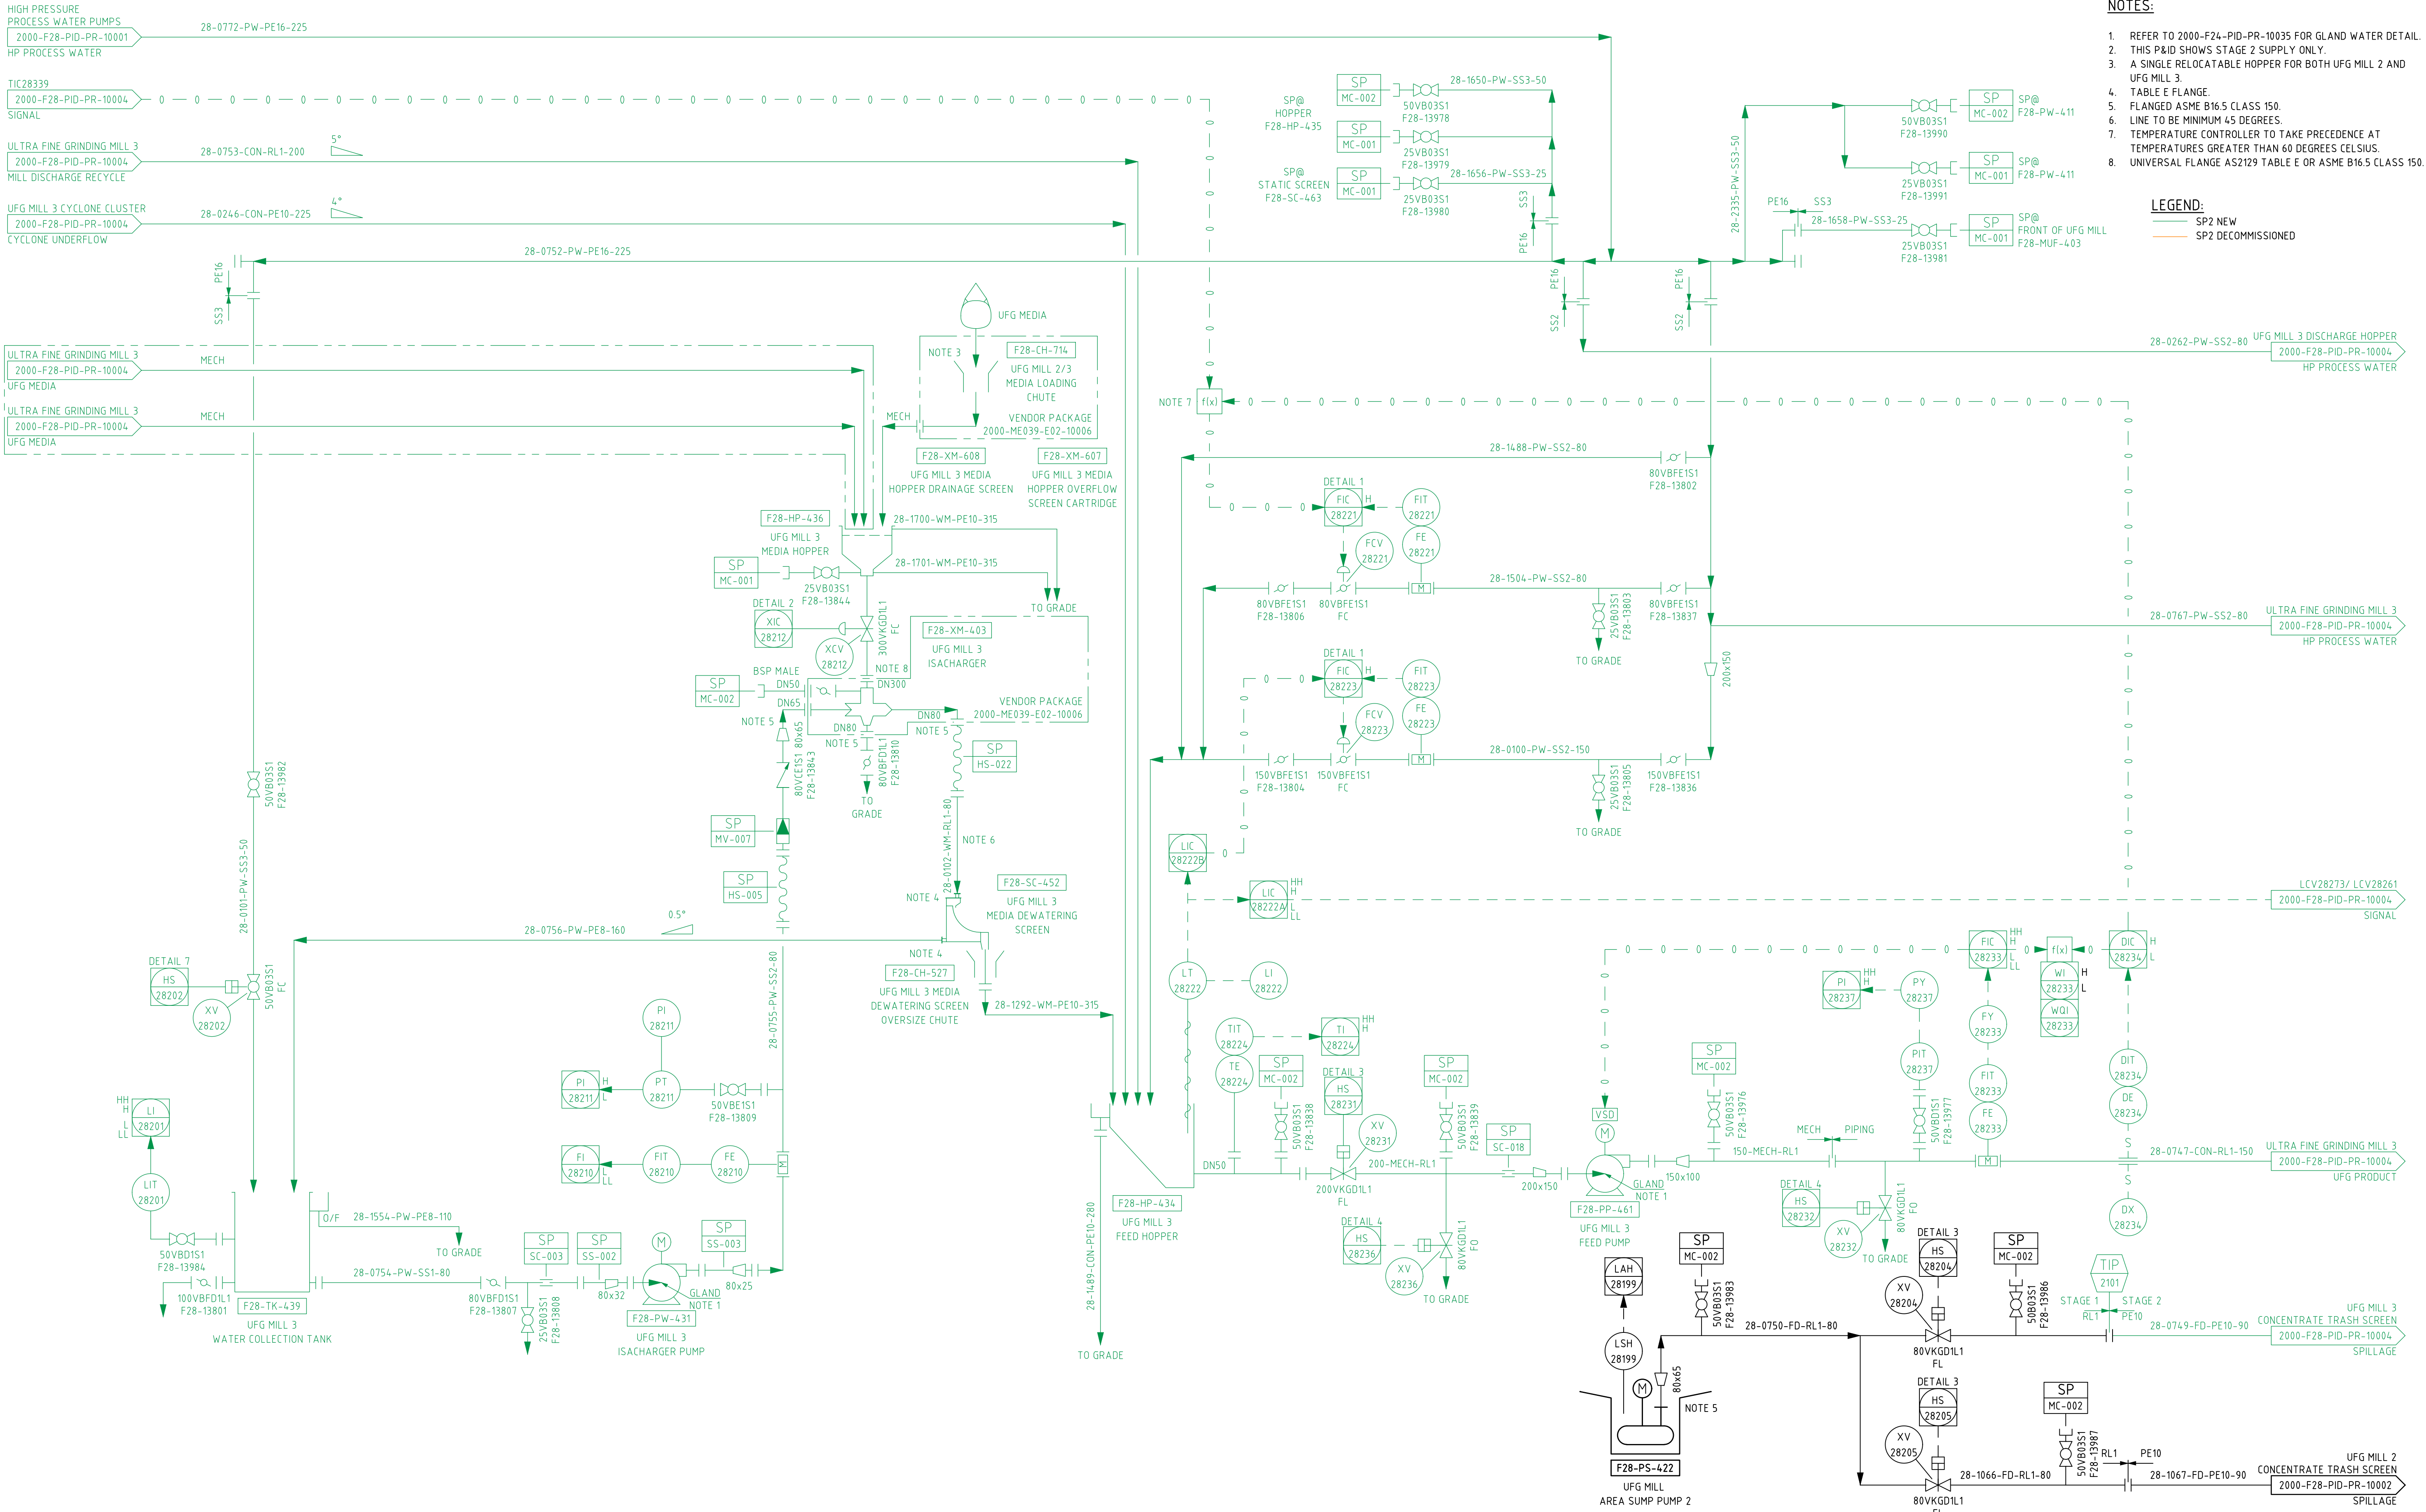

NOTES:

1. REFER TO 2000-F24-PID-PR-10035 FOR GLAND WATER DETAIL.
2. THIS P&ID SHOWS STAGE 2 SUPPLY ONLY.
3. A SINGLE RELOCATABLE HOPPER FOR BOTH UFG MILL 2 AND UFG MILL 3.
4. TABLE E FLANGE.
5. FLANGED ASME B16.5 CLASS 150.
6. LINE TO BE MINIMUM 45 DEGREES.
7. TEMPERATURE CONTROLLER TO TAKE PRECEDENCE AT TEMPERATURES GREATER THAN 60 DEGREES CELSIUS.
8. UNIVERSAL FLANGE AS2129 TABLE E OR ASME B16.5 CLASS 150.

LEGEND:

- SP2 NEW
- SP2 DECOMMISSIONED