

FME-75-PI-461 35-607-PSW-PE16-050
UFG CIRCUIT PROCESS WATER DISTRIBUTION
35-PI-0701-SK-01

35-8026-PSW-PE16-063

PE-63

MOVED TO 2000-F35-PID-PR-60005

FME-35-PI-444 35-613-PSW-PE16-032

FME-35-PI-446 FROM BELT FILTER CHUTE

FME-35-PI-445 FROM BELT FILTER CHUTE

FME-35-PI-445 35-603-FD-PE16-063

NOTES

- 1 THIS PID DETAILS MODIFICATIONS REQUIRED TO EXISTING DRAWING 35-PI-0447.
- 2 TAKEOFF FOR FUTURE TRUCK WASH.
- 3 EXISTING PULL WIRE BEING MODIFIED, INSTRUMENT JUNCTION BOX REMAINING IN SITU.

HOLDS

HOLD-001 REQUIREMENT TO BE CONFIRMED.


LEGENDS

DECOMMISSION
EXISTING
NEW

F35-CV-18 CONCENTRATE STOCKPILE FEED CONVEYOR 2
F35-PS-64 CONCENTRATE STOCKPILE SUMP PUMP
F35-WD-18 CONCENTRATE STOCKPILE BELT WEIGHER
F35-CV-17 CONCENTRATE STOCKPILE FEED CONVEYOR
F35-CH-01 CONCENTRATE STOCKPILE FEED CONVEYOR TRANSFER CHUTE

APPROVED FOR

ENGINEERING PLEASE CHECK HOW
AS-BUILDS TIE INTO THIS PID

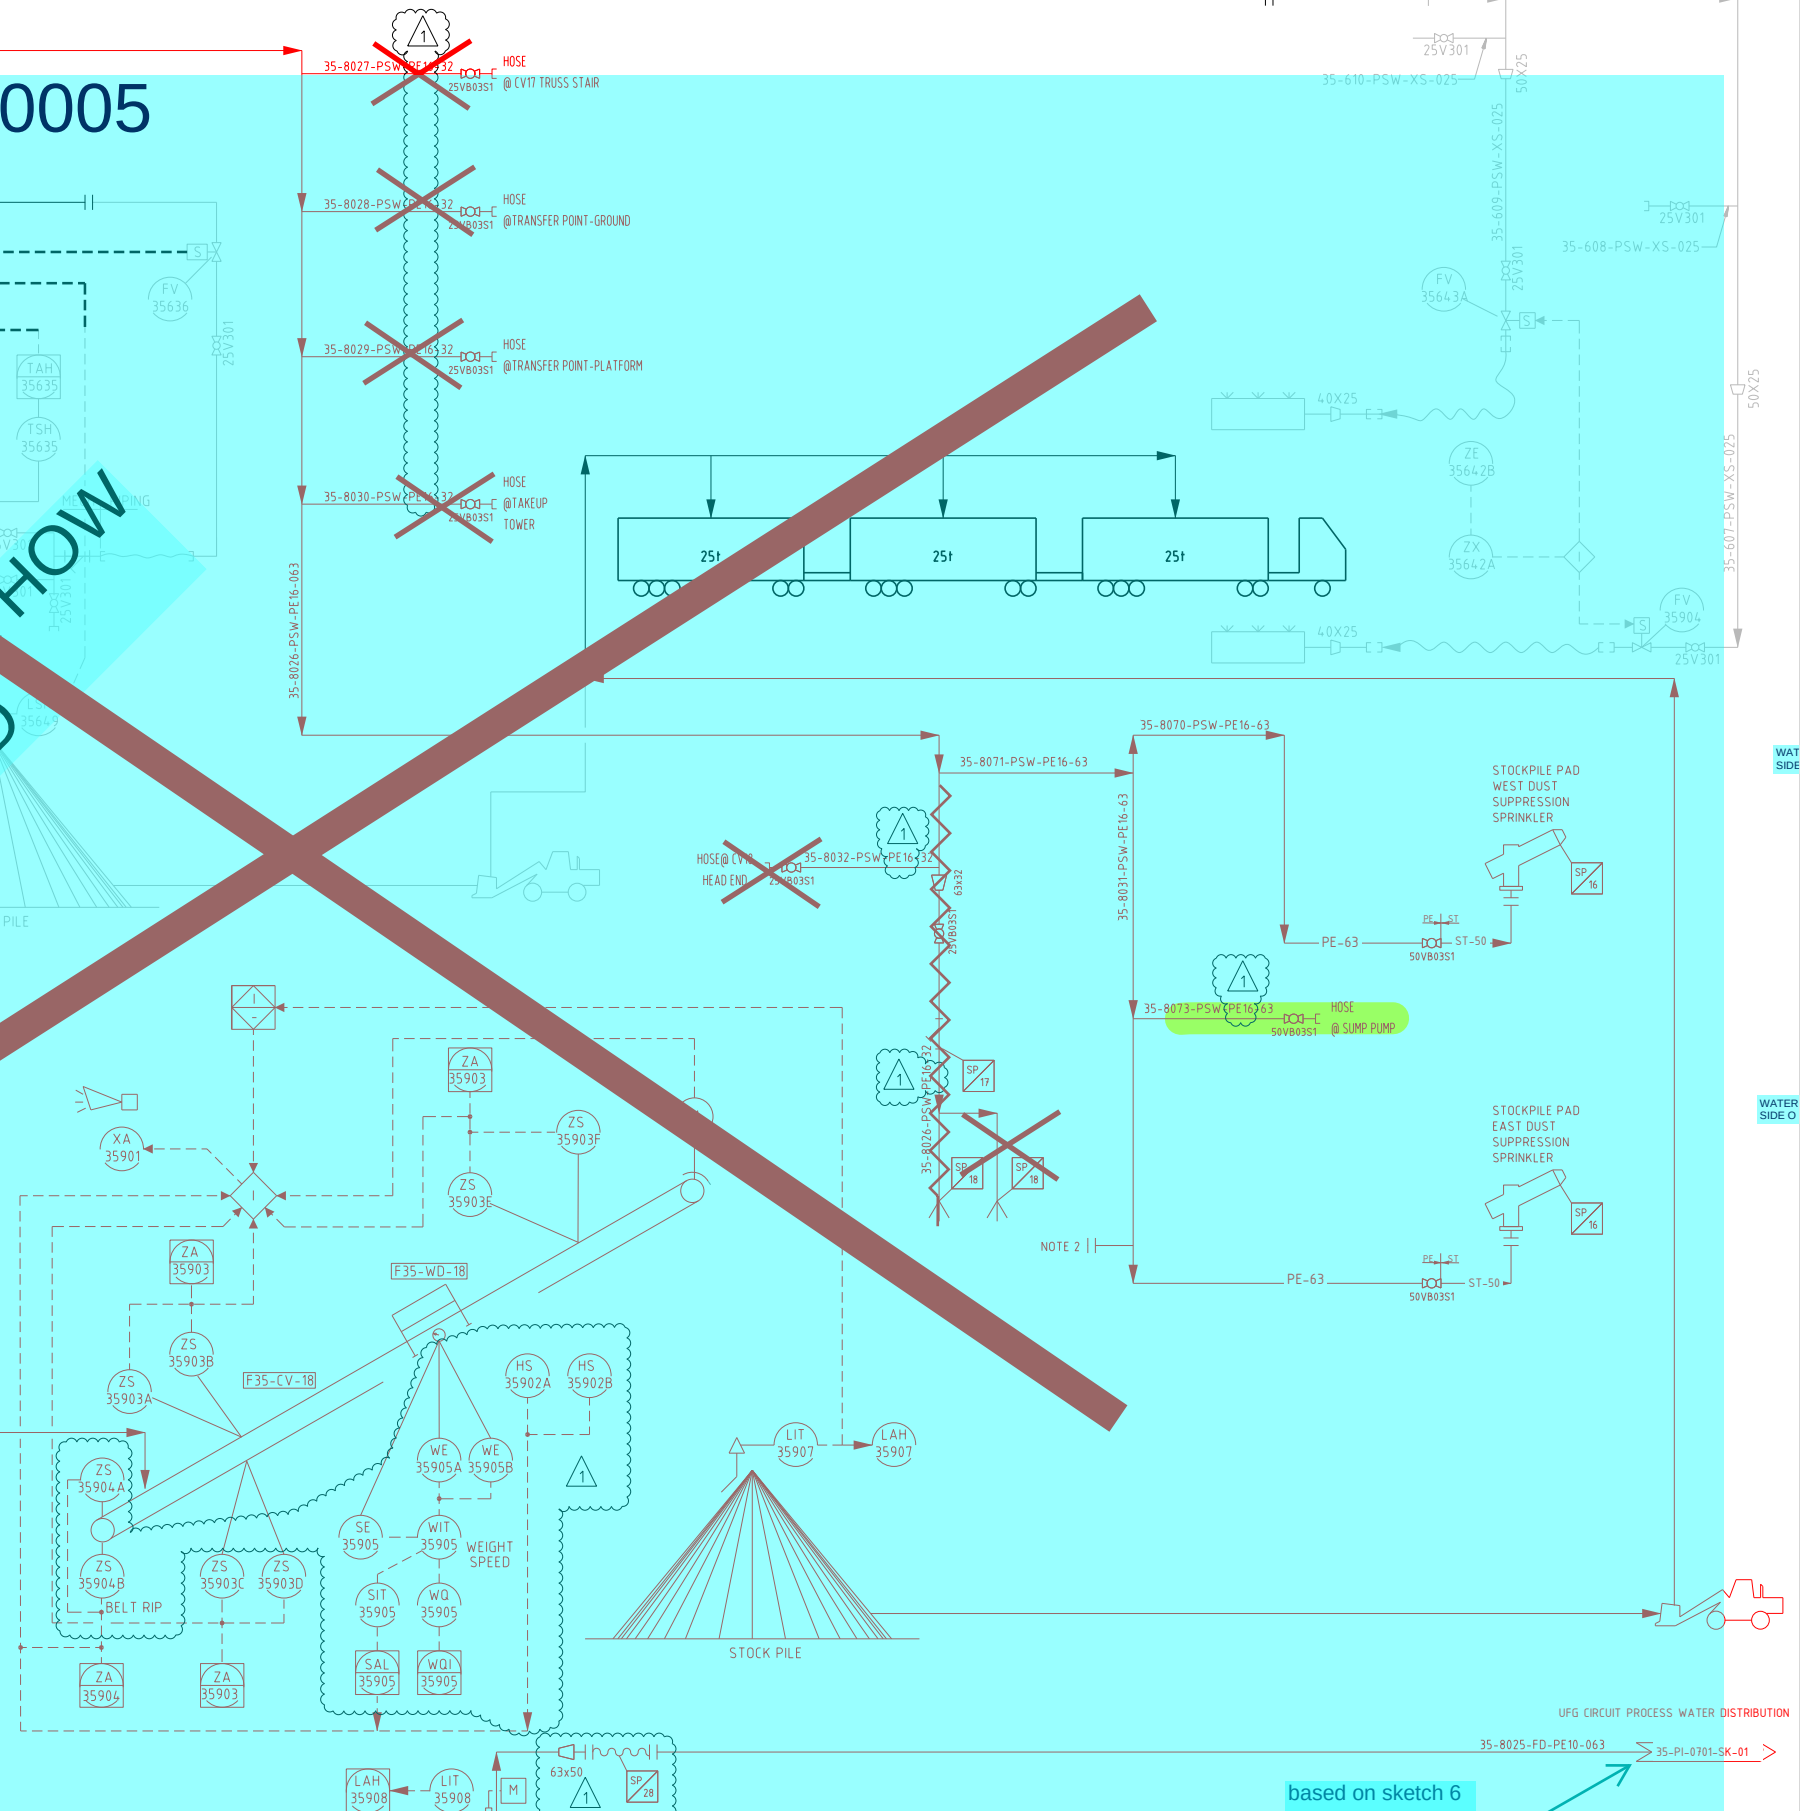

based on sketch 6