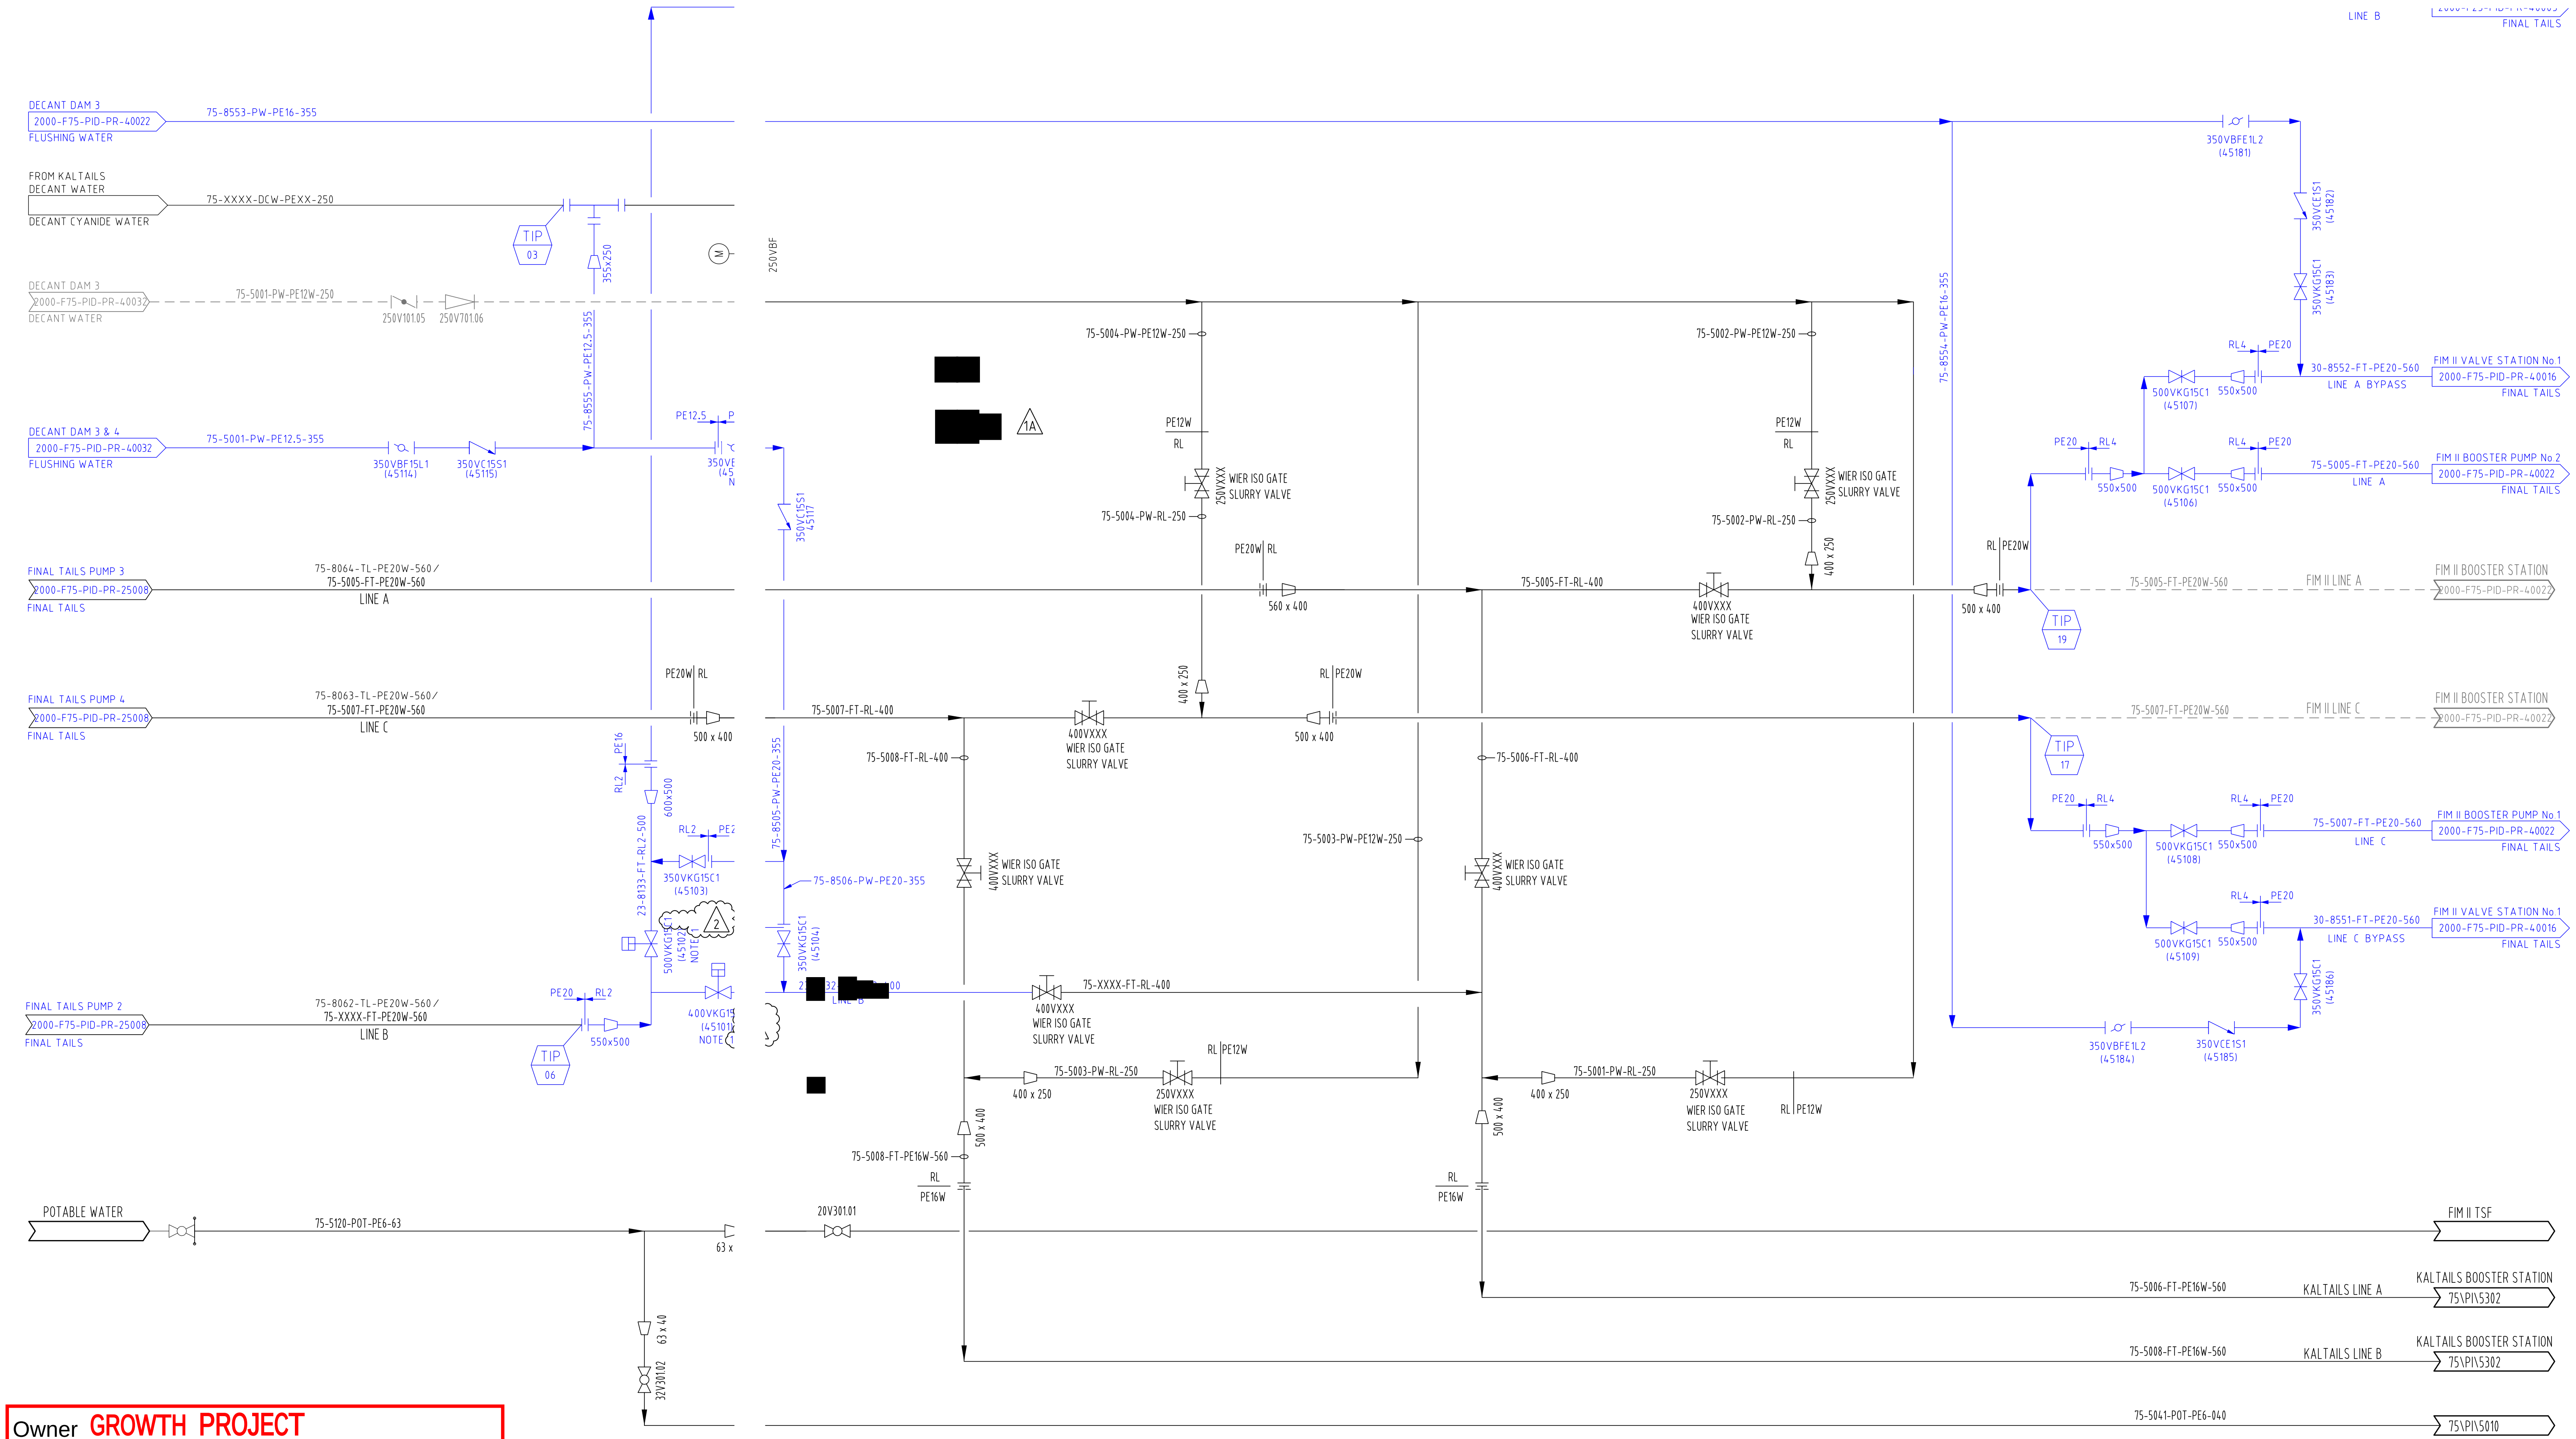

Owner **GROWTH PROJECT**

DRAWING NO.
2000-F75-PID-PR-40021

			DS	Initial
2	16DEC25	APPROVED FOR CONSTRUCTION	CS CS	MB
1A	11NOV25	ISSUED FOR INTERNAL AND CLIENT REVIEW	CS	TH
1	01MAY25	APPROVED FOR CONSTRUCTION	CS	TvB
0	05DEC24	APPROVED FOR CONSTRUCTION	CS	TvB
REV	DATE	DESCRIPTION	CHECK	TECH APP

LEGEND:

- EXISTING
- NEW
- FUTURE
- DECOMMISSIONED

NOTE
1. VA) BE PLARAD OPERATED. 2

[redacted]

														SCALE	NTS
						4	21 JULY 2019	GENERAL REVIS	JM						DRAWN	MAL	1.10.09
						3	06 APRIL 2018	FIM LOM TAILIN ICATIONS	JM						DESIGNED	JC	1.2.10
						2	15 NOV 2012	ISSUED FOR AS	GAO	AG					CHECKED	AJC	28.1.10
						1		GENERAL REVIS							APPROVED	JE	1.2.10
						0		ISSUED FOR CO ION	MAL	AJC	JC	JE			PROJ.APP		
MK	DATE	REVISION	BY	CKD	APP	MK	DATE	REVISION	BY	CKD	ENG CHK	APP	REFERENCE DRAWINGS	DWG NO.	PROJ. FILE #.		

SEDGMAN
Limited A.B.N. 86 088 471 667
© 2006

SEDGMAN DRG No. 0251-2-2-0010 SEDGMAN JOB No. 0251

FIMISTON PLANT
WATER TREATMENT FIMISTON
KALTAILS TSF RECOMMISSIONING
PIPING & INSTRUMENTATION DIAGRAM - KEARNS CORNER

SIZE	DRAWING NUMBER	REV
A1	75\PI\5001	4

KALGOORLIE CONSOLIDATED GOLD MINES PTY. LTD.
ABN 009 377 619 003

PLOT DATE: 22/02/10 - 09:43 - Cad File: P:\0251 - Kaltails Recommissioning\20 CAD\22\0251-2-2-0010.dwg [0251-2-2-0010] - Printed by: mark.lawson