



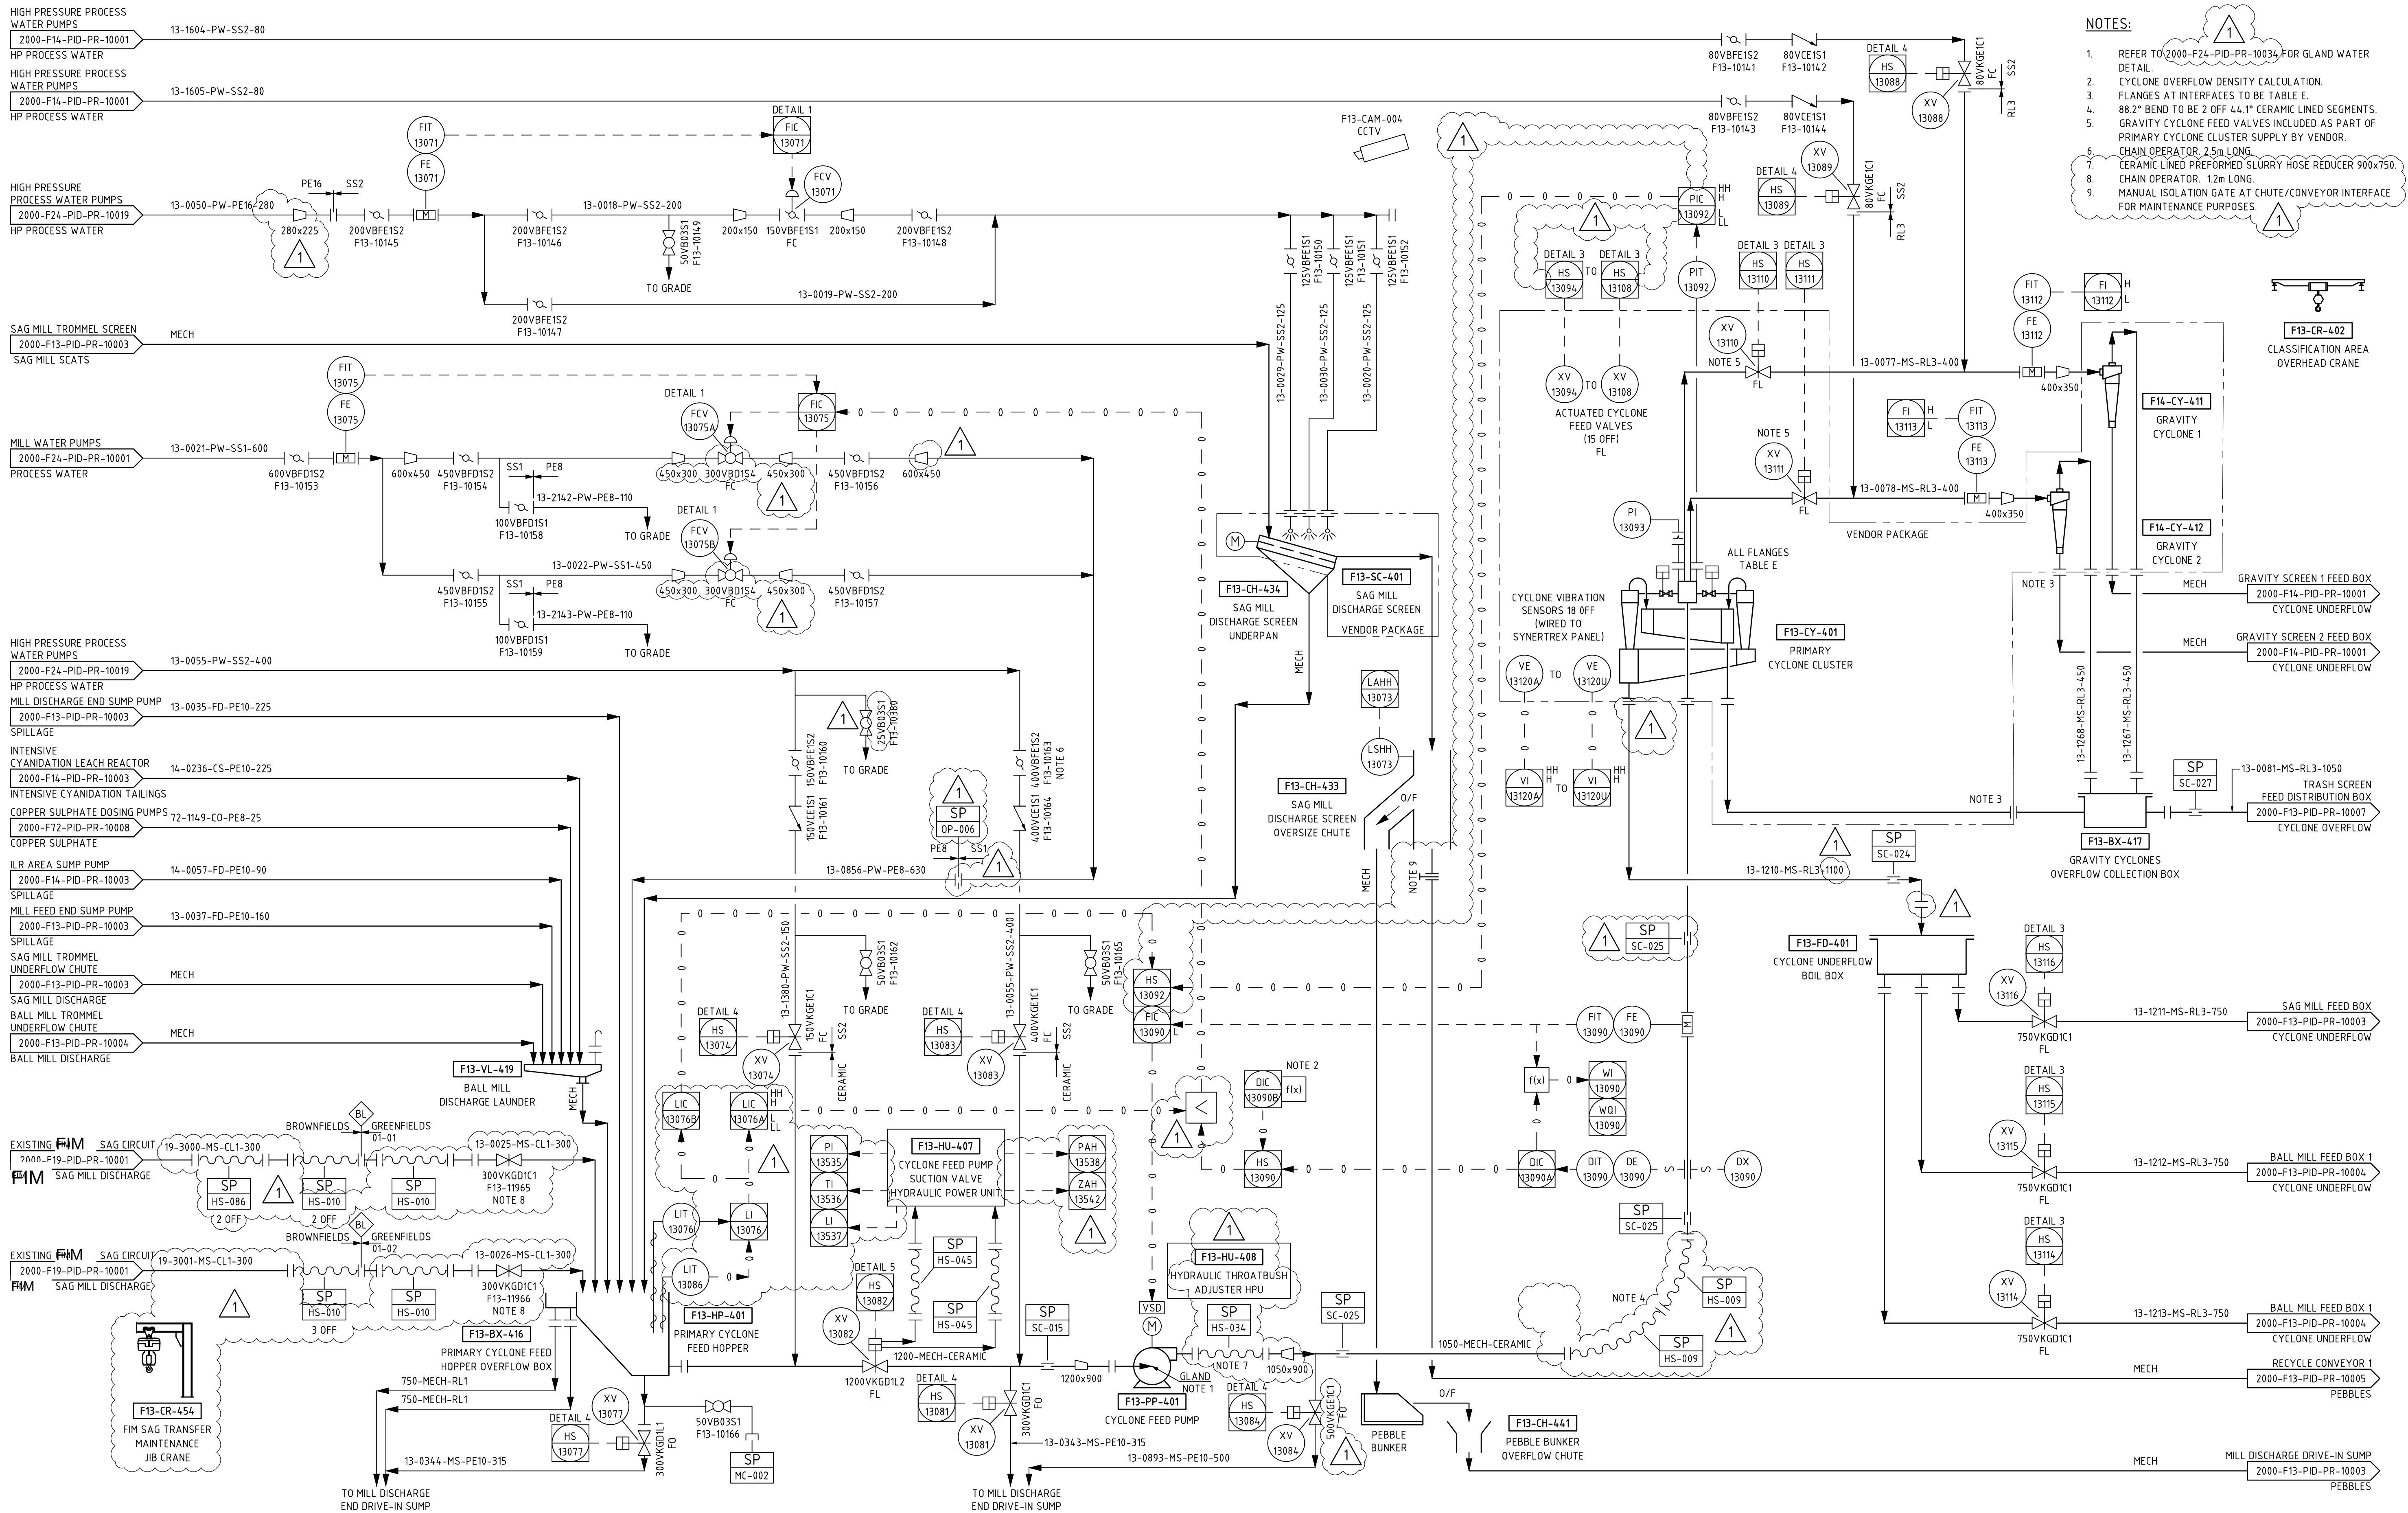

NOTES:

1. REFER TO 2000-F24-PID-PR-10003 FOR GLAND WATER DETAIL
2. CYCLONE OVERFLOW DENSITY CALCULATION
3. FLANGES AT INTERFACES TO BE TABLE E
4. 88.2" BEND TO BE 2 OFF 4.4" CERAMIC LINED SEGMENTS
5. GRAVITY CYCLONE FEED VALVES INCLUDED AS PART OF PRIMARY CYCLONE CLUSTER SUPPLY BY VENDOR
6. CHAIN OPERATOR, 2.5m LONG
7. CERAMIC LINED PREFORMED SLURRY HOSE REDUCER 900x750
8. CHAIN OPERATOR, 1.2m LONG
9. MANUAL ISOLATION GATE AT CHUTE/CONVEYOR INTERFACE FOR MAINTENANCE PURPOSES

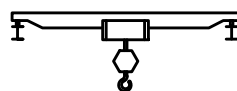

F13-CR-402
CLASSIFICATION AREA
OVERHEAD CRANE