


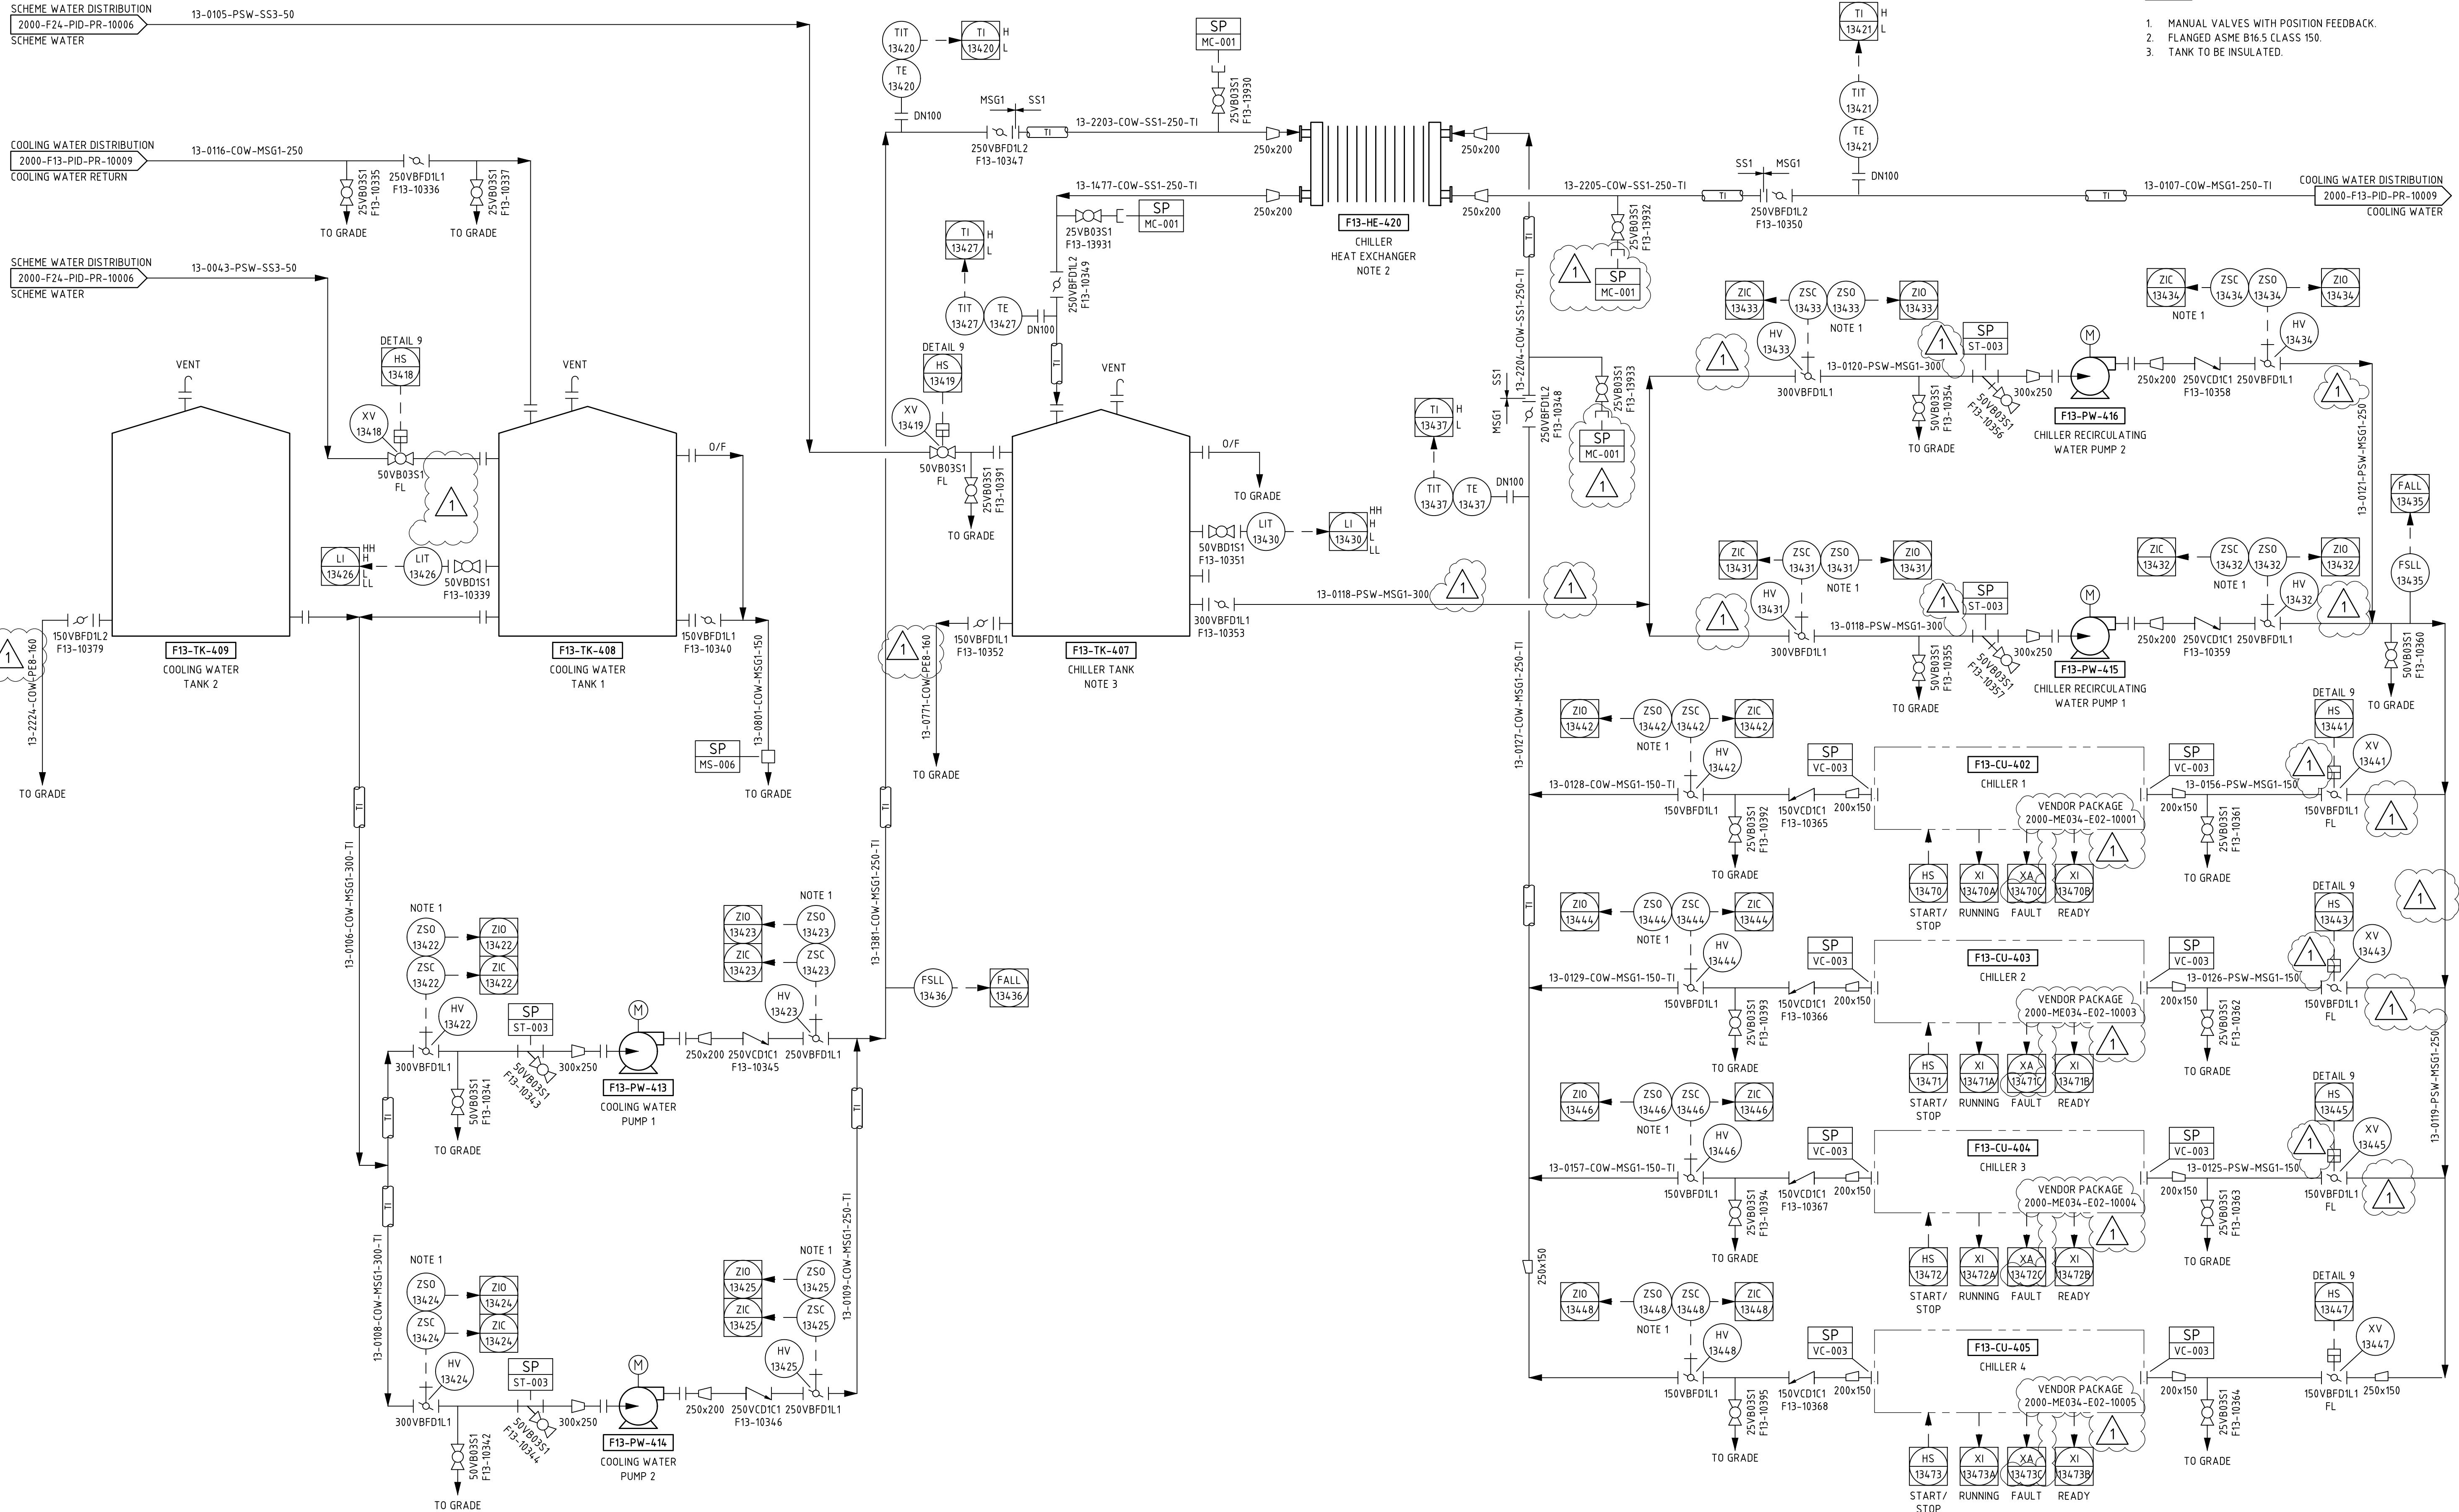

NOTES:

1. MANUAL VALVES WITH POSITION FEEDBACK.
2. FLANGED ASME B16.5 CLASS 150.
3. TANK TO BE INSULATED.