
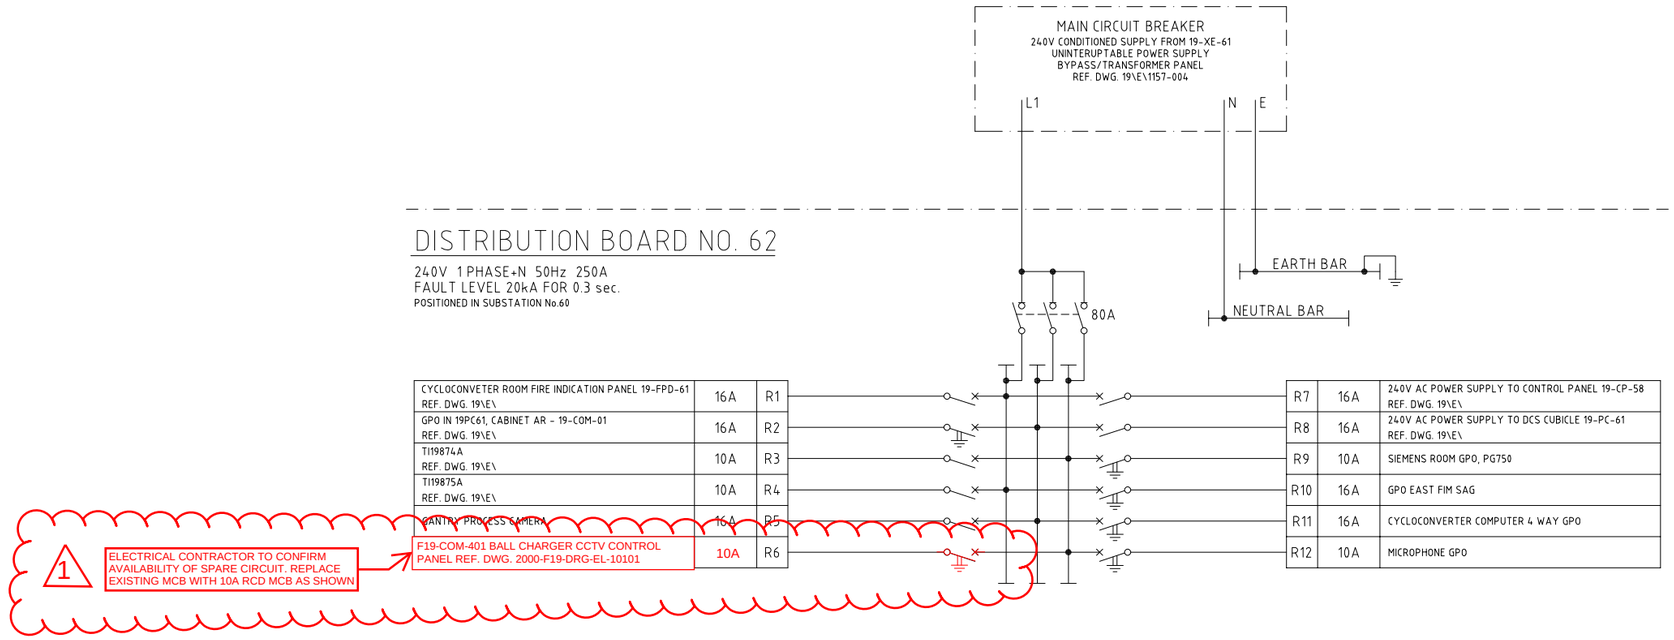


LEGEND

- CIRCUIT BREAKER
- ISOLATOR
- CIRCUIT BREAKER RCD 30mA

LOCATION

SUB STATION 60
19-DB-62

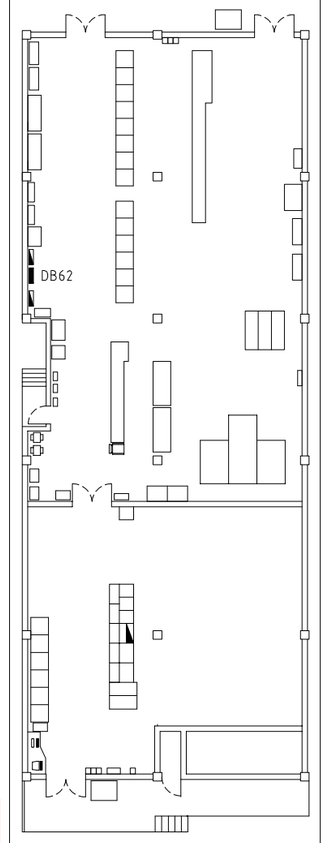

NOTES

PRIMERO
primero.com.au | DESIGN | CONSTRUCT | OPERATE

KCGM GROWTH PROJECT

DRAWING NO.
2000-F19-TLD-EL-10002

REV.: 1

DESIGN APPR.:

DATE: 09/11/23

2000-F19-TLD-EL-10002_Rev1
240V instrument disctribution board no. 62 power schematic