
F22-SR-001
415V CARBON TREATMENT & ELUTION SWITCHROOM

F22-SW-030
CARBON TREATMENT & ELUTION 415V MOTOR CONTROL CENTRE No.1

CONTINUED ON SHT 1
2000-F22-SLD-EL-10201

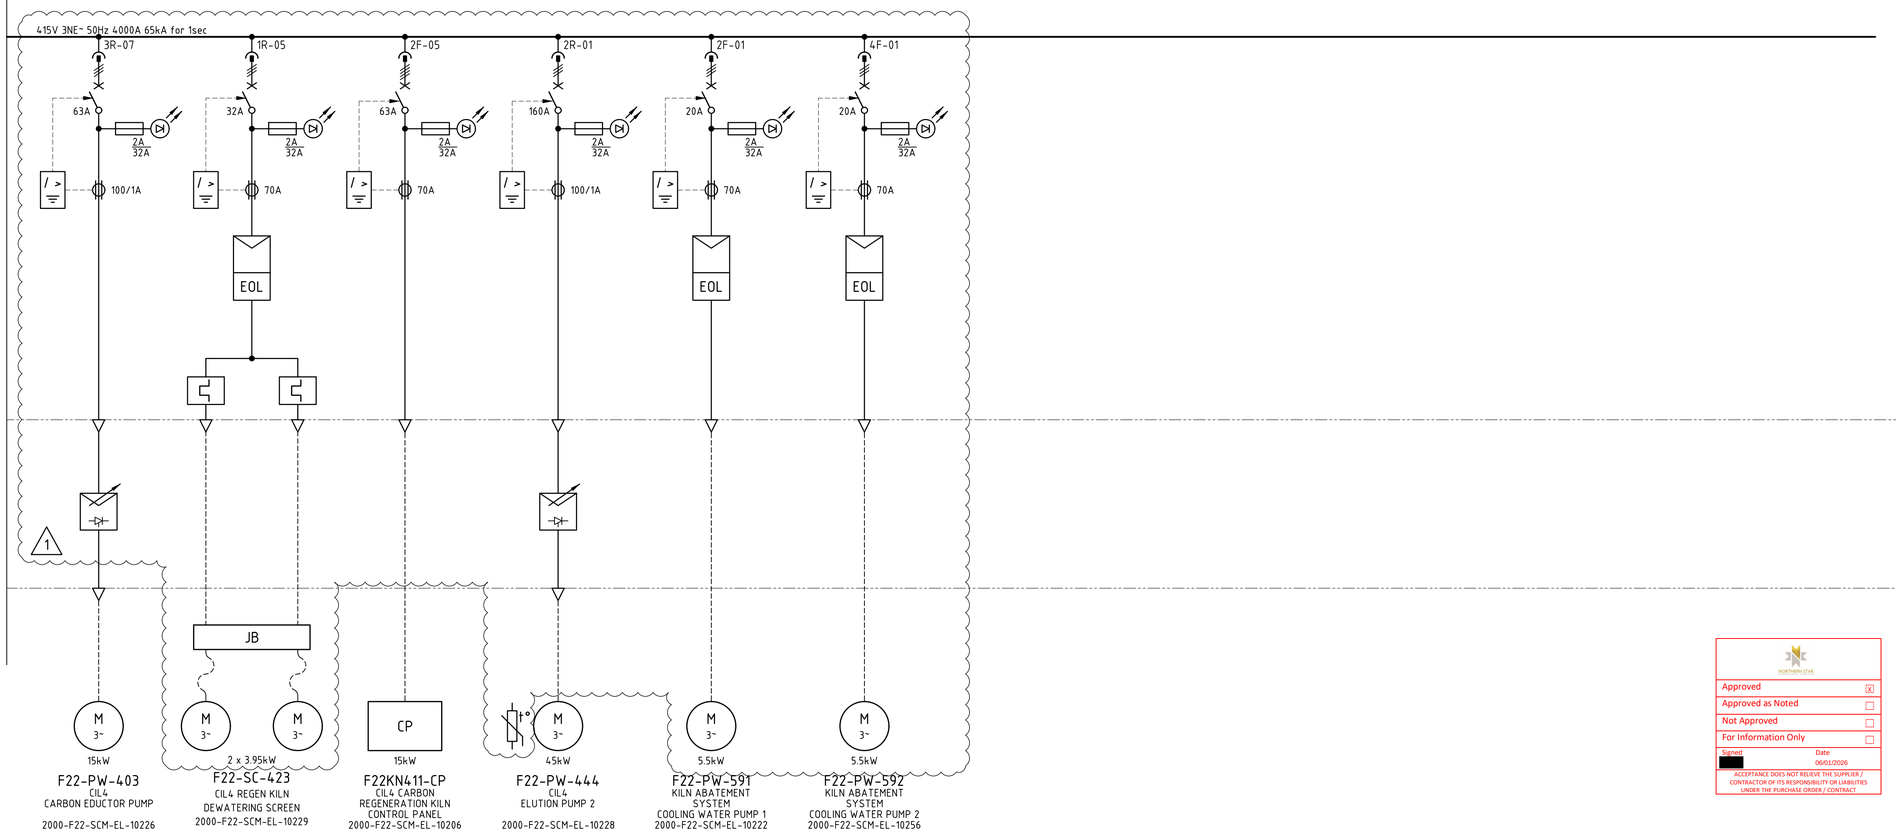

NOTES

1. REFER TO SHEET 1.

LEGEND

1. REFER TO SHEET 1.

Approved	X
Approved as Noted	
Not Approved	
For Information Only	

Signed [redacted] Date 06/01/2026

ACCEPTANCE DOES NOT RELIEVE THE SUPPLIER / CONTRACTOR OF ITS RESPONSIBILITY OR LIABILITIES UNDER THE PURCHASE ORDER / CONTRACT

2000-F22-SLD-EL-10202_Rev1

CIL4 carbon treatment & elution F22-SW-030 415V MCC single line diagram sheet 2

O:\CAD PROJECTS\235 NORTHERN STAR RESOURCES LTD\235I7 KCGM GROWTH PROJECT\03 DELIVERABLES\ELV\F22 - CIL4 CARBON TREAMENT & ELUTION\2000-F22-SLD-EL-10202.DWG 18DEC25 12:14PM HOTSEAT04