
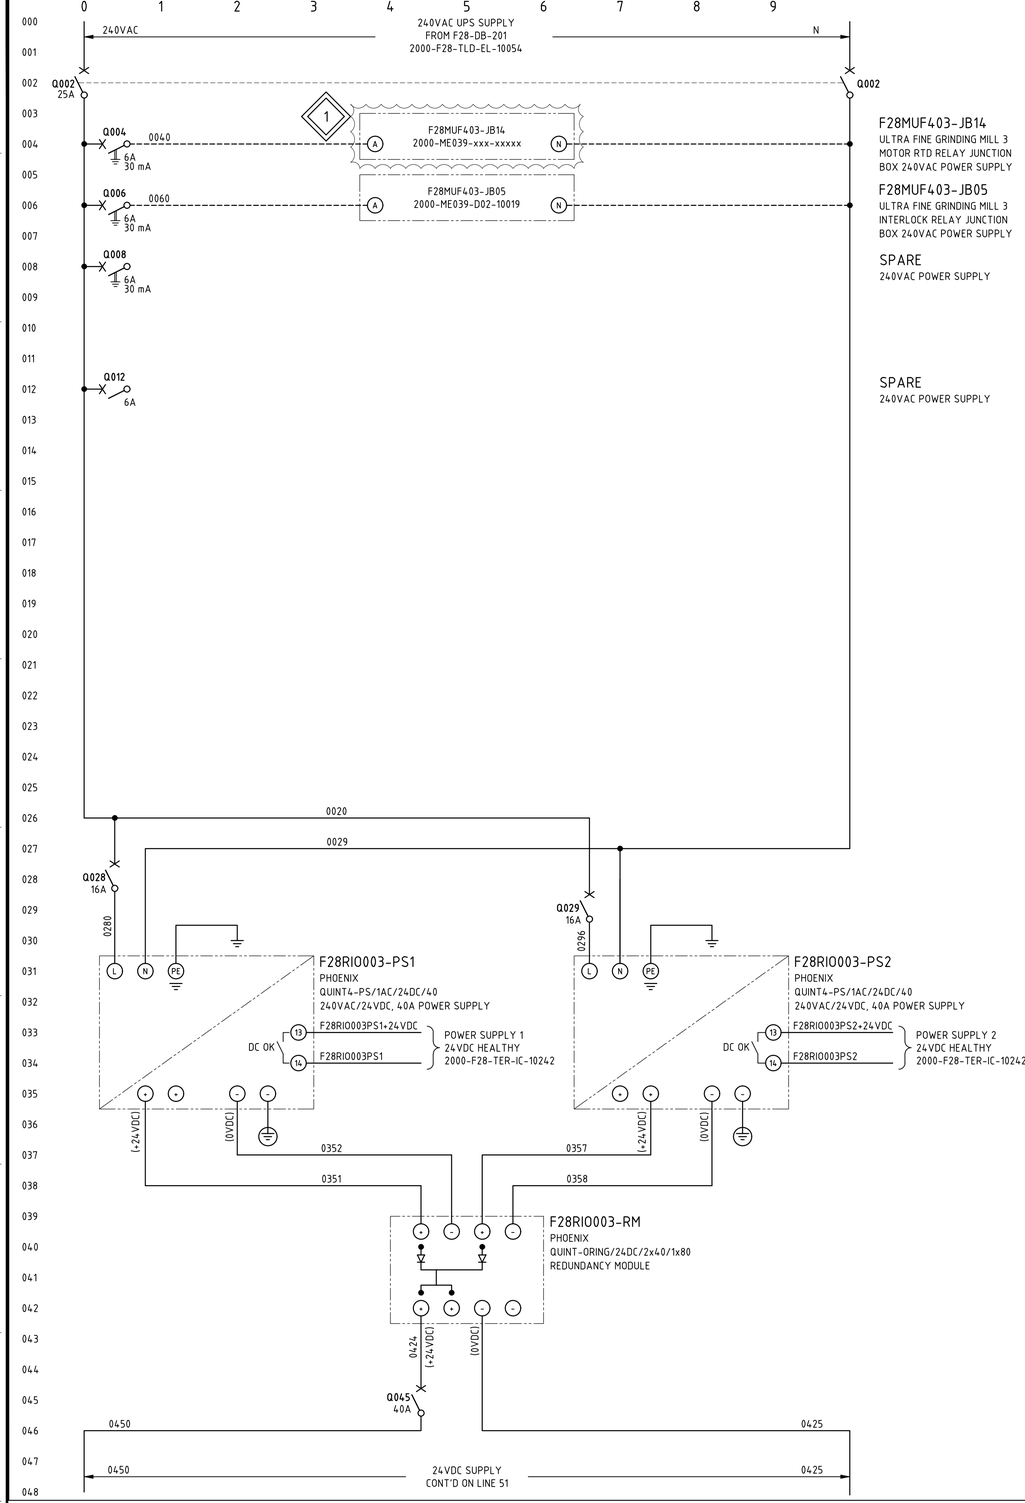


F28MUF403-JB14
ULTRA FINE GRINDING MILL 3
MOTOR RTD RELAY JUNCTION
BOX 240VAC POWER SUPPLY

F28MUF403-JB05
ULTRA FINE GRINDING MILL 3
INTERLOCK RELAY JUNCTION
BOX 240VAC POWER SUPPLY

SPARE
240VAC POWER SUPPLY

SPARE
240VAC POWER SUPPLY

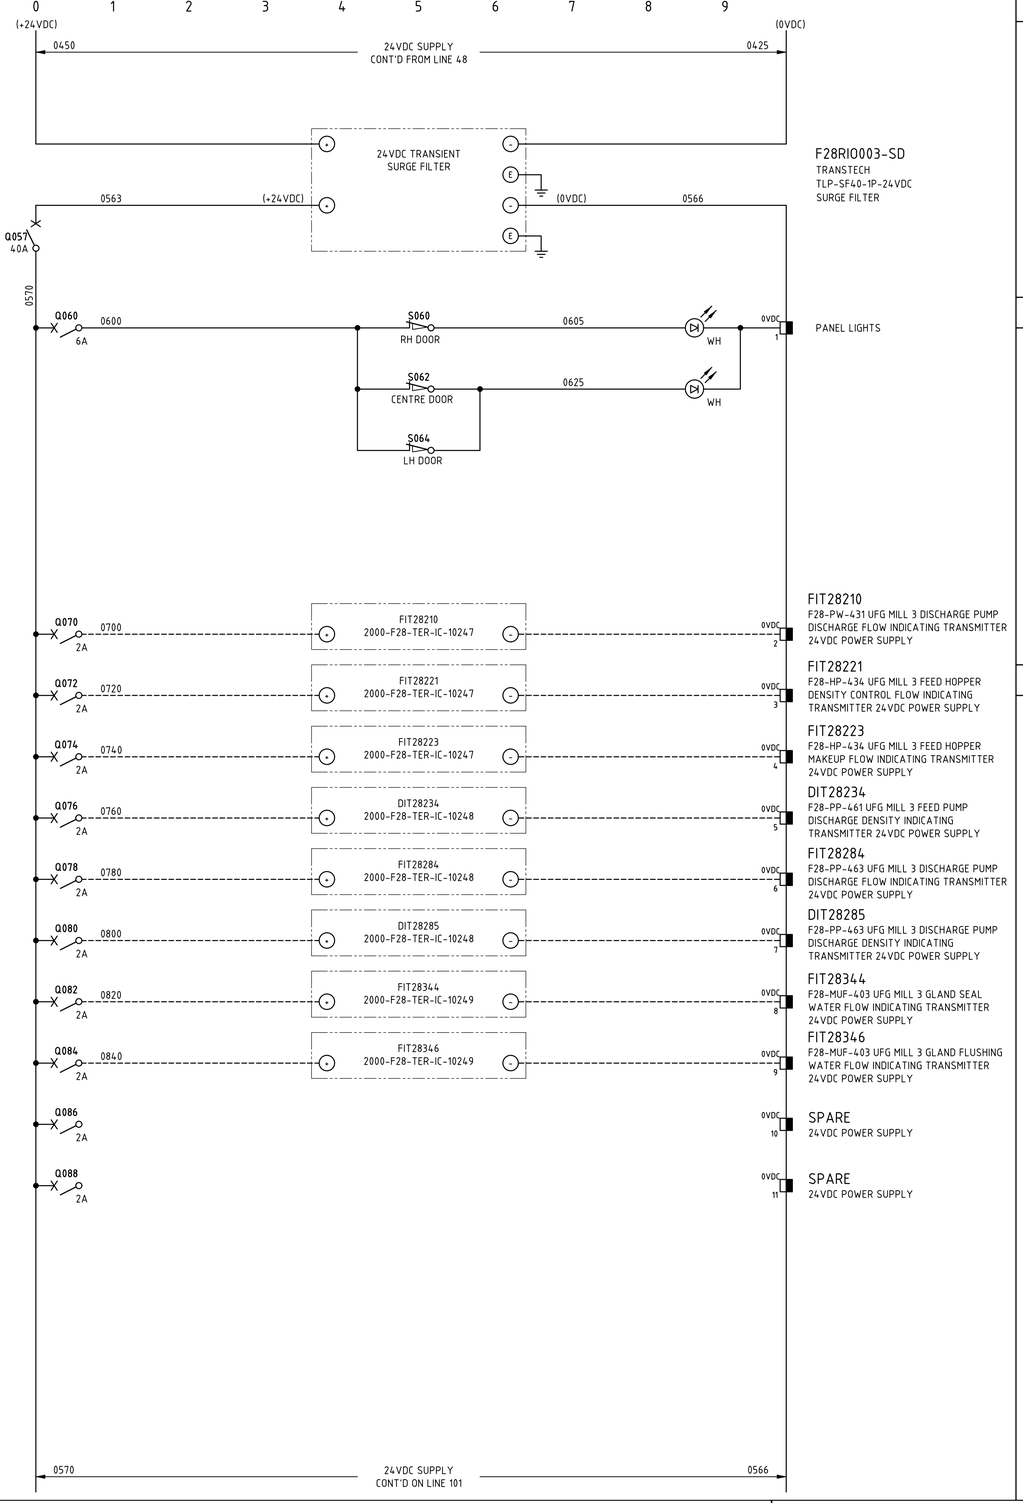

F28RIO003-SD
TRANSTECH
TLP-SF40-1P-24VDC
SURGE FILTER

PANEL LIGHTS

FIT28210
F28-PW-431 UFG MILL 3 DISCHARGE PUMP
DISCHARGE FLOW INDICATING TRANSMITTER
24VDC POWER SUPPLY

FIT28221
F28-HP-434 UFG MILL 3 FEED HOPPER
DENSITY CONTROL FLOW INDICATING
TRANSMITTER 24VDC POWER SUPPLY

FIT28223
F28-HP-434 UFG MILL 3 FEED HOPPER
MAKEUP FLOW INDICATING TRANSMITTER
24VDC POWER SUPPLY

DIT28234
F28-PP-461 UFG MILL 3 FEED PUMP
DISCHARGE DENSITY INDICATING
TRANSMITTER 24VDC POWER SUPPLY

FIT28284
F28-PP-463 UFG MILL 3 DISCHARGE PUMP
DISCHARGE FLOW INDICATING TRANSMITTER
24VDC POWER SUPPLY

DIT28285
F28-PP-463 UFG MILL 3 DISCHARGE PUMP
DISCHARGE DENSITY INDICATING
TRANSMITTER 24VDC POWER SUPPLY

FIT28344
F28-MUF-403 UFG MILL 3 GLAND SEAL
WATER FLOW INDICATING TRANSMITTER
24VDC POWER SUPPLY

FIT28346
F28-MUF-403 UFG MILL 3 GLAND FLUSHING
WATER FLOW INDICATING TRANSMITTER
24VDC POWER SUPPLY

SPARE
24VDC POWER SUPPLY

SPARE
24VDC POWER SUPPLY

NOTES

1. TERMINALS ON TERMINAL STRIPS ABOVE 50VAC SHALL HAVE A SEPARATE PERSPEX SHROUD AND SHALL BE LABELLED "DANGER xxxVAC".
2. WIRE NUMBER FERRULES ON TERMINAL STRIP SHALL BE PREFIXED WITH EQUIPMENT NUMBER e.g. F28RIO003-xxxx.
3. EACH WIRE SHALL BE IDENTIFIED AT BOTH ENDS WITH FERRULES.
4. FOR NETWORK CONNECTION & BUS CABLING DETAILS REFER TO RIO PANEL COMMUNICATIONS TERMINATION DIAGRAMS.
5. INSTRUMENT EARTH BAR TO BE BONDED TO MAIN EARTH BAR WITH SOLID COPPER LINK.

LEGEND

- FIELD TERMINAL
- DCS OR I/O TERMINAL
- 0VDC TERMINAL FOR 24VDC
- 0VDC TERMINAL FOR 54VDC
- DEVICE TERMINAL
- INDICATION LAMP, cc = COLOUR
- EARTH BAR
- INSTRUMENT EARTH BAR

HOLD

1. AWAITING VENDOR INFORMATION.

2000-F28-SCM-IC-10241_Rev0

F28-RIO-003 ultra fine grinding field n-IO panel
-schematic diagram sheet 1

O:\CAD PROJECTS\235 NORTHERN STAR RESOURCES LTD\23517 KCGM GROWTH PROJECT\03 DELIVERABLES\IC\F28 - ULTRAFINE GRINDING 2 & 3\2000-F28-SCM-IC-10241.DWG 14MAR25 6:20AM SANDRA CULL