
SUBSTATION No. 68
CARBON IN LEACH (C.I.L. 3)

F30-SW-401
CIL 3 415V MOTOR CONTROL CENTRE

CONTINUED ON SHT 1.
2000-F30-SLD-EL-10301

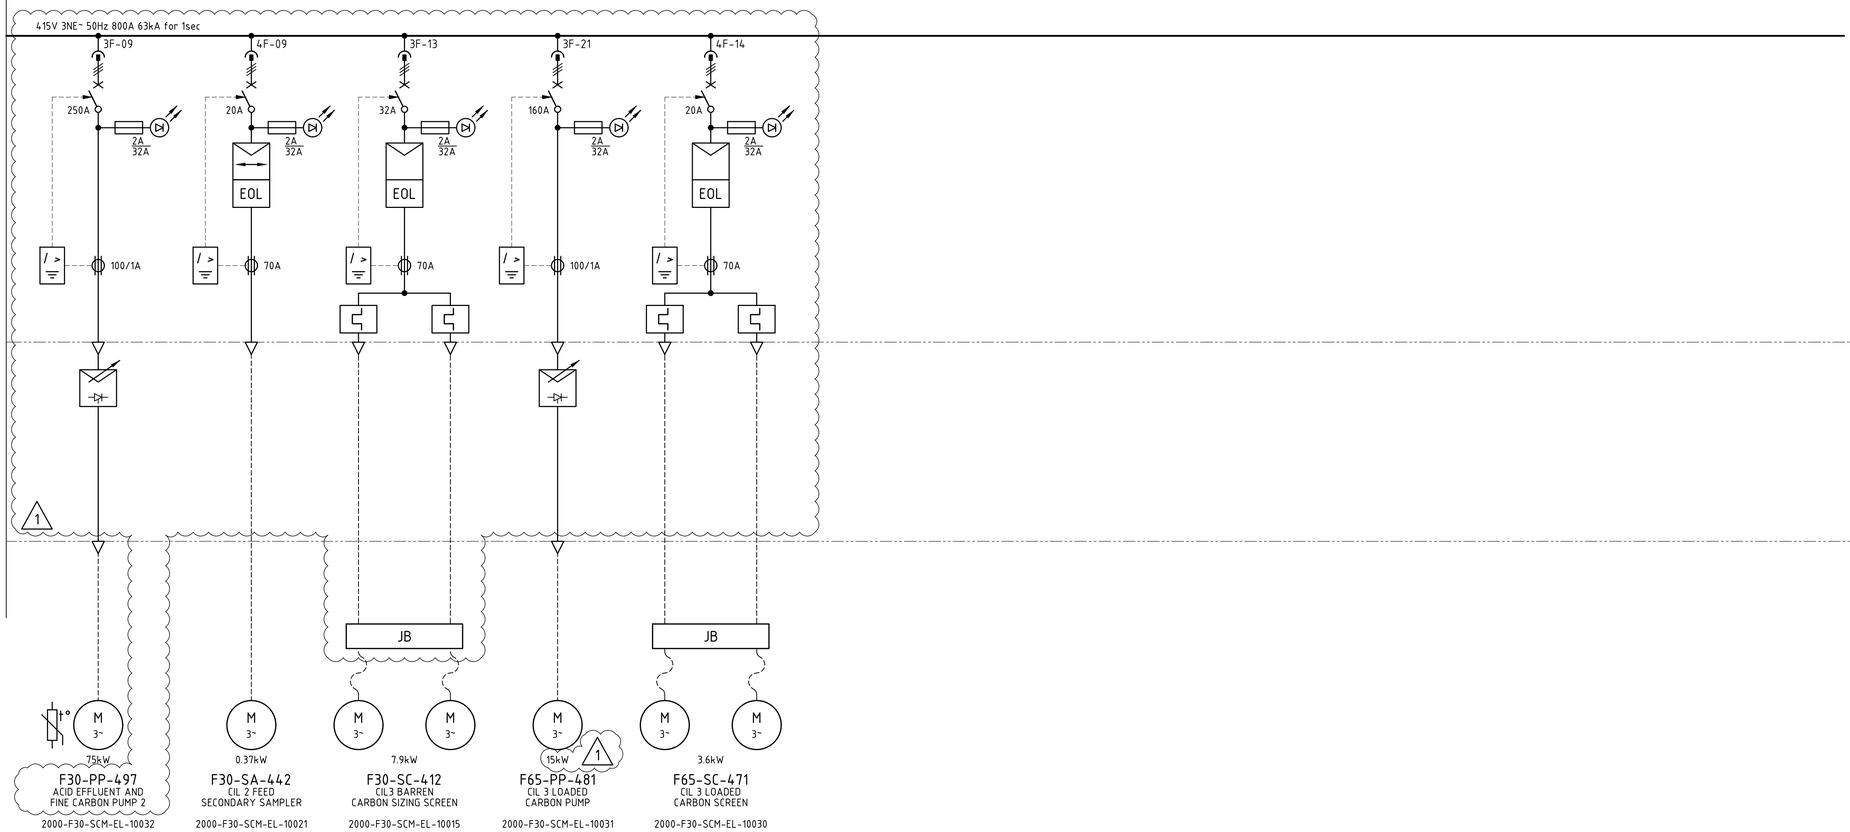

NOTES

1. REFER TO SHEET 1.

LEGEND

1. REFER TO SHEET 1.

Approved	☒
Approved as Noted	☐
Not Approved	☐
For Information Only	☐

Signed [redacted] Date 05/12/2025

ACCEPTANCE DOES NOT RELIEVE THE SUPPLIER / CONTRACTOR OF ITS RESPONSIBILITY OR LIABILITIES UNDER THE PURCHASE ORDER / CONTRACT

2000-F30-SLD-EL-10302_Rev1

Carbon in leach (CIL3) substation no. 68 MCC
F30-SW-401 single line diagram sheet 2

O:\CAD PROJECTS\235 NORTHERN STAR RESOURCES LTD\23517 KCGM GROWTH PROJECT\03 DELIVERABLES\ELV\F30 - CIL2_3 & CONCENTRATE THICKENING\2000-F30-SLD-EL-10302.DWG 19NOV25 11:45AM HOTSEAT04