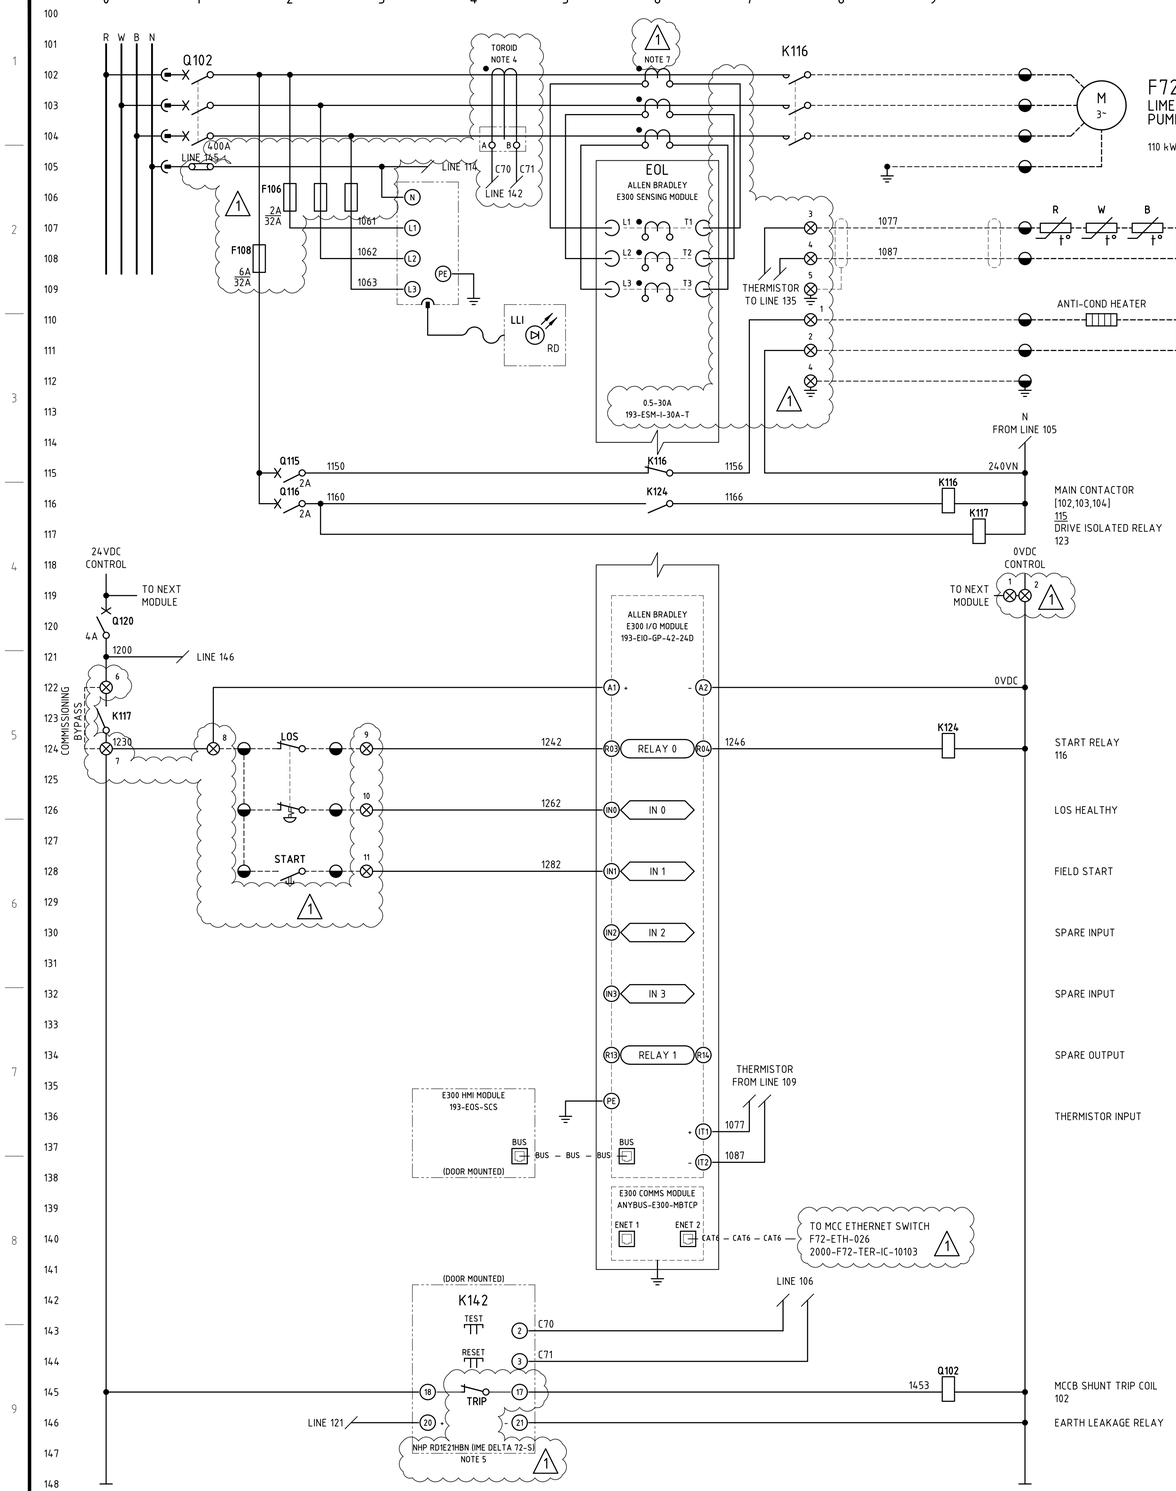


240VAC TERMINALS

1		F72PP657-1156
2		F72PP657-240VN
3		
4	⏚	EARTH

NOTES 2, 6

RD
BK
GNYE

F72PP657-P3
2.5 mm² 2C+E

F72PP657 MOTOR TERMINAL BOX
ANTI-COND HEATER

24VDC LOOPED POWER
NEXT MODULE
PREV MODULE

CABLE ZONE
24VDC TERMINALS

Q120	4A		F72SW172-2570
1			F72SW172-2580
2			F72SW172-2580
3			F72PP657-1077
4			F72PP657-1087
5	⏚		SCREEN
6			F72PP657-1200
7			F72PP657-1230
8			F72PP657-1230
9			F72PP657-1242
10			F72PP657-1262
11			F72PP657-1282
12			
13			
14			
15			
16			
17	⏚		EARTH

NOTE 2

WH
BK
GNYE

COMMISSIONING BYPASS

F72PP657-I1
1.5 mm² 1 Pair O/S

THERMISTORS

F72PP657-LCS
LOCAL CONTROL STATION

F72PP657LCS-C1
1.5 mm² 4C+E

LOS
START

NOTES

1. TERMINALS ON TERMINAL STRIPS ABOVE 50VAC SHALL HAVE A SEPARATE PERSPEX SHROUD AND SHALL BE LABELLED "DANGER xxxVAC".
2. WIRE NUMBER FERRULES ON TERMINAL STRIP SHALL BE PREFIXED WITH EQUIPMENT NUMBER e.g. F72PP657-1200, UNLESS OTHERWISE NOTED. (1)
3. EACH WIRE SHALL BE IDENTIFIED AT BOTH ENDS WITH FERRULES.
4. NHP TDGE2 IN:250A IΔN MIN:0.3A TOROID TO SUIT CABLE DIAMETER. (1)
5. EARTH LEAKAGE RELAY (ELV) USER INTERFACE TO BE MOUNTED ON MCC MODULE DOOR. RELAY ENERGISED (NORMALLY CLOSED CONTACT OPEN) IN NORMAL OPERATION.
6. 240VAC TERMINALS FOR THE HEATER CIRCUITS SHALL BE LOCATED IN THE MCC DRIVE MODULE.
7. EXTERNAL CURRENT TRANSFORMER RATIO (1)
   RED PHASE: 400/5A
   WHITE PHASE: 400/5A
   BLUE PHASE: 400/5A

LEGEND

- 00/01/00 — DCS DIGITAL INPUT
- 00/02/00 — DCS DIGITAL OUTPUT
- ⊗ — MCC TERMINAL
- ◓ — VSD TERMINAL
- ◒ — FIELD TERMINAL
- ◑ — DCS OR I/O TERMINAL
- ◧ — MARSHALLING TERMINAL
- (x) — DEVICE TERMINAL
- ⊗ cc — INDICATION LAMP, cc = COLOUR

(1)

TERMINATION LEGEND

Q120	4A		F72SW172-2xxx
1			F72SW172-2xxx
2			F72SW172-2xxx
3			F72PP657-1200
4			F72PP657-1230
5			F72PP657-1230
6	⏚		EARTH

RD
BK
GNYE

CORE COLOUR/ IDENTIFIER
BARRIER
FERRULE
JUMPER/DISCONNECT/ FUSE/EARTH
TERMINAL No.
DESTINATION

2000-F72-SCM-EL-10658_Rev1

F72-SW-172 F72-PP-657 lime ringmain pump 2 schematic and termination diagram

O:\CAD PROJECTS\235 NORTHERN STAR RESOURCES LTD\235171 KCGM GROWTH PROJECT\03 DELIVERABLES\EL\F72 - REAGENTS MIXING & STORAGE\2000-F72-SCM-EL-10658.DWG 02DEC25 12:40PM HOTSEAT04