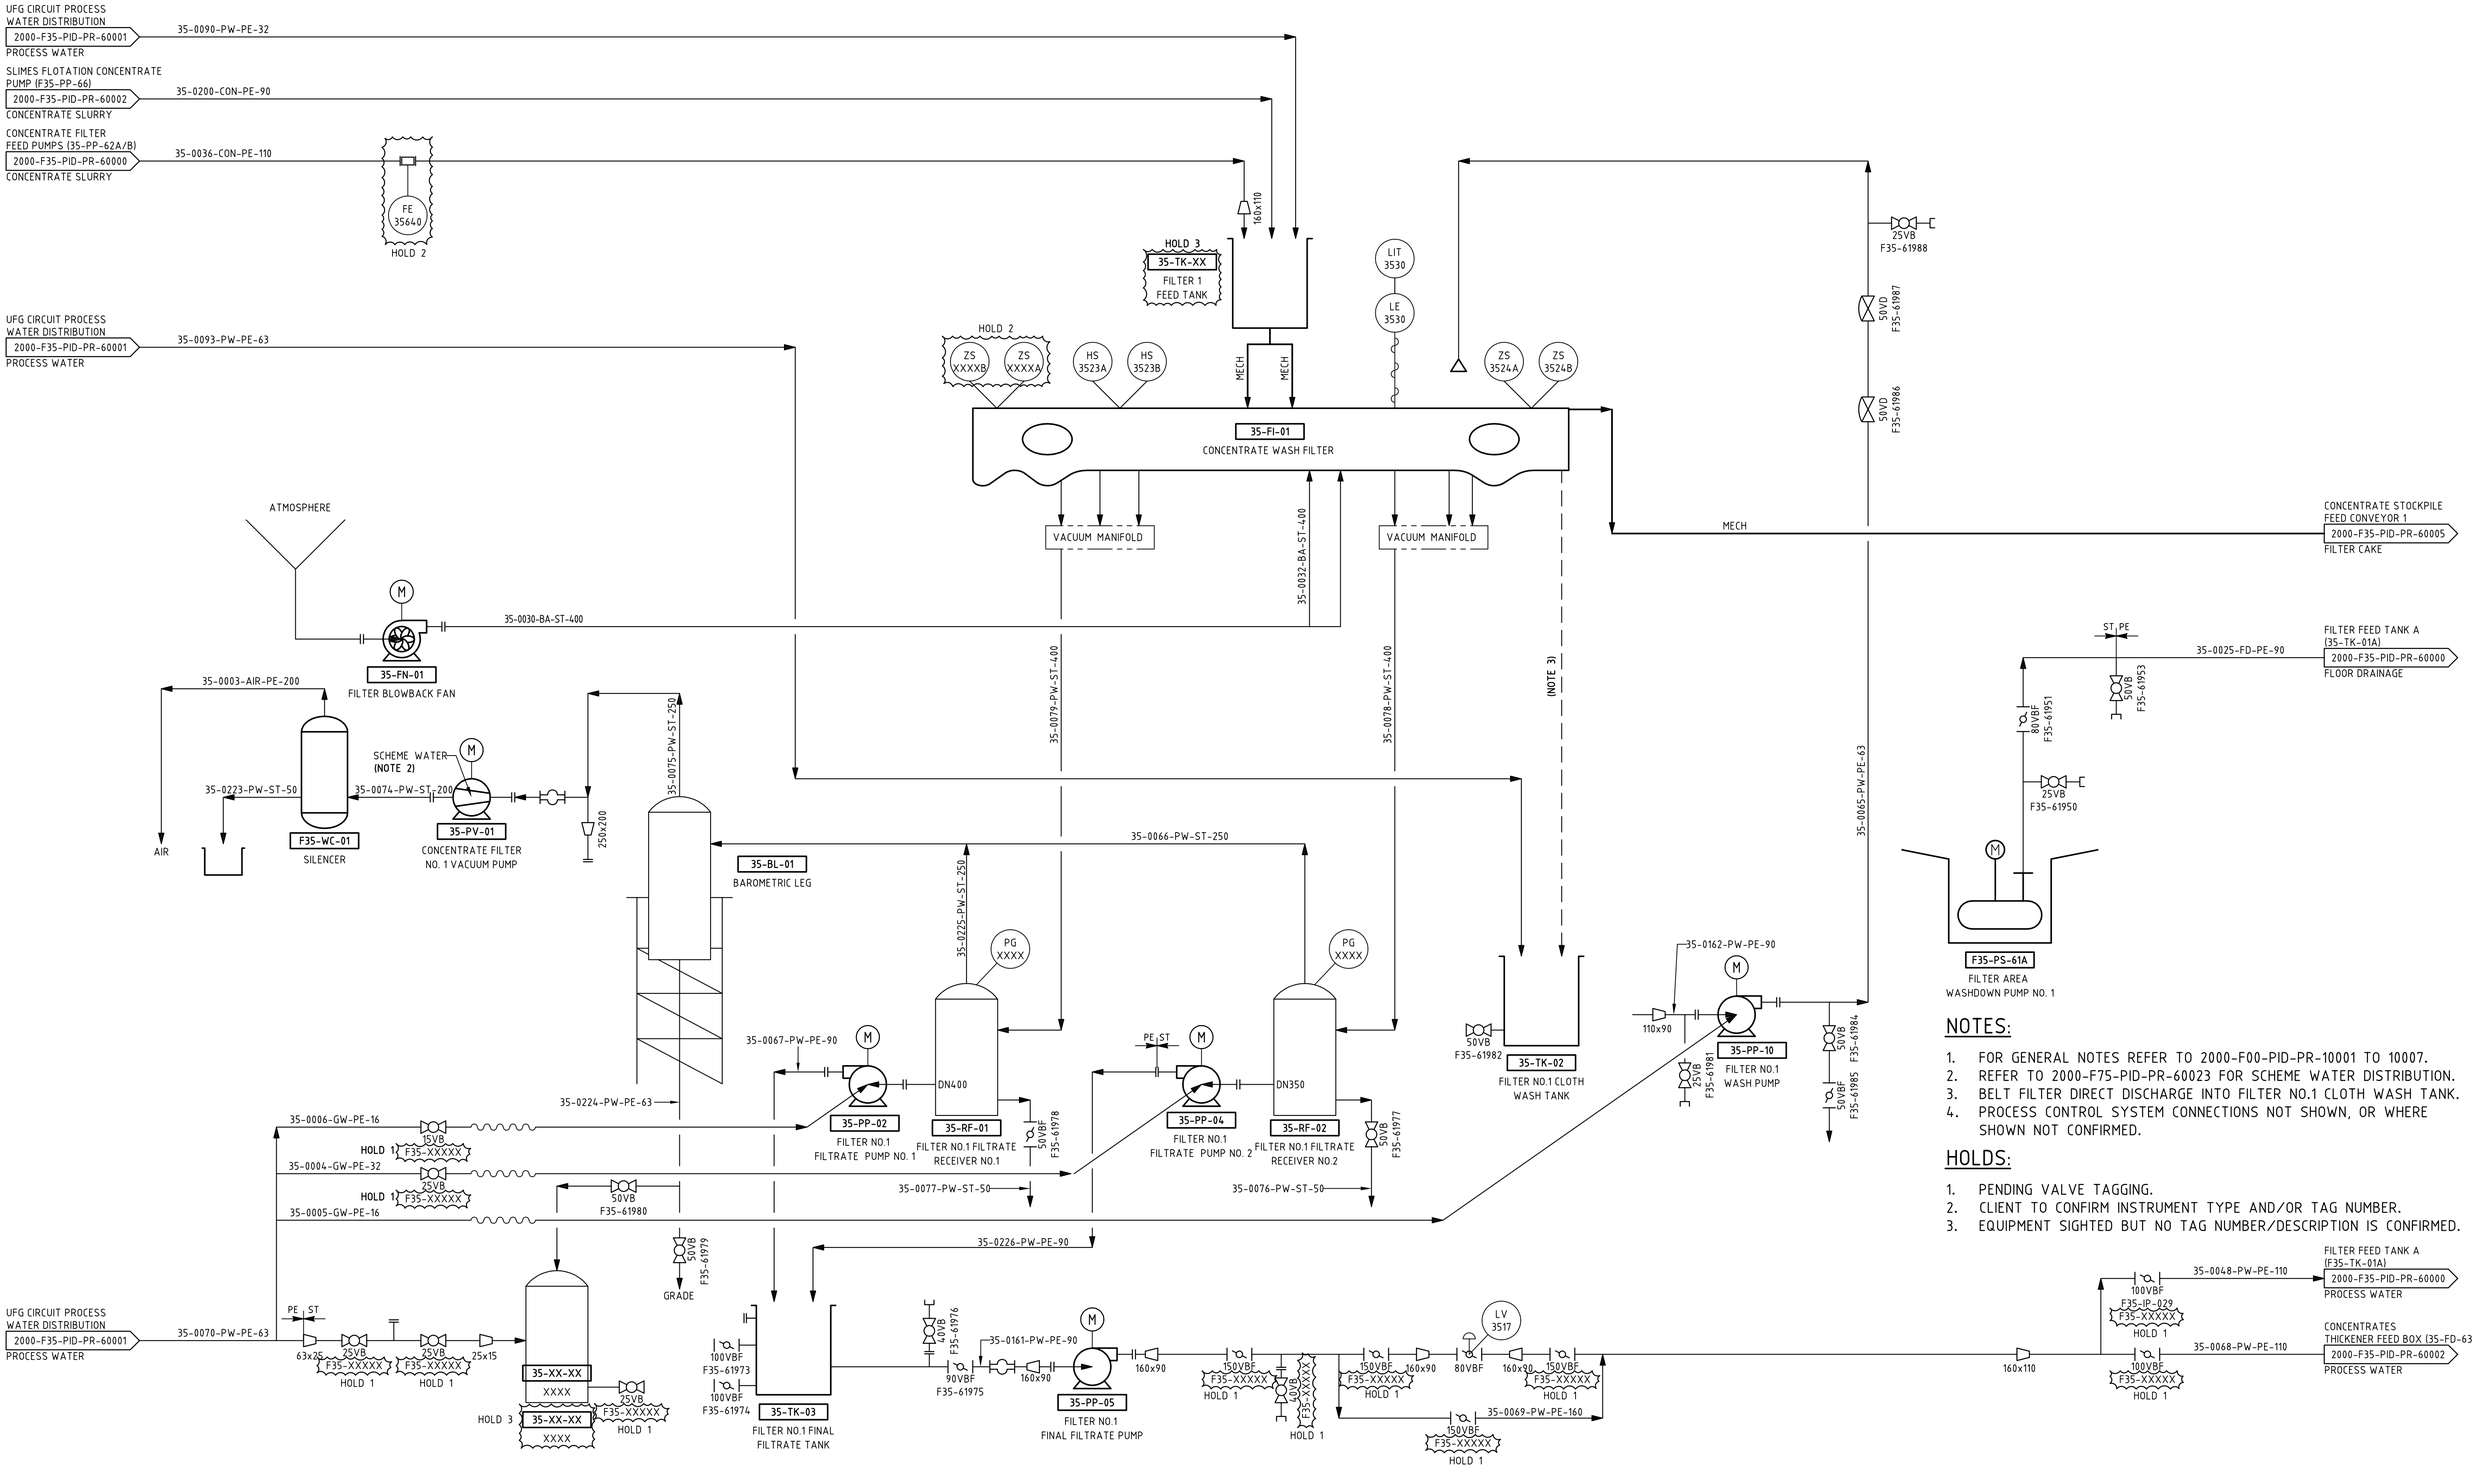


NOTES:

1. FOR GENERAL NOTES REFER TO 2000-F00-PID-PR-10001 TO 10007.
2. REFER TO 2000-F75-PID-PR-60023 FOR SCHEME WATER DISTRIBUTION.
3. BELT FILTER DIRECT DISCHARGE INTO FILTER NO.1 CLOTH WASH TANK.
4. PROCESS CONTROL SYSTEM CONNECTIONS NOT SHOWN, OR WHERE SHOWN NOT CONFIRMED.

HOLDS:

1. PENDING VALVE TAGGING.
2. CLIENT TO CONFIRM INSTRUMENT TYPE AND/OR TAG NUMBER.
3. EQUIPMENT SIGHTED BUT NO TAG NUMBER/DESCRIPTION IS CONFIRMED.

ORIGINAL DRAWING: FME-35-PI-445