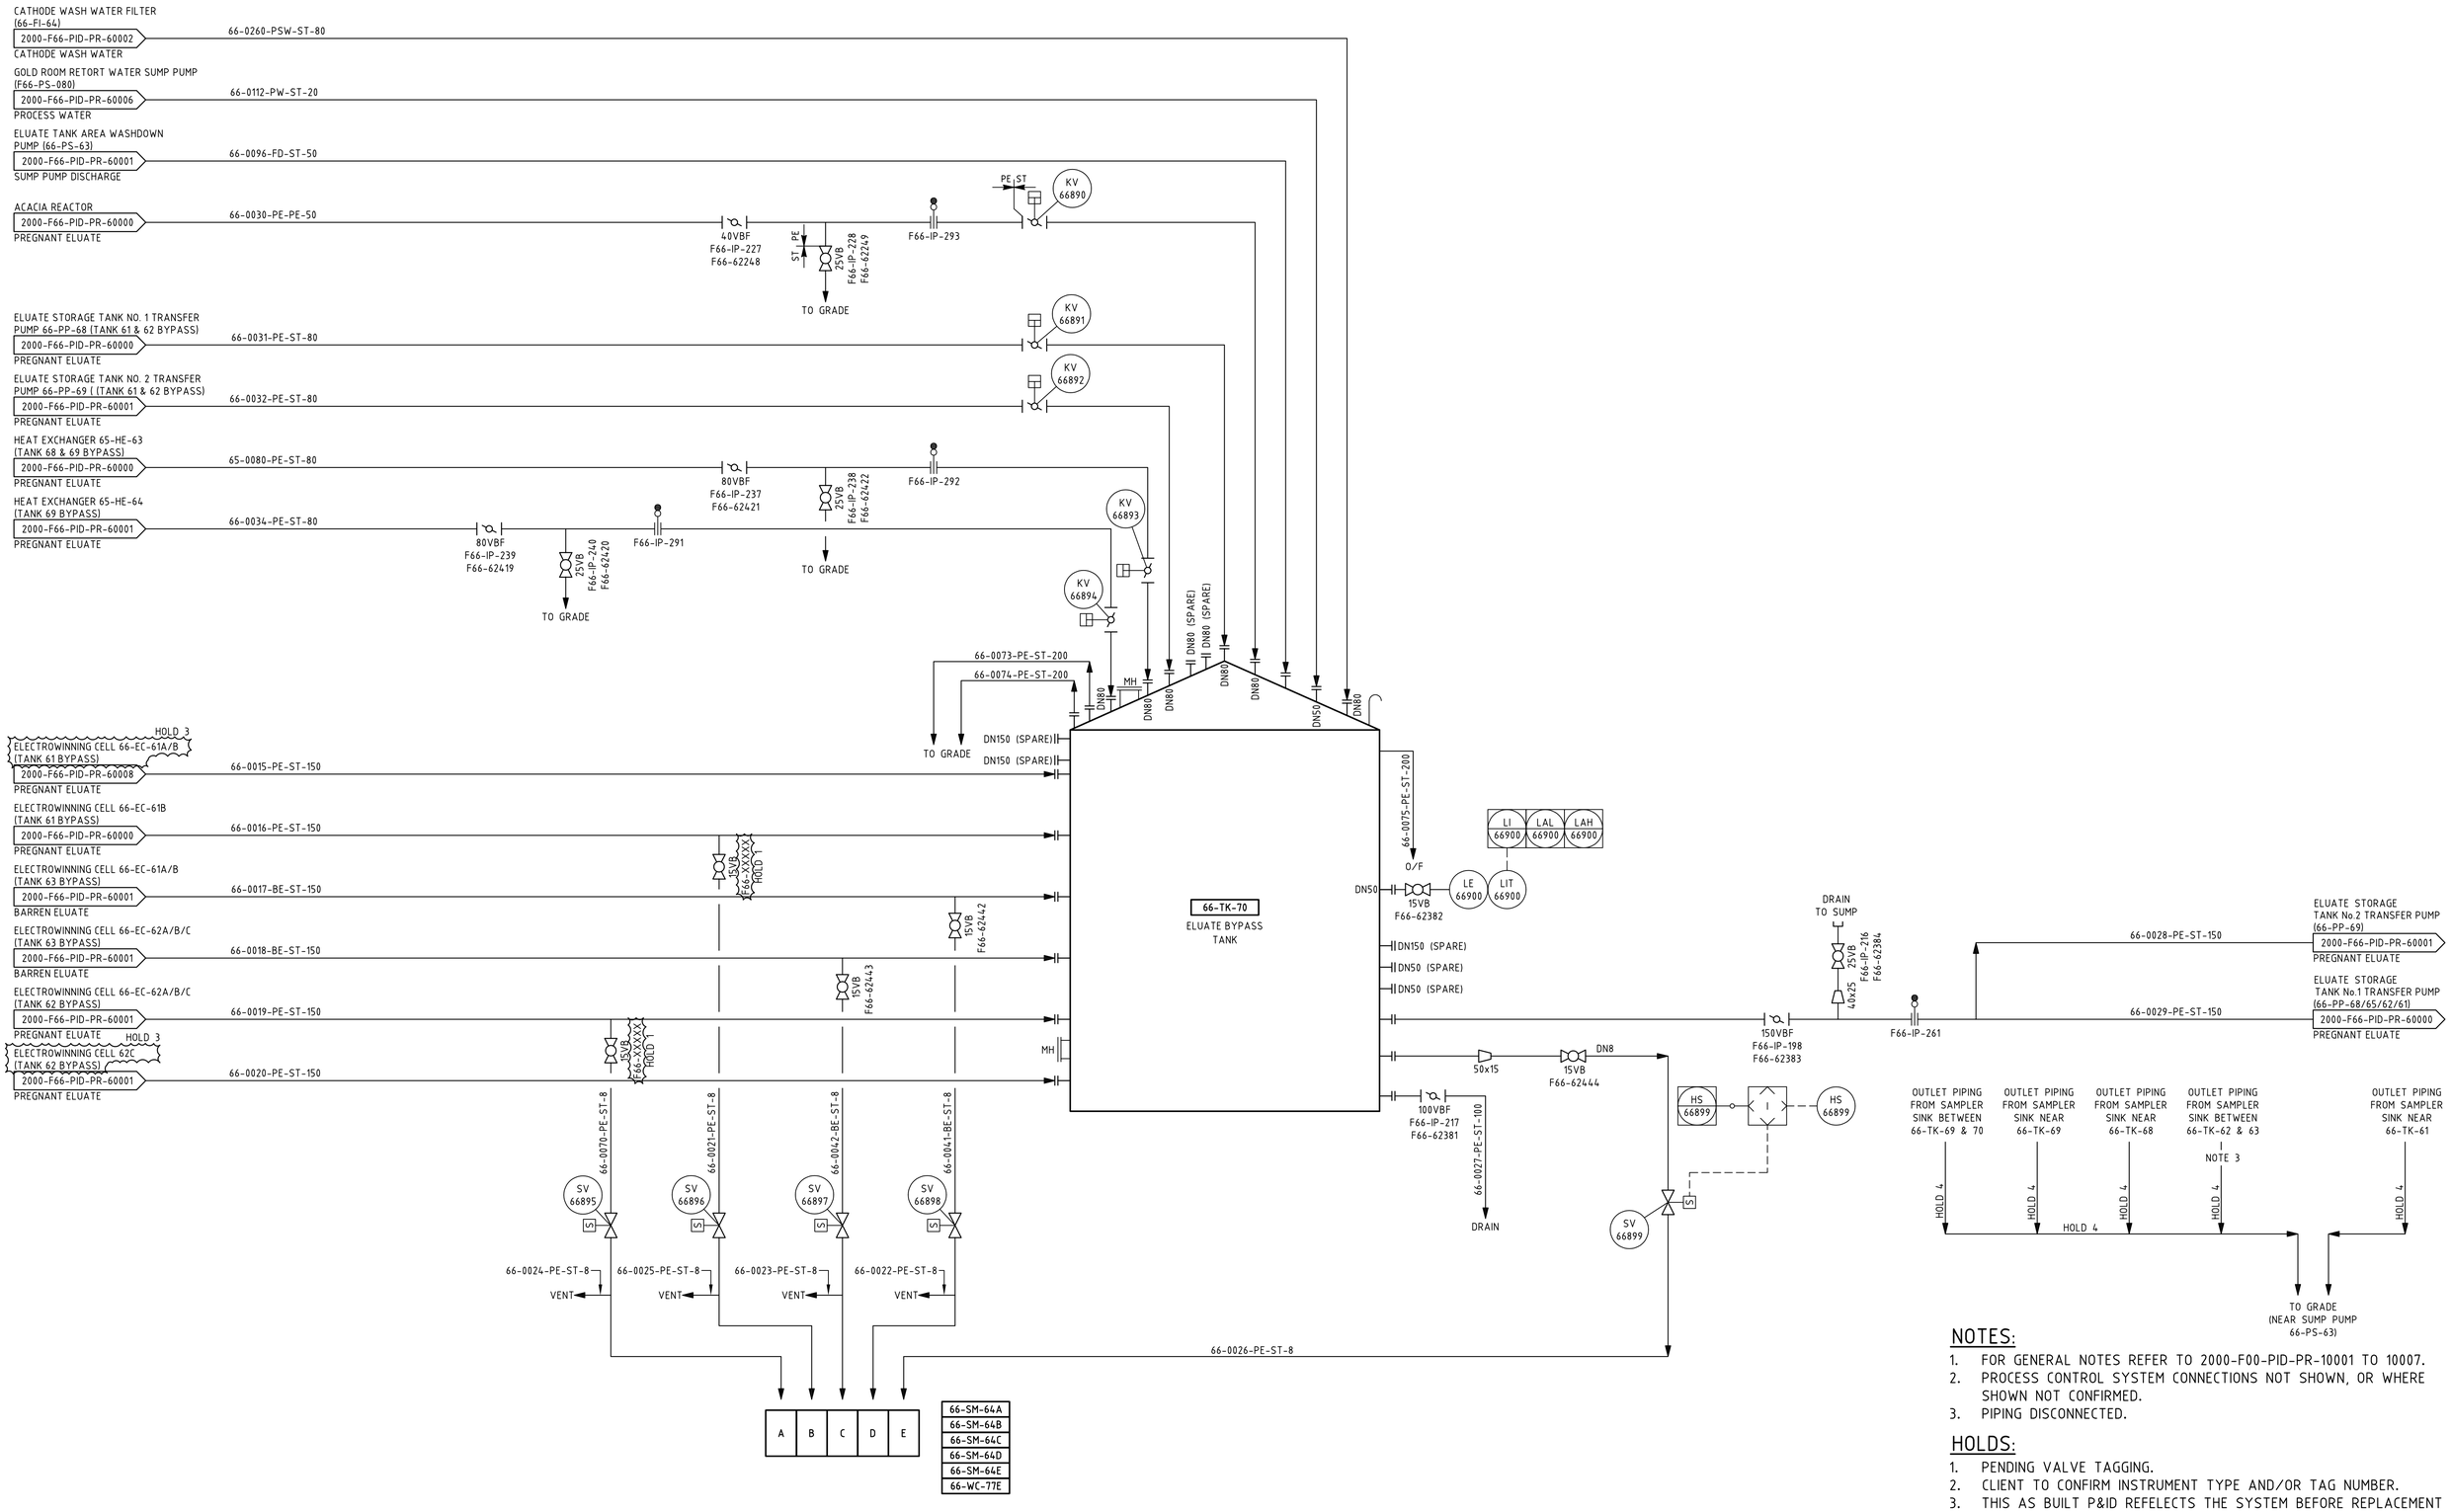


NOTES:

1. FOR GENERAL NOTES REFER TO 2000-F00-PID-PR-10001 TO 10007.
2. PROCESS CONTROL SYSTEM CONNECTIONS NOT SHOWN, OR WHERE SHOWN NOT CONFIRMED.
3. PIPING DISCONNECTED.

HOLDS:

1. PENDING VALVE TAGGING.
2. CLIENT TO CONFIRM INSTRUMENT TYPE AND/OR TAG NUMBER.
3. THIS AS BUILT P&ID REFELECTS THE SYSTEM BEFORE REPLACEMENT OF OLD ELECTROWINNING CELL WITH THE NEW ONE.
4. OD57 WHITE COLOR PIPING - MATERIAL (TBC BY CLIENT).

ORIGINAL DRAWING: FME-66-PI-1002