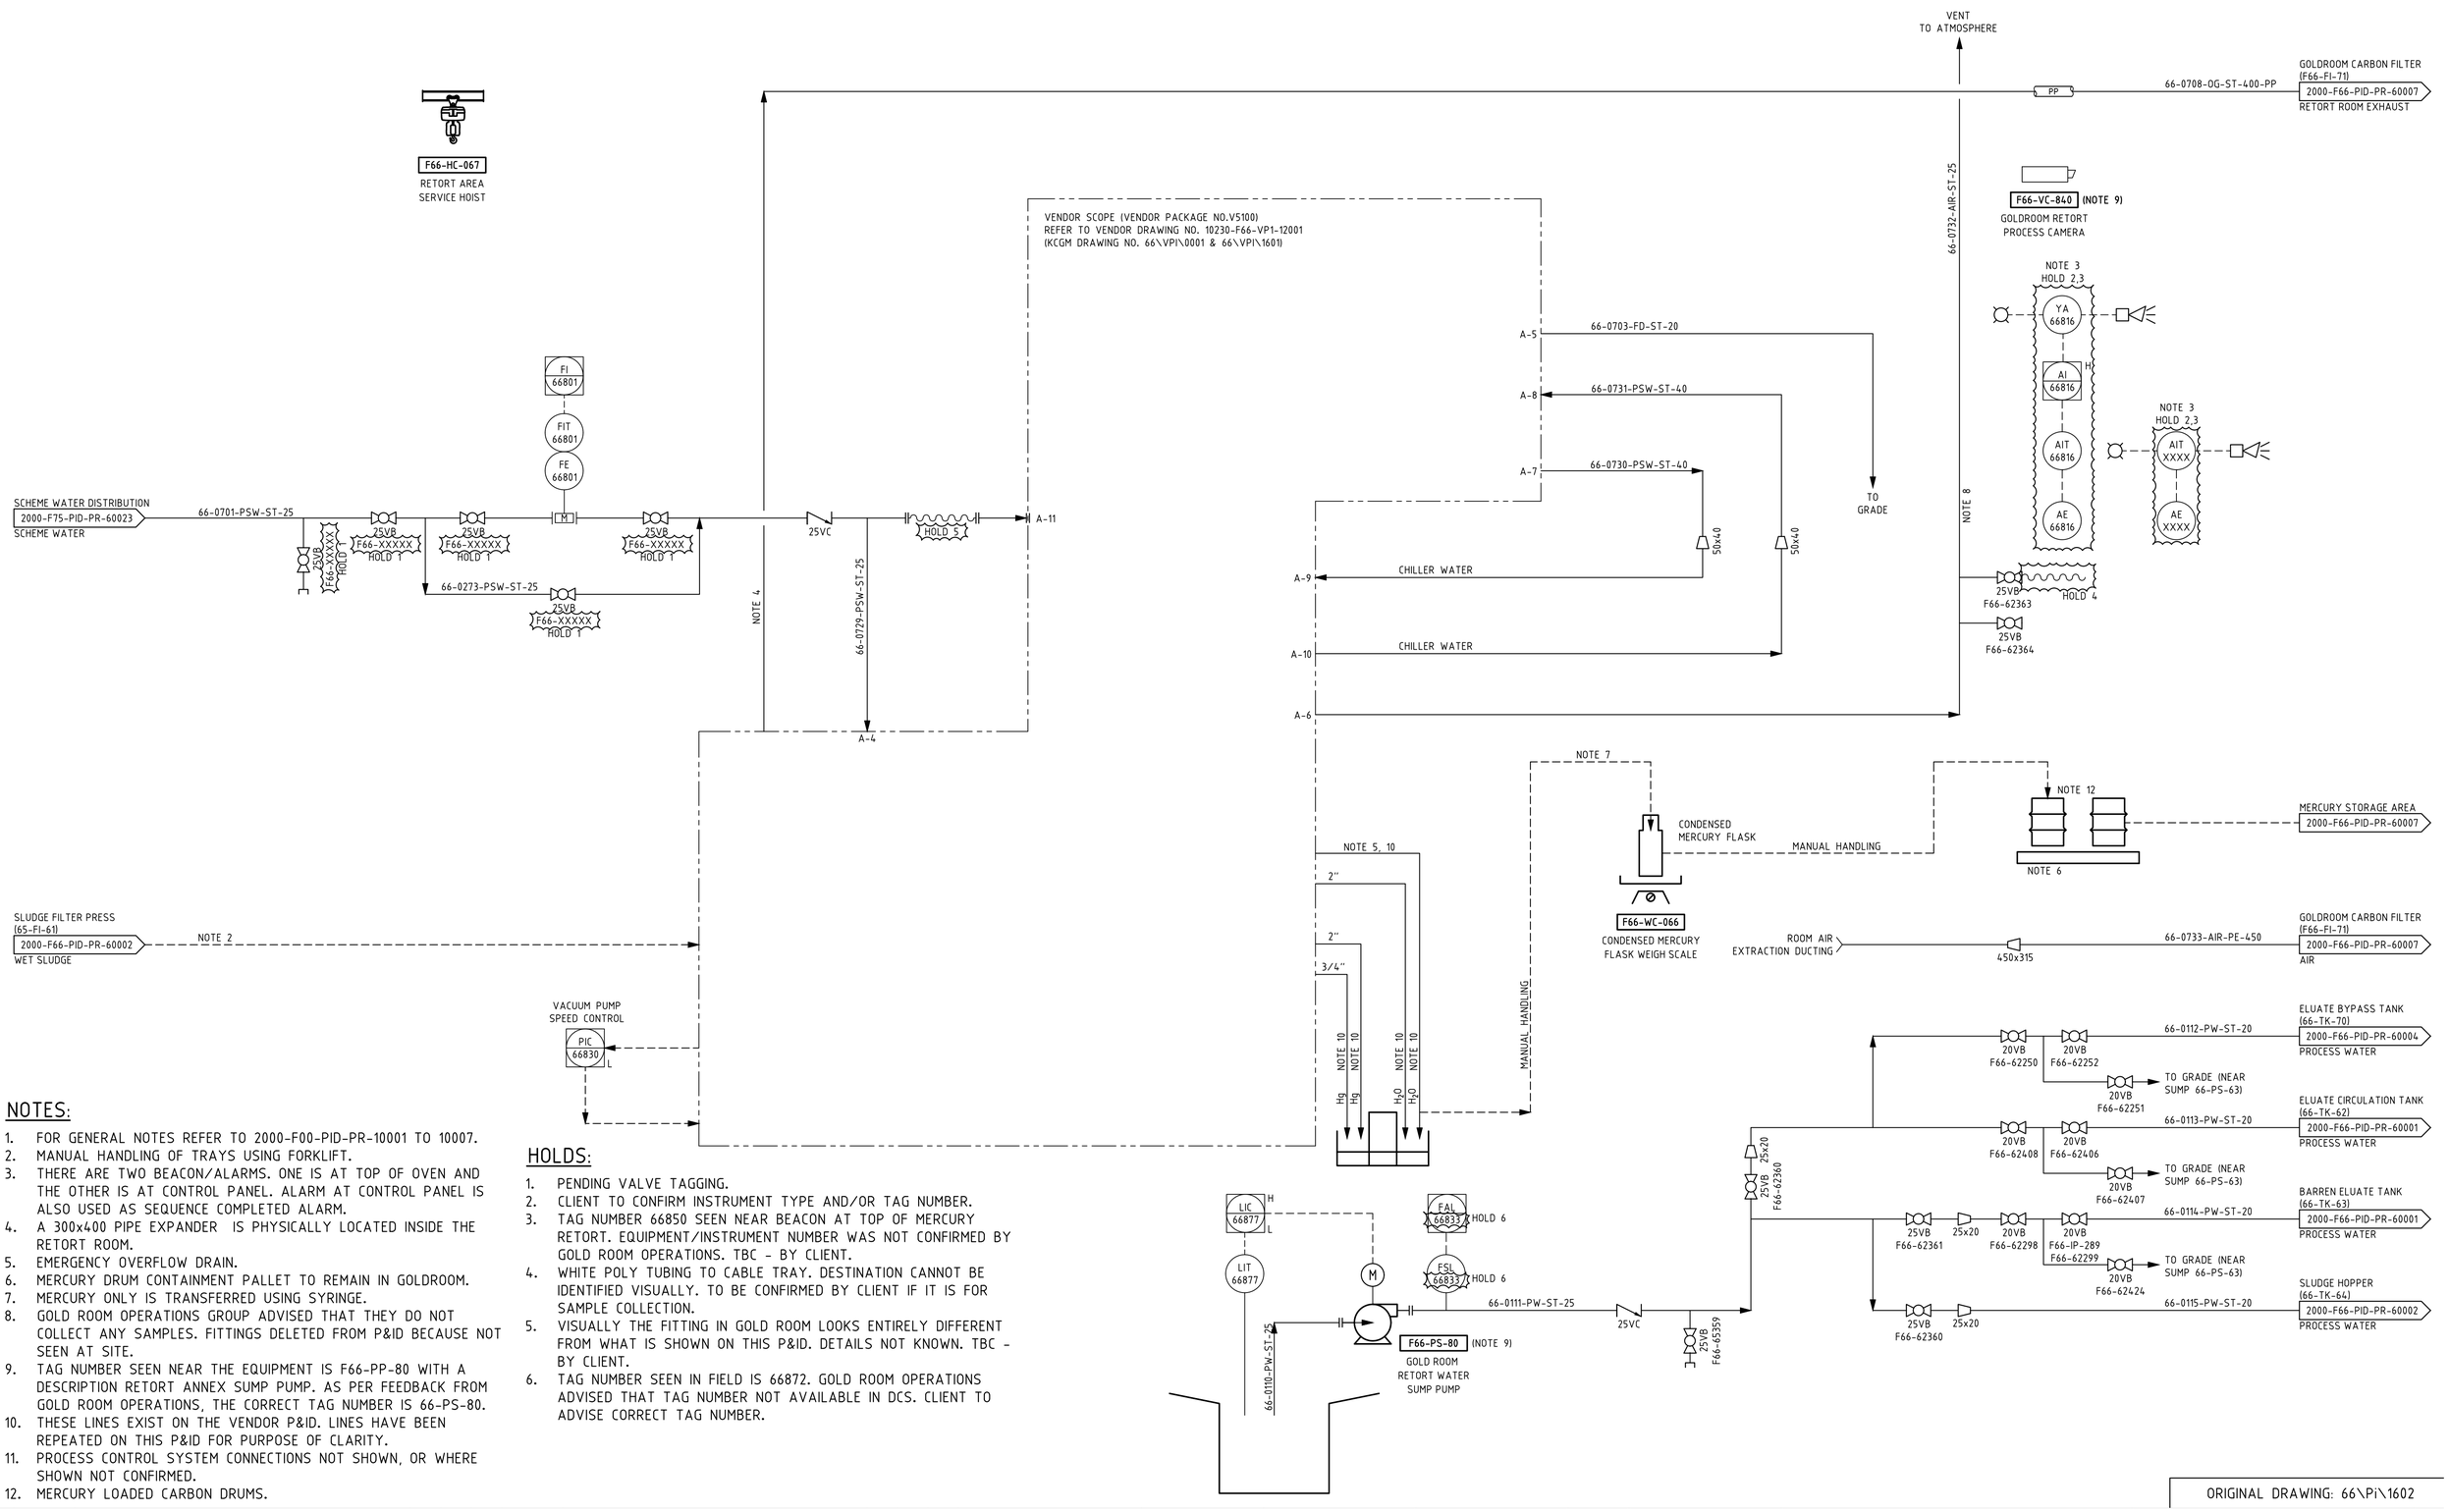


NOTES:

1. FOR GENERAL NOTES REFER TO 2000-F00-PID-PR-10001 TO 10007.
2. MANUAL HANDLING OF TRAYS USING FORKLIFT.
3. THERE ARE TWO BEACON/ALARMS. ONE IS AT TOP OF OVEN AND THE OTHER IS AT CONTROL PANEL. ALARM AT CONTROL PANEL IS ALSO USED AS SEQUENCE COMPLETED ALARM.
4. A 300x400 PIPE EXPANDER IS PHYSICALLY LOCATED INSIDE THE RETORT ROOM.
5. EMERGENCY OVERFLOW DRAIN.
6. MERCURY DRUM CONTAINMENT PALLET TO REMAIN IN GOLDROOM.
7. MERCURY ONLY IS TRANSFERRED USING SYRINGE.
8. GOLD ROOM OPERATIONS GROUP ADVISED THAT THEY DO NOT COLLECT ANY SAMPLES. FITTINGS DELETED FROM P&ID BECAUSE NOT SEEN AT SITE.
9. TAG NUMBER SEEN NEAR THE EQUIPMENT IS F66-PP-80 WITH A DESCRIPTION RETORT ANNEX SUMP PUMP. AS PER FEEDBACK FROM GOLD ROOM OPERATIONS, THE CORRECT TAG NUMBER IS 66-PS-80.
10. THESE LINES EXIST ON THE VENDOR P&ID. LINES HAVE BEEN REPEATED ON THIS P&ID FOR PURPOSE OF CLARITY.
11. PROCESS CONTROL SYSTEM CONNECTIONS NOT SHOWN, OR WHERE SHOWN NOT CONFIRMED.
12. MERCURY LOADED CARBON DRUMS.

HOLDS:

1. PENDING VALVE TAGGING.
2. CLIENT TO CONFIRM INSTRUMENT TYPE AND/OR TAG NUMBER.
3. TAG NUMBER 66850 SEEN NEAR BEACON AT TOP OF MERCURY RETORT. EQUIPMENT/INSTRUMENT NUMBER WAS NOT CONFIRMED BY GOLD ROOM OPERATIONS. TBC - BY CLIENT.
4. WHITE POLY TUBING TO CABLE TRAY. DESTINATION CANNOT BE IDENTIFIED VISUALLY. TO BE CONFIRMED BY CLIENT IF IT IS FOR SAMPLE COLLECTION.
5. VISUALLY THE FITTING IN GOLD ROOM LOOKS ENTIRELY DIFFERENT FROM WHAT IS SHOWN ON THIS P&ID. DETAILS NOT KNOWN. TBC - BY CLIENT.
6. TAG NUMBER SEEN IN FIELD IS 66872. GOLD ROOM OPERATIONS ADVISED THAT TAG NUMBER NOT AVAILABLE IN DCS. CLIENT TO ADVISE CORRECT TAG NUMBER.

ORIGINAL DRAWING: 66\Pi\1602