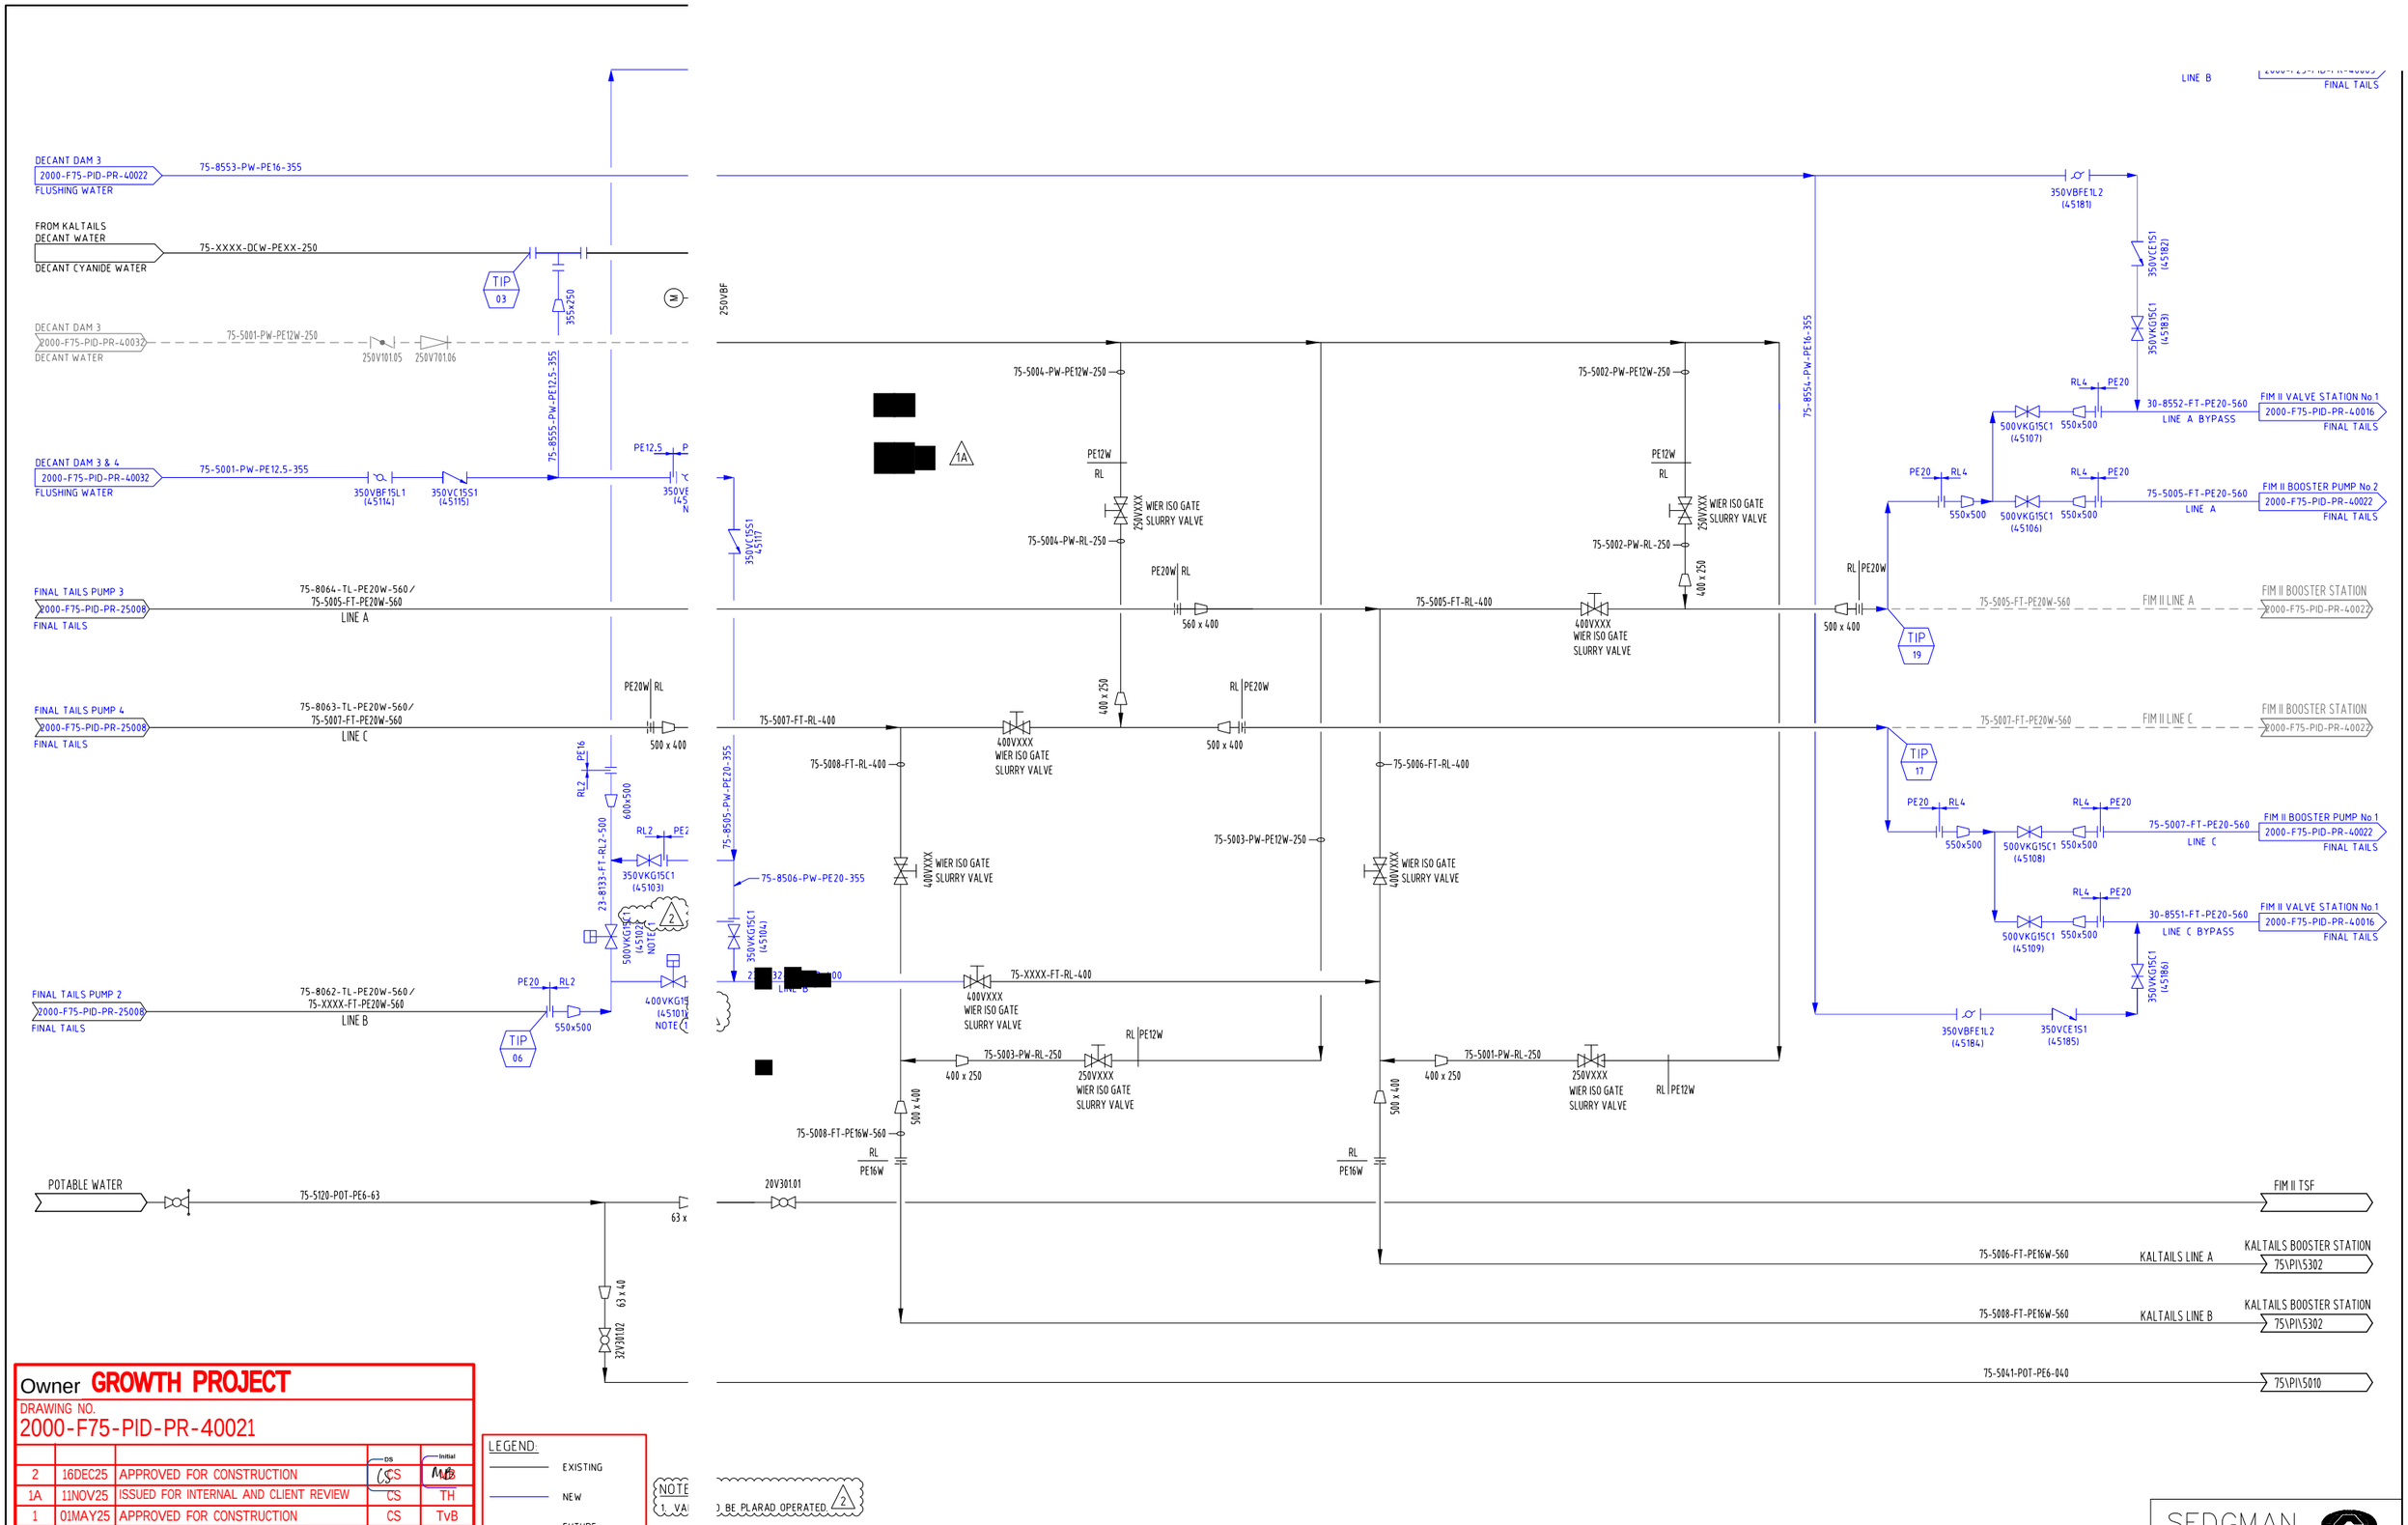


Owner **GROWTH PROJECT**

DRAWING NO.
2000-F75-PID-PR-40021

REV	DATE	DESCRIPTION	DS CHECK	Initial TECH APP
2	16DEC25	APPROVED FOR CONSTRUCTION	CS	MvB
1A	11NOV25	ISSUED FOR INTERNAL AND CLIENT REVIEW	CS	TH
1	01MAY25	APPROVED FOR CONSTRUCTION	CS	TvB
0	05DEC24	APPROVED FOR CONSTRUCTION	CS	TvB

MK	DATE	REVISION	BY	CKD	APP
4	21 JULY 2019	GENERAL REVIS			
3	06 APRIL 2018	FIM LOM TAILIN			
2	15 NOV 2012	ISSUED FOR AS			
1		GENERAL REVIS			
0		ISSUED FOR CO			

REVISION	BY	CKD	ENG CHK	APP	REFERENCE DRAWINGS	DWG NO.
	JM					
	JM					
	GAO	AG				
	MAL	AJC	JC	JE		

SCALE	NTS
DRAWN	MAL 1.10.09
DESIGNED	JC 1.2.10
CHECKED	AJC 28.1.10
APPROVED	JE 1.2.10
PROJ.APP	
PROJ. FILE #	

SEDGMAN Limited A.B.N. 86 088 471 667 ISO 2006

SEDGMAN DRG No. 0251-2-2-0010 SEDGMAN JOB No. 0251

FIMISTON PLANT
WATER TREATMENT FIMISTON
KALTAILS TSF RECOMMISSIONING
PIPING & INSTRUMENTATION DIAGRAM - KEARNS CORNER

SIZE	DRAWING NUMBER	REV
A1	75\PI\5001	4

KALGOORLIE CONSOLIDATED GOLD MINES PTY. LTD. ABN 009 377 619 003

PLOT DATE: 22/02/19 - 09:43 - Cad File: P:\0251 - Kaltails Recommissioning\26 CAD\27\0251-2-2-4098.dwg [0251-2-2-4098] - Printed by: mark.lawson