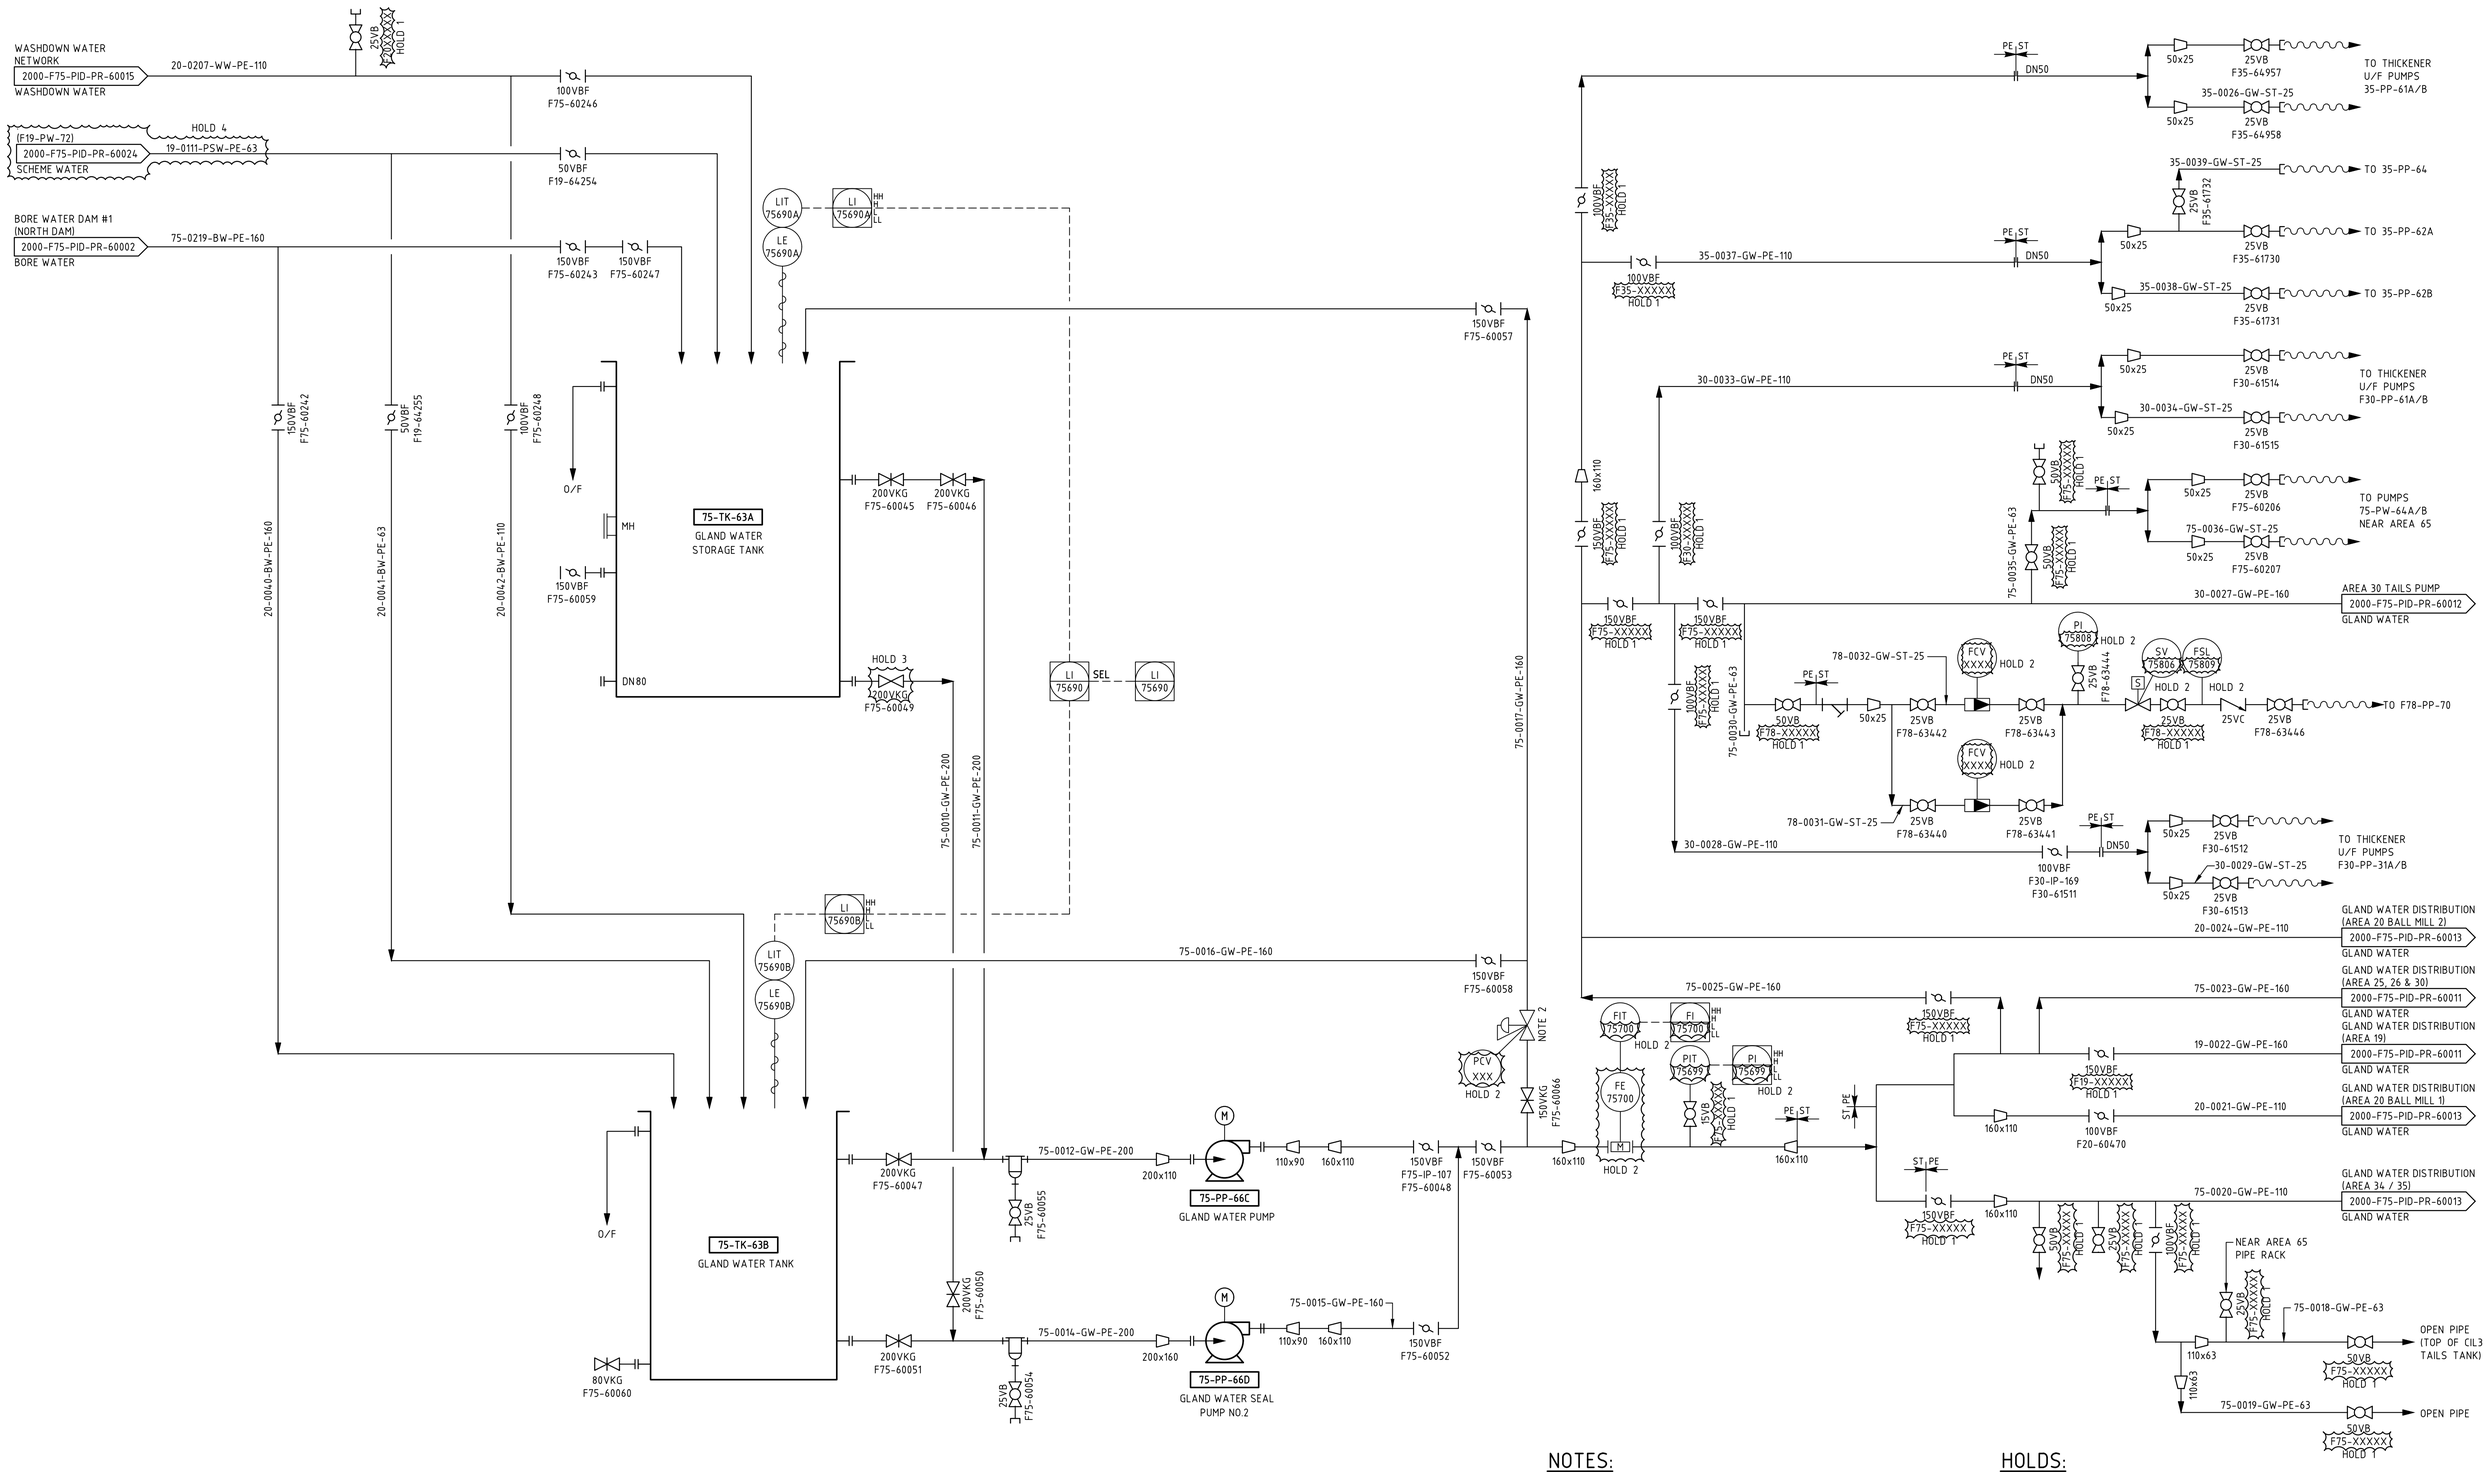


NOTES:

1. FOR GENERAL NOTES REFER TO 2000-F00-PID-PR-10001 TO 10007
2. SITE INDICATED THIS IS A PRESSURE SUSTAINING VALVE NOT IN OPERATION.
3. DETAILS MARKED UP ARE AS SIGHTED DURING SITE INSPECTION.
4. PROCESS CONTROL SYSTEM CONNECTIONS NOT SHOWN, OR WHERE SHOWN NOT CONFIRMED.

HOLDS:

1. PENDING VALVE TAGGING.
2. CLIENT TO CONFIRM INSTRUMENT TYPE AND/OR TAG NUMBER.
3. VALVE TYPE - TBC AT SITE.
4. PROCESS WATER STICKERS ARE MARKED AT SITE FOR THESE LINES. HOWEVER PROCESS SCHEME WATER HAS BEEN USED BY CPC. CLIENT TO CONFIRM THE SERVICE CODE FOR THESE PIPING.

ORIGINAL DRAWING: 71\PI\0504