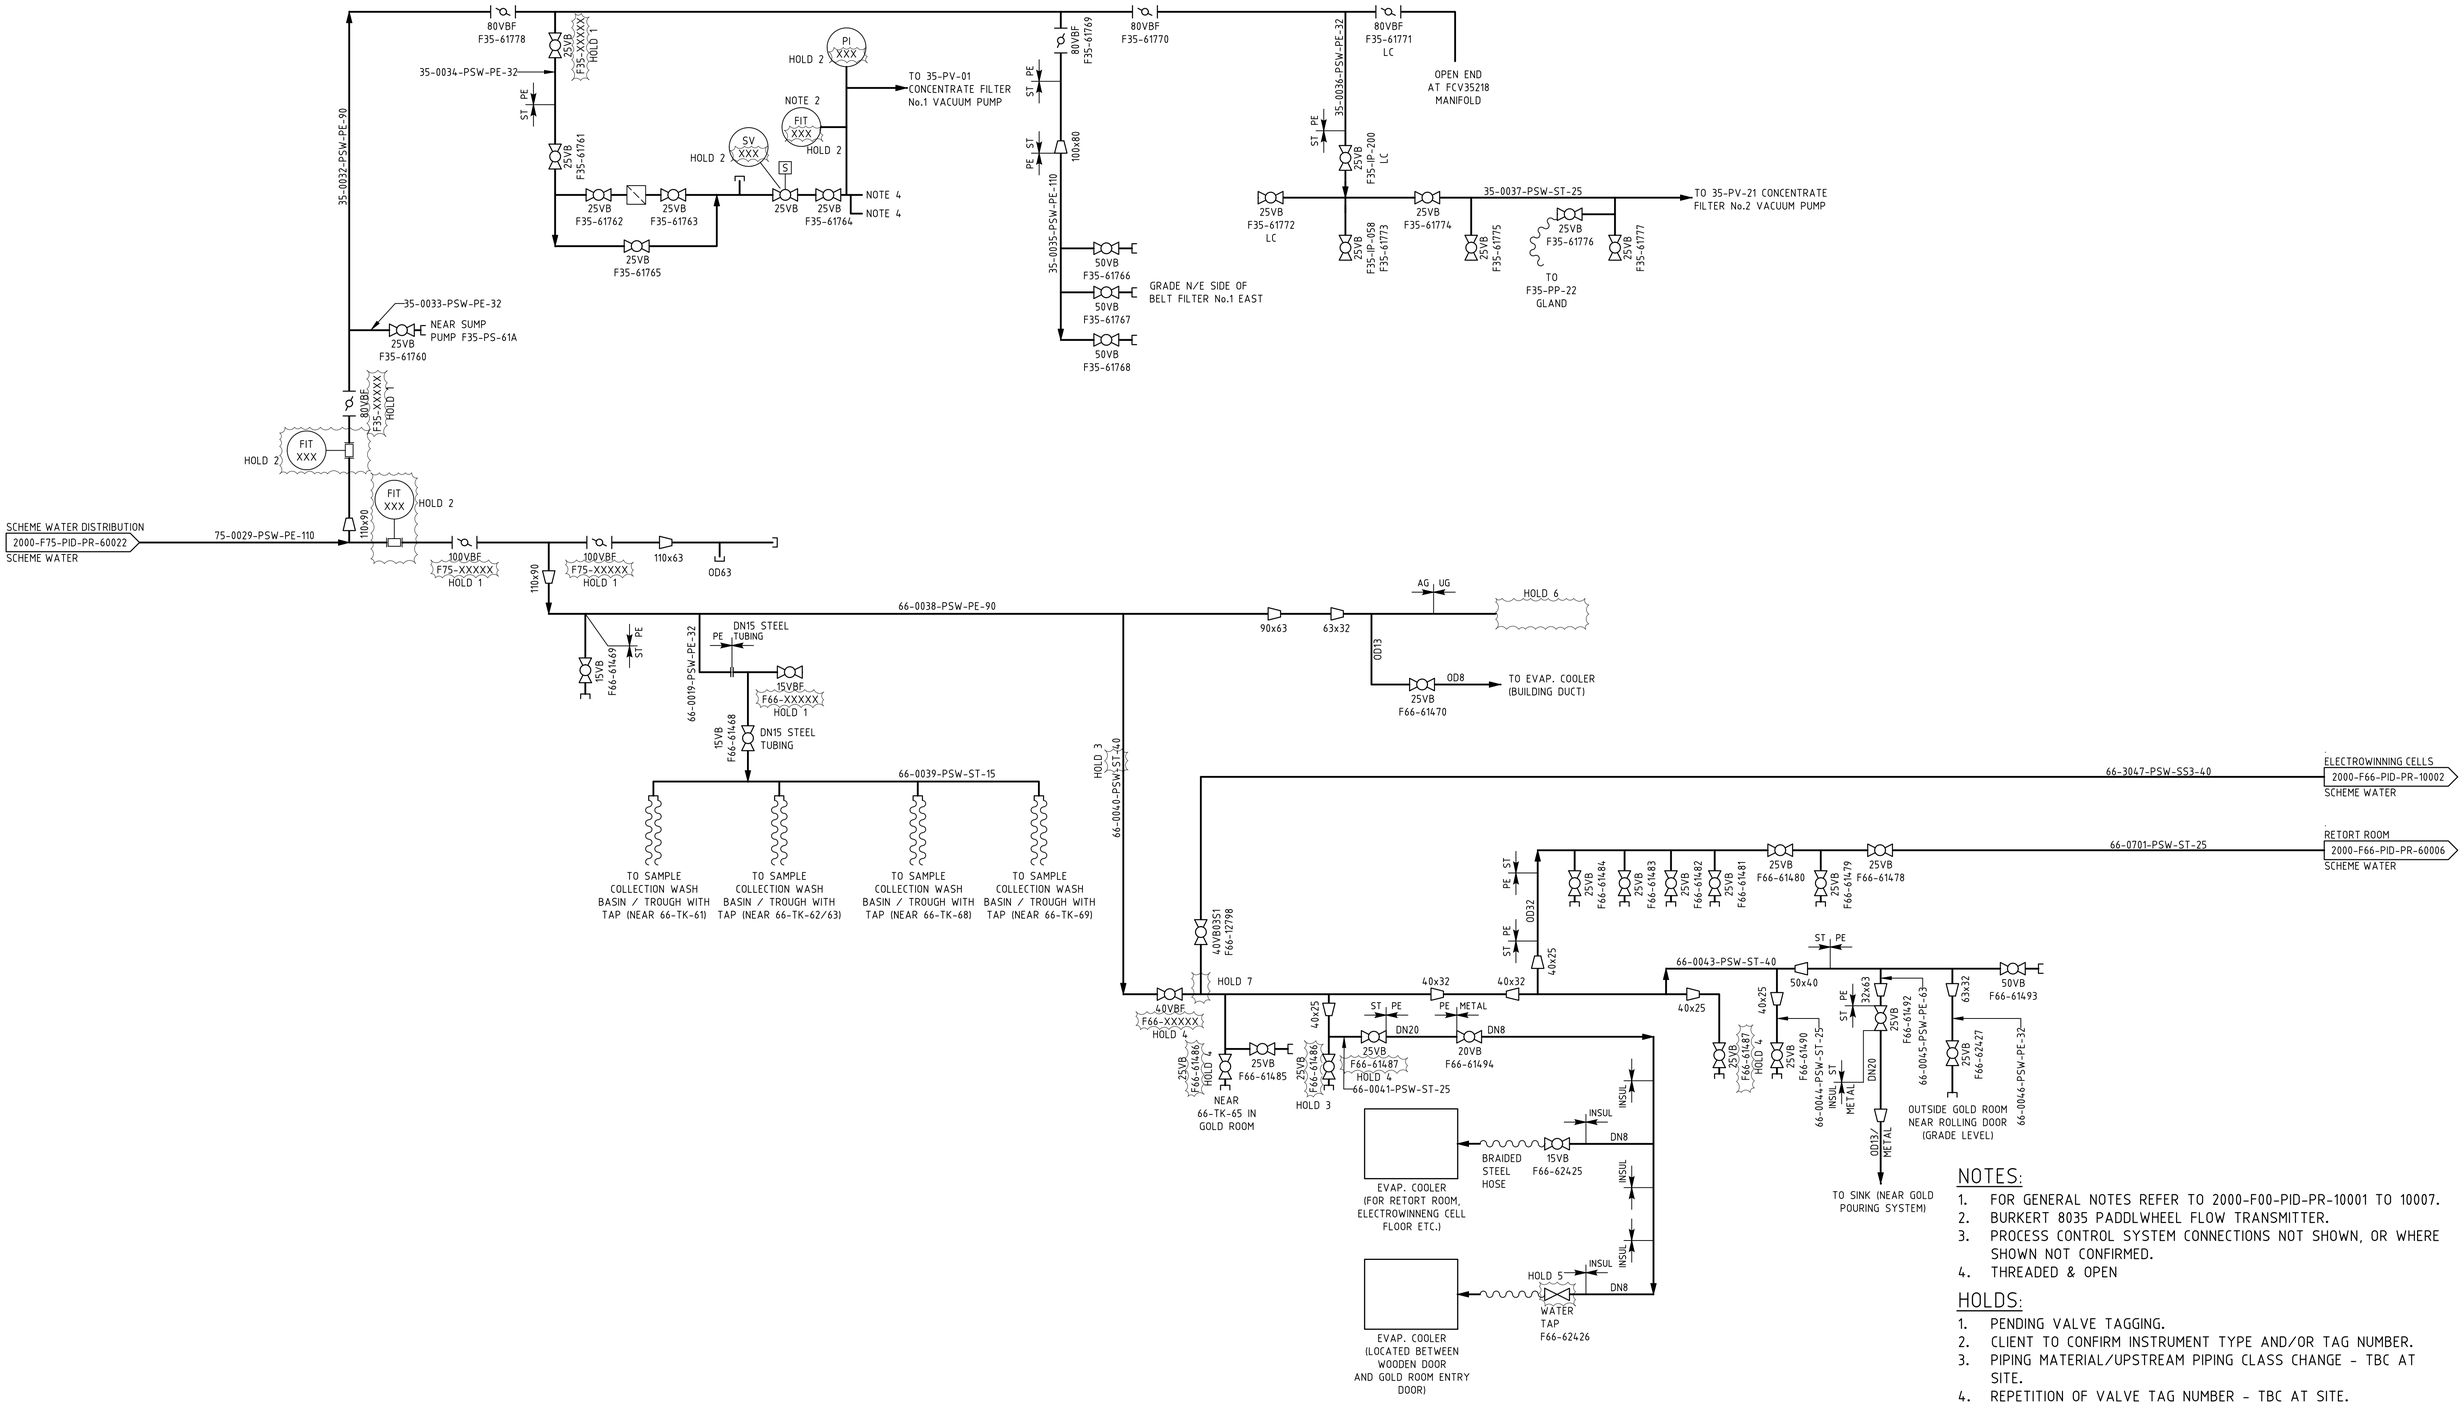


NOTES:

1. FOR GENERAL NOTES REFER TO 2000-F00-PID-PR-10001 TO 10007.
2. BURKERT 8035 PADDLWHEEL FLOW TRANSMITTER.
3. PROCESS CONTROL SYSTEM CONNECTIONS NOT SHOWN, OR WHERE SHOWN NOT CONFIRMED.
4. THREADED & OPEN

HOLDS:

1. PENDING VALVE TAGGING.
2. CLIENT TO CONFIRM INSTRUMENT TYPE AND/OR TAG NUMBER.
3. PIPING MATERIAL/UPSTREAM PIPING CLASS CHANGE - TBC AT SITE.
4. REPETITION OF VALVE TAG NUMBER - TBC AT SITE.
5. VALVE TYPE TBC AT SITE.
6. UNDERGROUND PIPING CONTINUATION OUTSIDE GOLD ROOM UNKNOWN - TBC BY CLIENT.
7. TIE IN POINT (TIP-1055) LOCATION TO BE CONFIRMED.