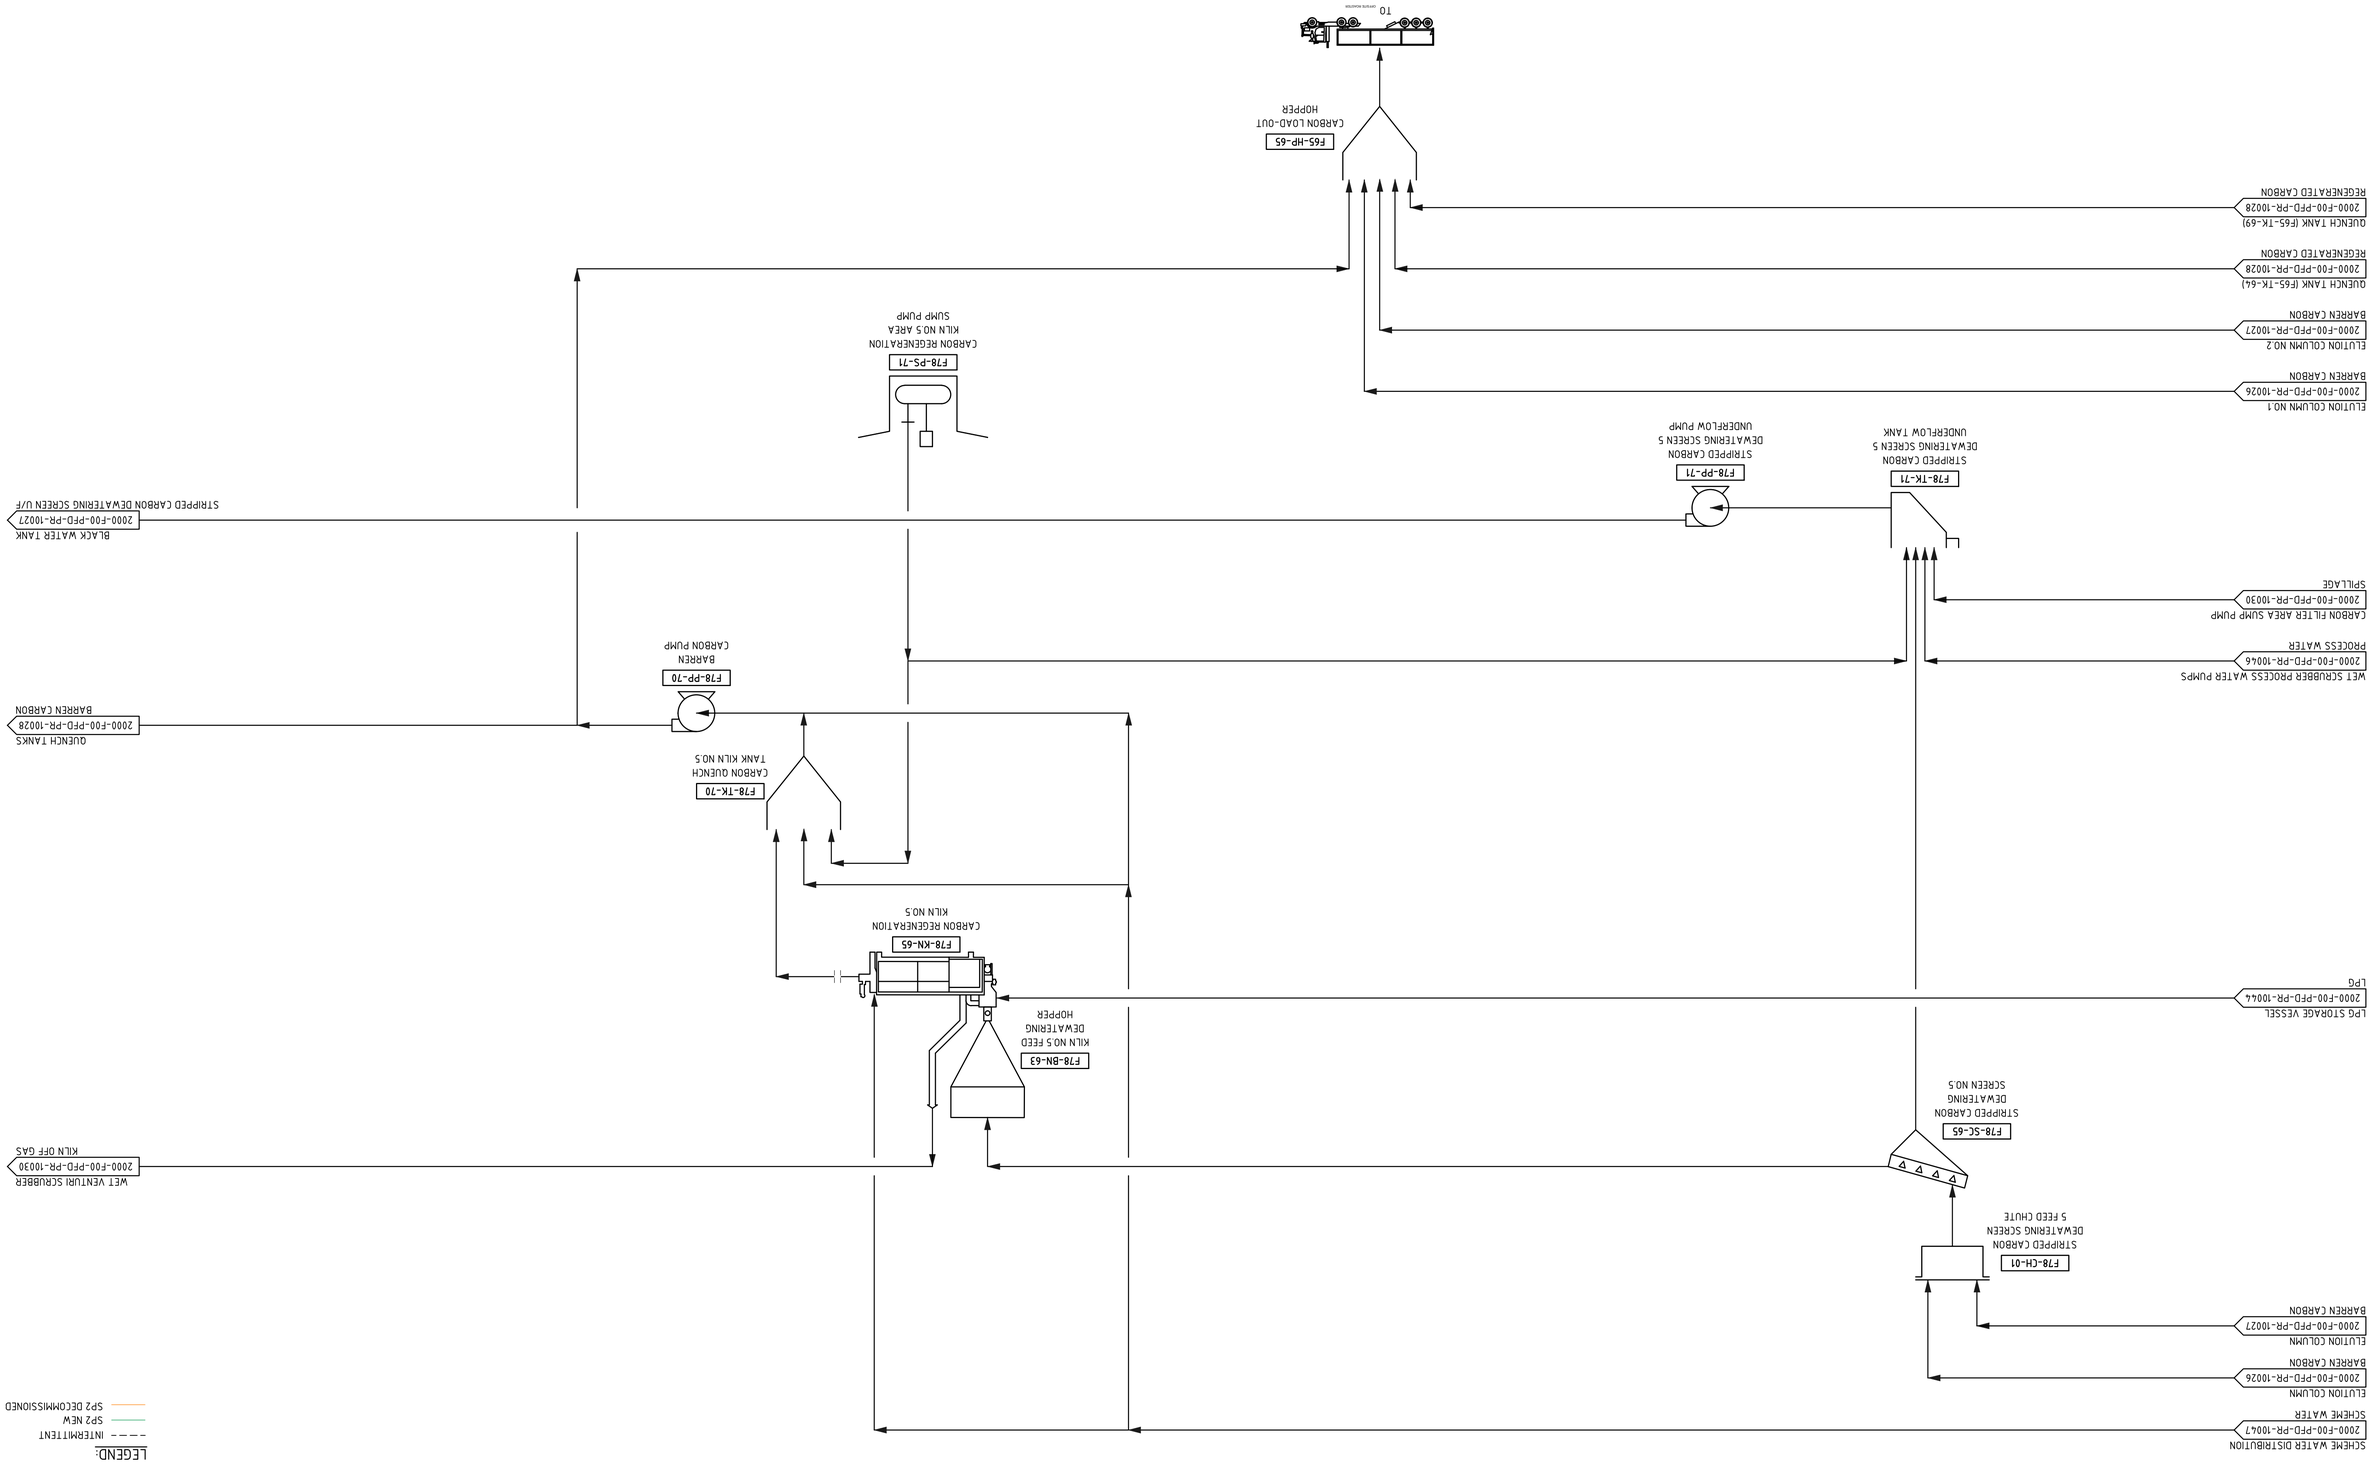

TO
DRYING MACHINE
F65-HP-65
CARBON LOAD-OUT HOPPER
QUENCH TANK (F65-TK-69)
2000-F00-PFD-PR-10028
REGENERATED CARBON
QUENCH TANK (F65-TK-64)
2000-F00-PFD-PR-10028
REGENERATED CARBON
ELUTION COLUMN NO.2
2000-F00-PFD-PR-10027
BARREN CARBON
ELUTION COLUMN NO.1
2000-F00-PFD-PR-10026
BARREN CARBON
F78-PS-71
CARBON REGENERATION KILN NO.5 AREA SUMP PUMP
F78-PP-71
STRIPPED CARBON DEWATERING SCREEN S UNDERFLOW PUMP
F78-TK-71
STRIPPED CARBON DEWATERING SCREEN S UNDERFLOW TANK
CARBON FILTER AREA SUMP PUMP
2000-F00-PFD-PR-10030
SPILLAGE
WET SCRUBBER PROCESS WATER PUMPS
2000-F00-PFD-PR-10046
PROCESS WATER
BLACK WATER TANK
2000-F00-PFD-PR-10027
STRIPPED CARBON DEWATERING SCREEN U/F
F78-PP-70
BARREN CARBON PUMP
QUENCH TANKS
2000-F00-PFD-PR-10028
BARREN CARBON
F78-TK-70
CARBON QUENCH TANK KILN NO.5
F78-KN-65
CARBON REGENERATION KILN NO.5
F78-BN-63
KILN NO.5 FEED DEWATERING HOPPER
WET VENTURI SCRUBBER
2000-F00-PFD-PR-10030
KILN OFF GAS
LPG STORAGE VESSEL
2000-F00-PFD-PR-10044
LPG
F78-SC-65
STRIPPED CARBON DEWATERING SCREEN NO.5
F78-CH-01
STRIPPED CARBON DEWATERING SCREEN 5 FEED CHUTE
ELUTION COLUMN
2000-F00-PFD-PR-10027
BARREN CARBON
ELUTION COLUMN
2000-F00-PFD-PR-10026
BARREN CARBON
SCHEME WATER DISTRIBUTION
2000-F00-PFD-PR-10047
SCHEME WATER
LEGEND:
INTERMITTENT
SP2 NEW
SP2 DECOMMISSIONED