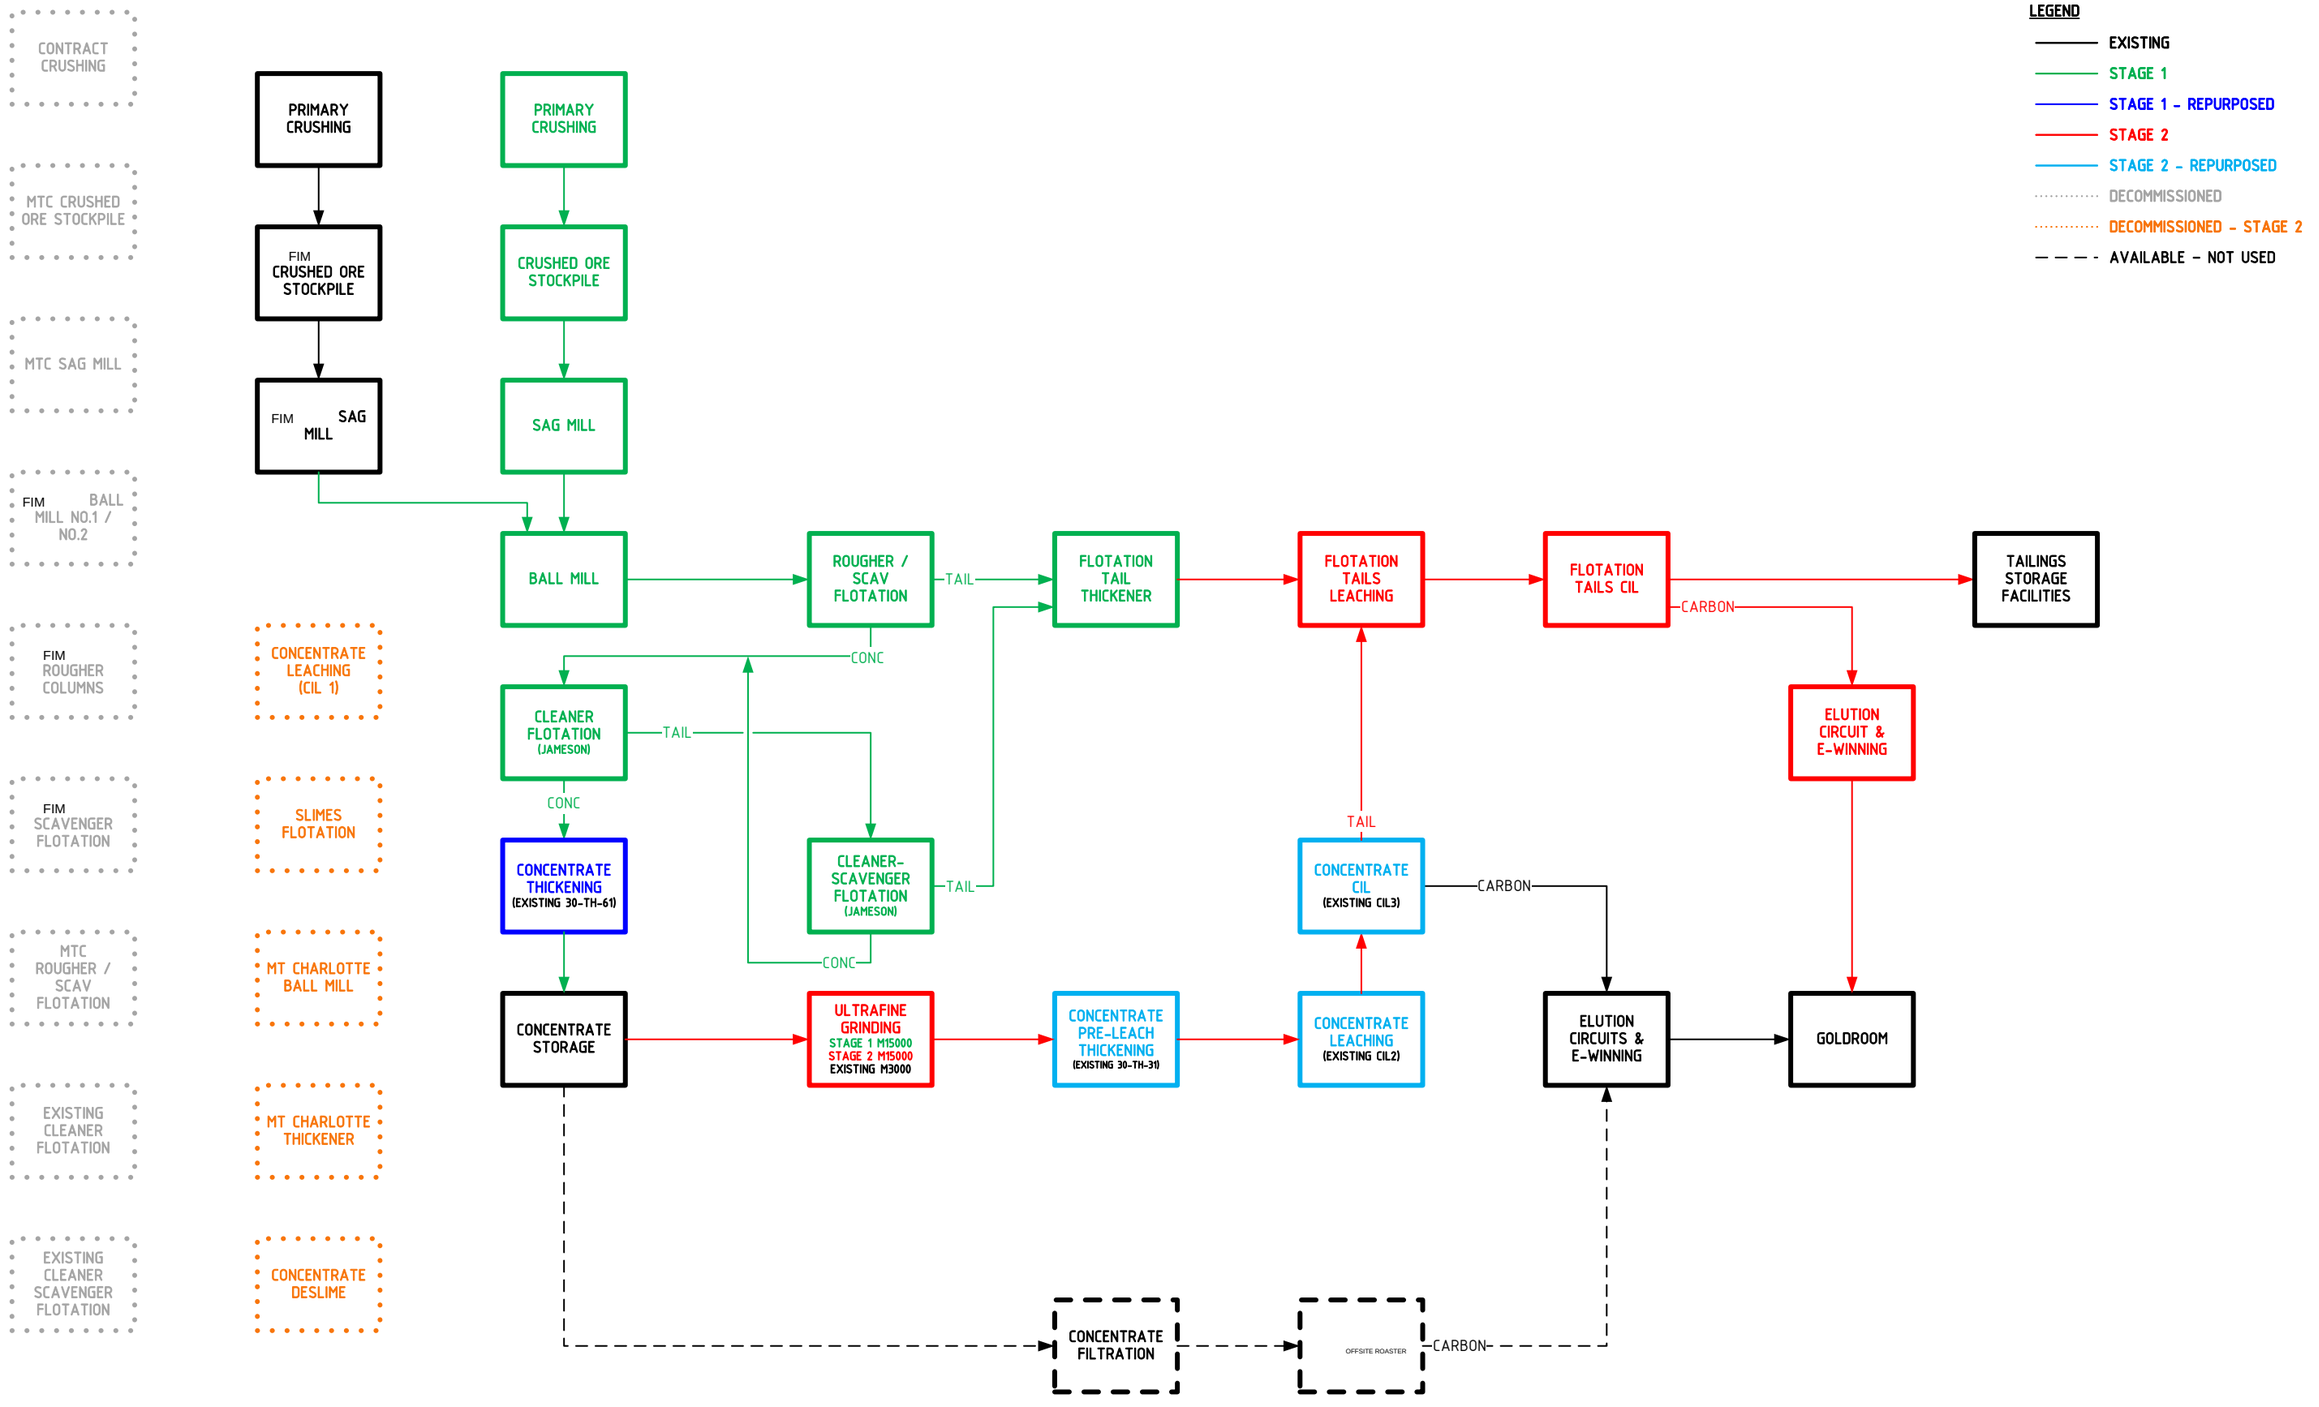

LEGEND
EXISTING
STAGE 1
STAGE 1 - REPURPOSED
STAGE 2
STAGE 2 - REPURPOSED
DECOMMISSIONED
DECOMMISSIONED - STAGE 2
AVAILABLE - NOT USED
CONTRACT CRUSHING
MTC CRUSHED ORE STOCKPILE
MTC SAG MILL
FIM BALL MILL NO.1 / NO.2
FIM ROUGHER COLUMNS
FIM SCAVENGER FLOTATION
MTC ROUGHER / SCAV FLOTATION
EXISTING CLEANER FLOTATION
EXISTING CLEANER SCAVENGER FLOTATION
CONCENTRATE LEACHING (CIL 1)
SLIMES FLOTATION
MT CHARLOTTE BALL MILL
MT CHARLOTTE THICKENER
CONCENTRATE DESLIME
PRIMARY CRUSHING
FIM CRUSHED ORE STOCKPILE
FIM SAG MILL
BALL MILL
PRIMARY CRUSHING
CRUSHED ORE STOCKPILE
SAG MILL
ROUGHER / SCAV FLOTATION
TAIL
CONC
CLEANER FLOTATION (JAMESON)
TAIL
CONC
CONCENTRATE THICKENING (EXISTING 30-TH-61)
CLEANER-SCAVENGER FLOTATION (JAMESON)
TAIL
CONC
CONCENTRATE STORAGE
ULTRAFINE GRINDING
STAGE 1 M15000
STAGE 2 M15000
EXISTING M3000
CONCENTRATE PRE-LEACH THICKENING (EXISTING 30-TH-31)
CONCENTRATE FILTRATION
OFFSITE ROASTER
CARBON
FLOTATION TAIL THICKENER
FLOTATION TAILS LEACHING
TAIL
CONCENTRATE CIL (EXISTING CIL3)
CONCENTRATE LEACHING (EXISTING CIL2)
FLOTATION TAILS CIL
CARBON
CARBON
ELUTION CIRCUIT & E-WINNING
ELUTION CIRCUITS & E-WINNING
TAILINGS STORAGE FACILITIES
GOLDROOM