
LEGEND:

- EXISTING
- NEW
- FUTURE
- DECOMMISSIONED

NOTES:

1. VALVES WILL BE HYDRAULICALLY ACTUATED VIA HYDRAULIC POWER PACK F23-HY-420.
2. DELETED
3. MANUAL OPERATED VALVE WITH PROXIMITY SWITCHES.
4. BURSTING DISC RUPTURE PRESSURE TO BE SUITABLE FOR INITIAL OPERATION. WILL BE REQUIRED TO BE REPLACED AT FINAL TSF HEIGHT.
5. DIFFERENTIAL FLOW CALCULATION FOR LEAK DETECTION.

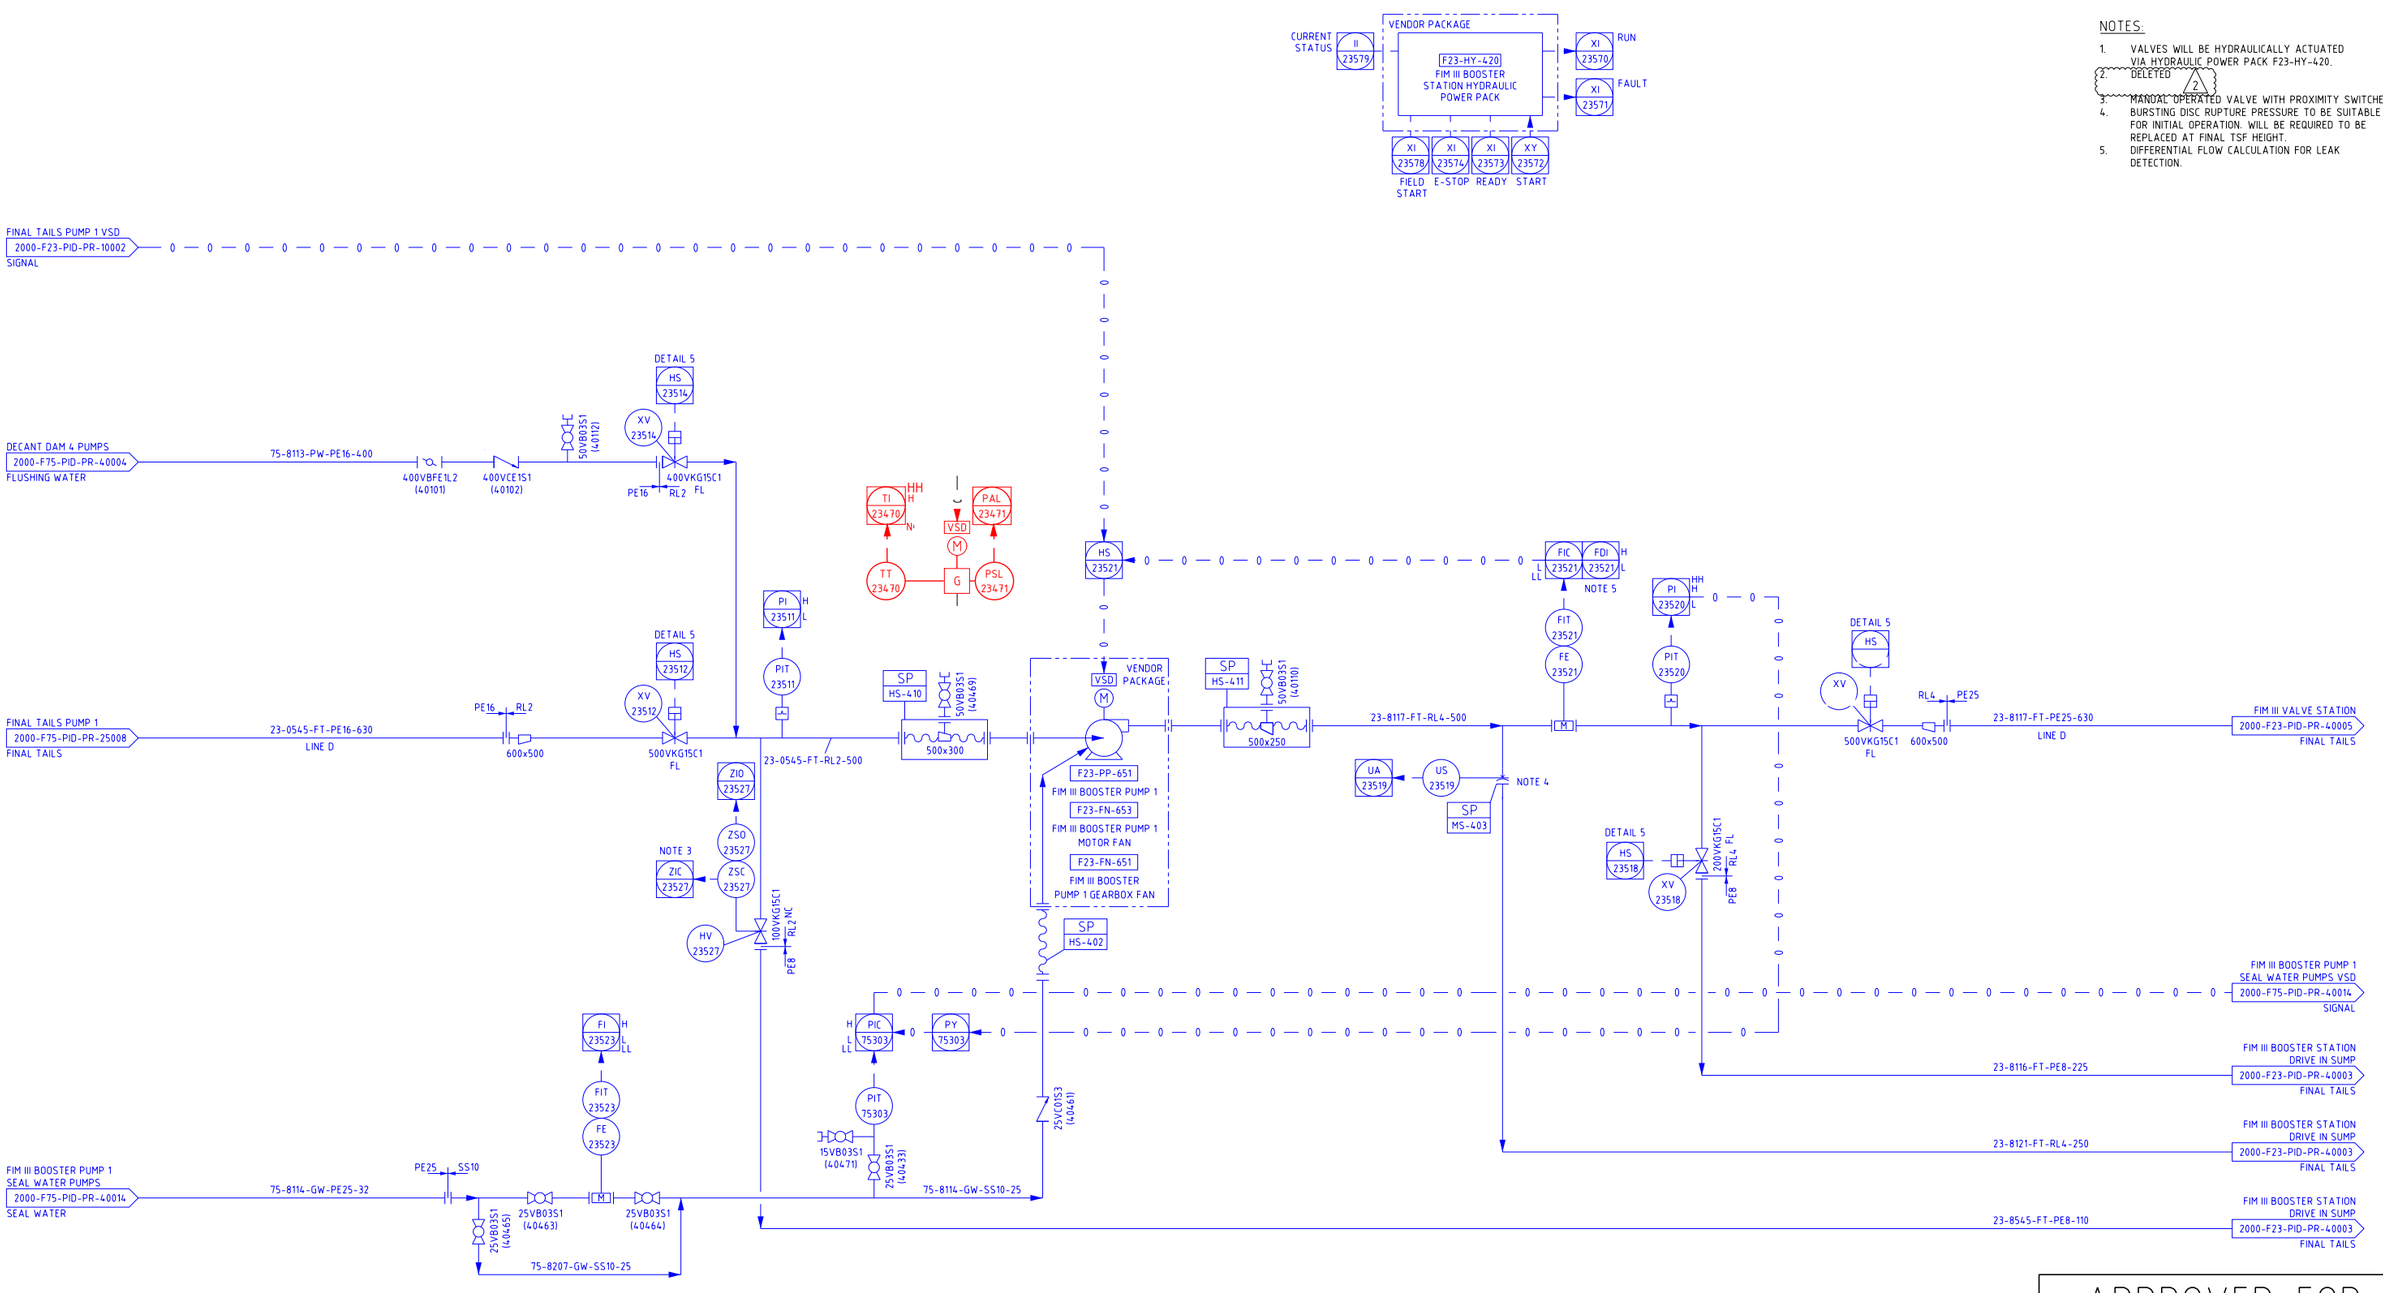

APPROVED FOR CONSTRUCTION