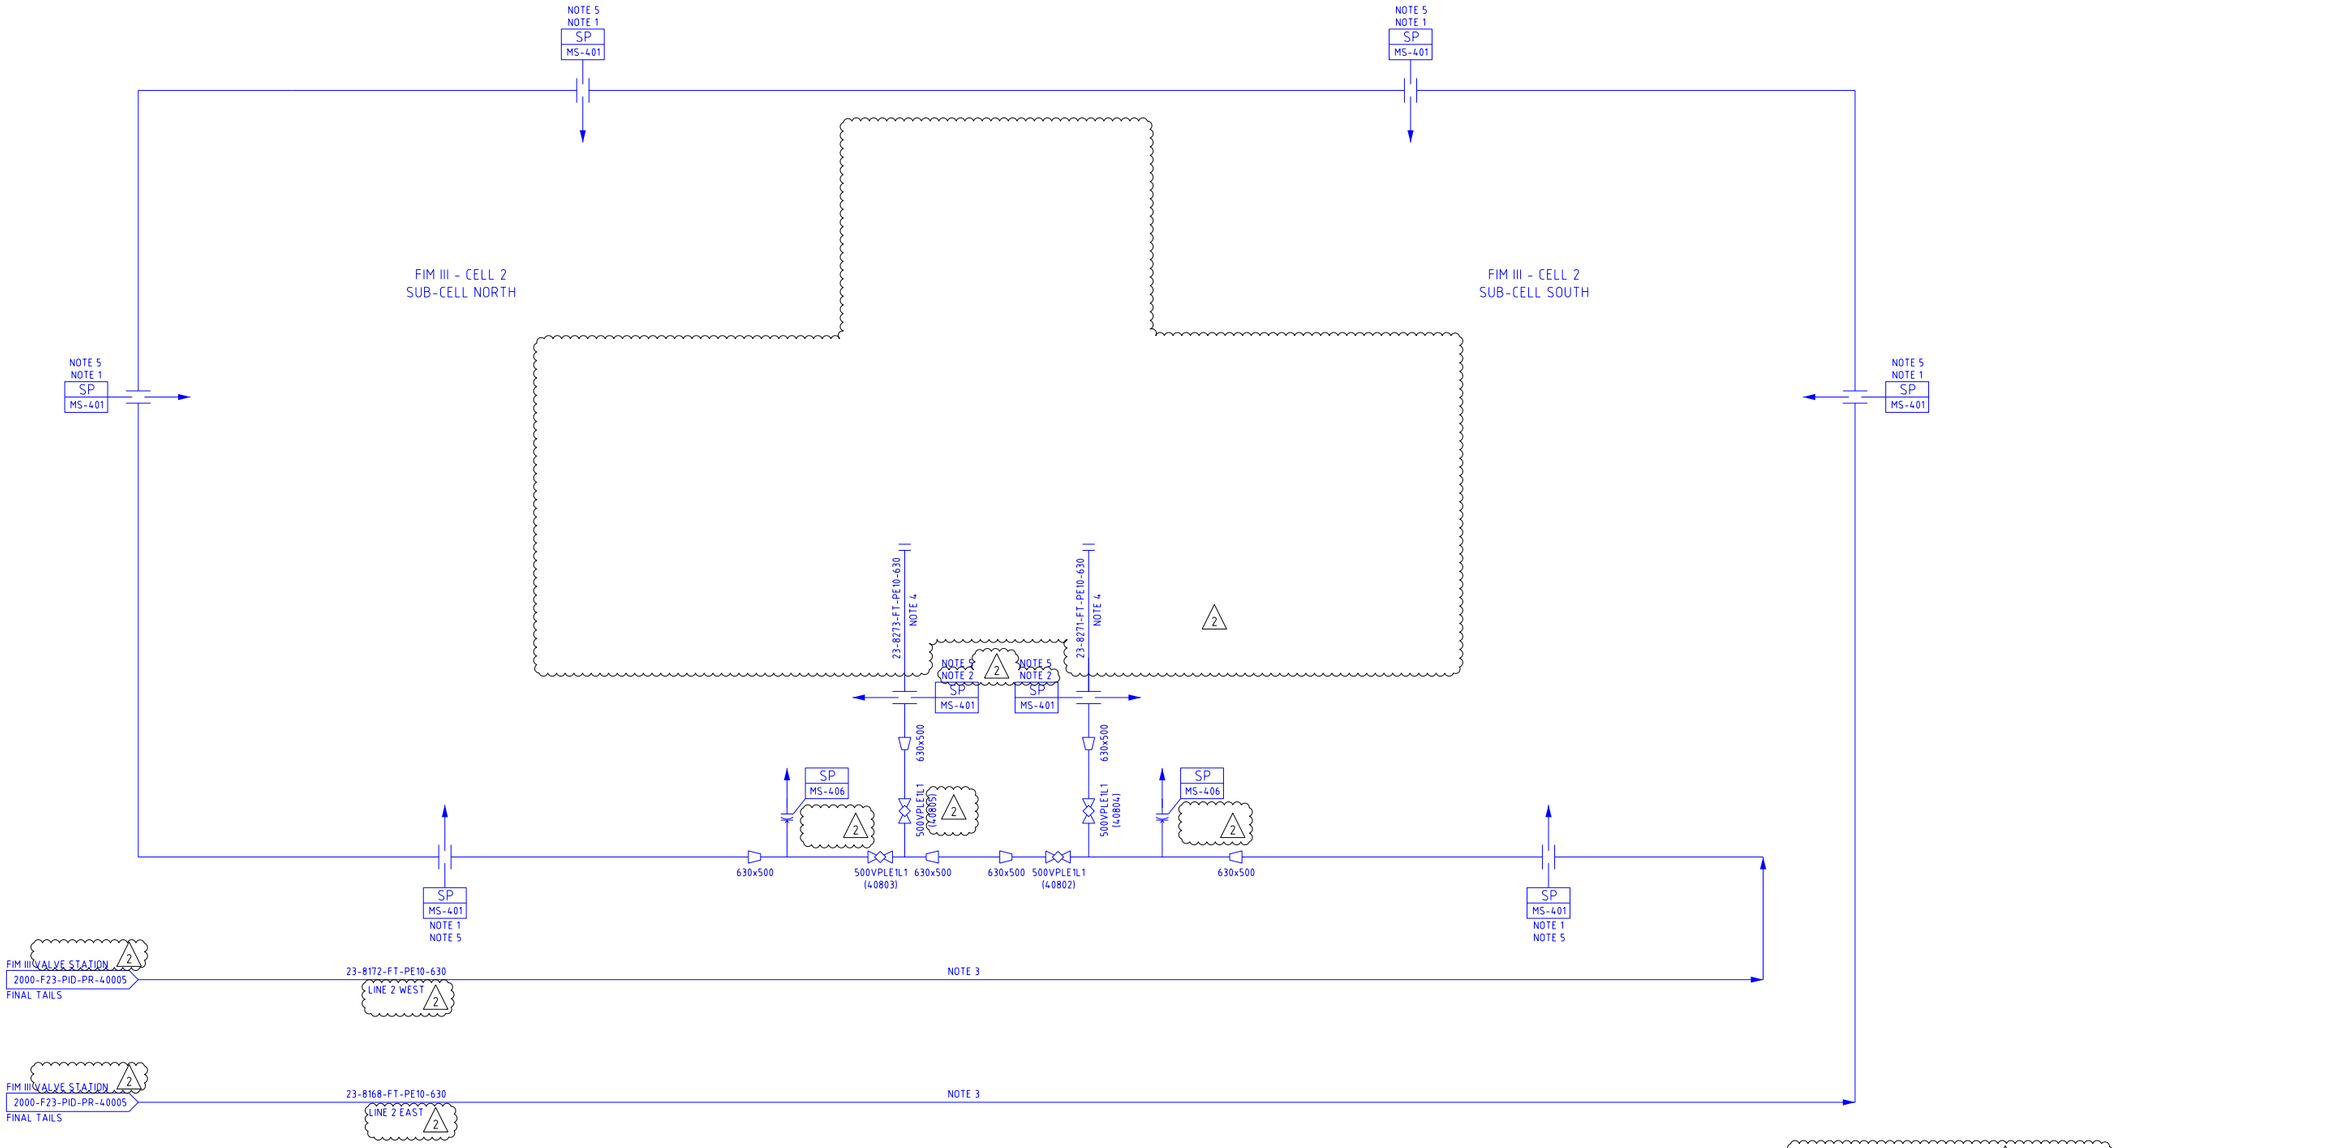

APPROVED FOR CONSTRUCTION

NOTES:

1. SPIGOTS PLACED AT 40m CENTRES ON THE EMBANKMENT.
2. SPIGOTS PLACED AT 15m CENTRES ON THE CAUSEWAYS.
3. PIPING ON TSF EMBANKMENT TO BE FLANGED EVERY 40m.
4. PIPING ON CAUSEWAY TO BE FLANGED EVERY 15m.
5. REFER TO DRAWING 2000-T03-DRG-GE-40003 FOR SPIGOT DETAILS. A TOTAL OF 187 SPIGOTS REQUIRED WITH UNIQUE VALVE NUMBERS 43401 TO 43587.

LEGEND:

- EXISTING
- NEW
- FUTURE
- DECOMMISSIONED