APPROVED FOR CONSTRUCTION

NOTES:
1. SPIGOTS PLACED AT 40m CENTRES ON TSF EMBANKMENT.
2. DELETED.
3. PIPING ON TSF EMBANKMENT TO BE FLANGED EVERY 40m.
4. DELETED.
5. REFER TO DRAWING 2000-T03-DRG-GE-40003 FOR SPIGOT DETAILS. A TOTAL OF 135 SPIGOTS REQUIRED WITH UNIQUE VALVE NUMBERS 43801 TO 43935. (2)
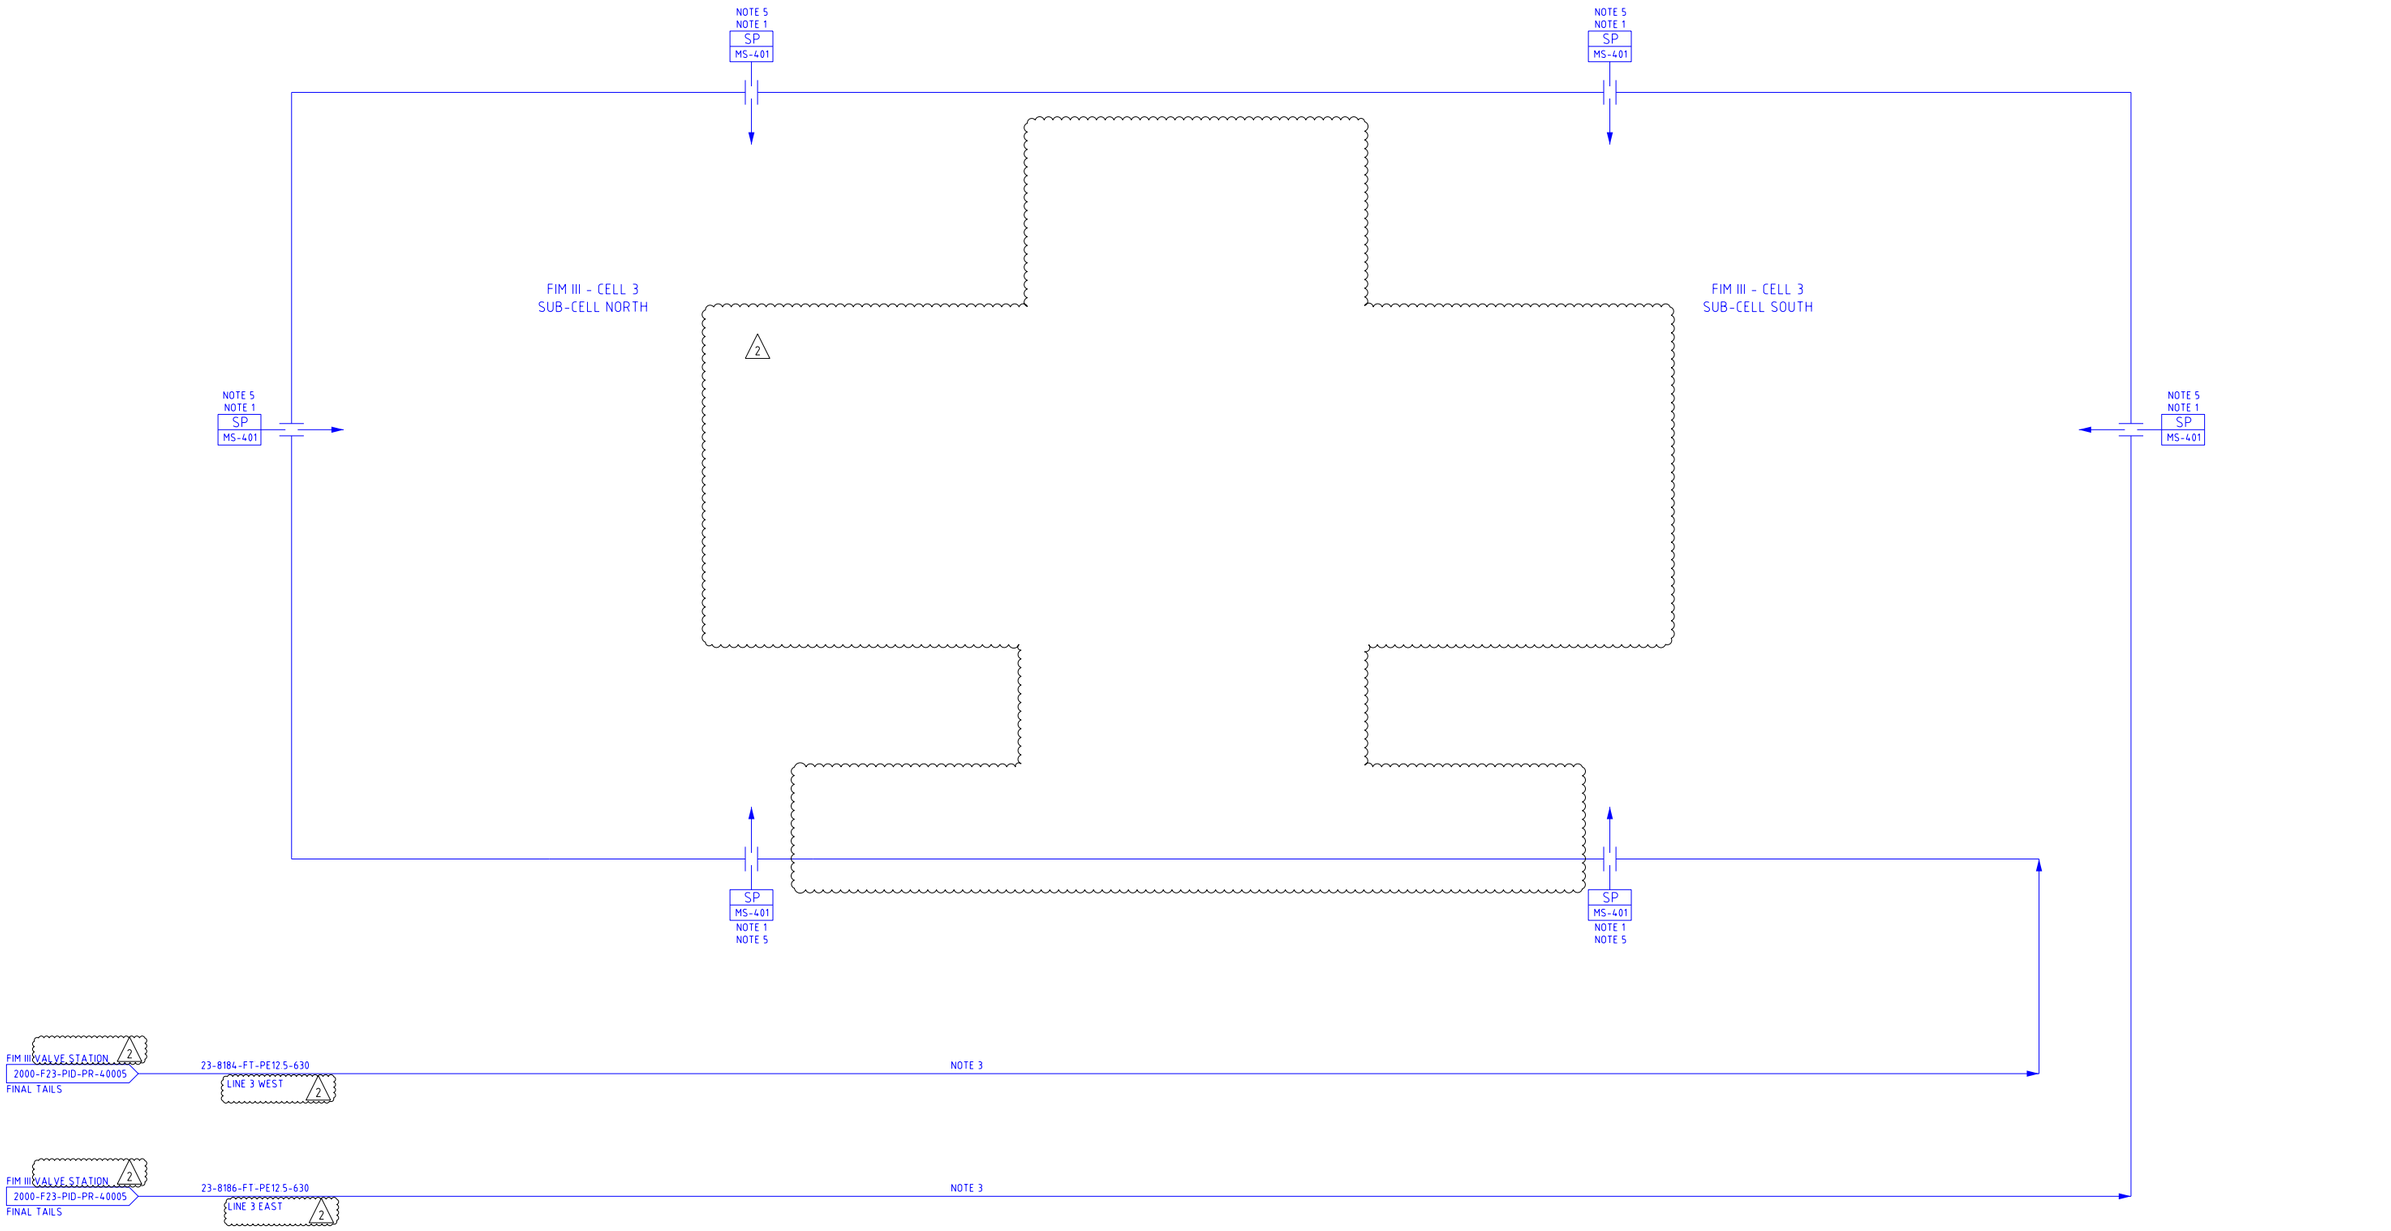
LEGEND:
- EXISTING
- NEW
- FUTURE
- DECOMMISSIONED