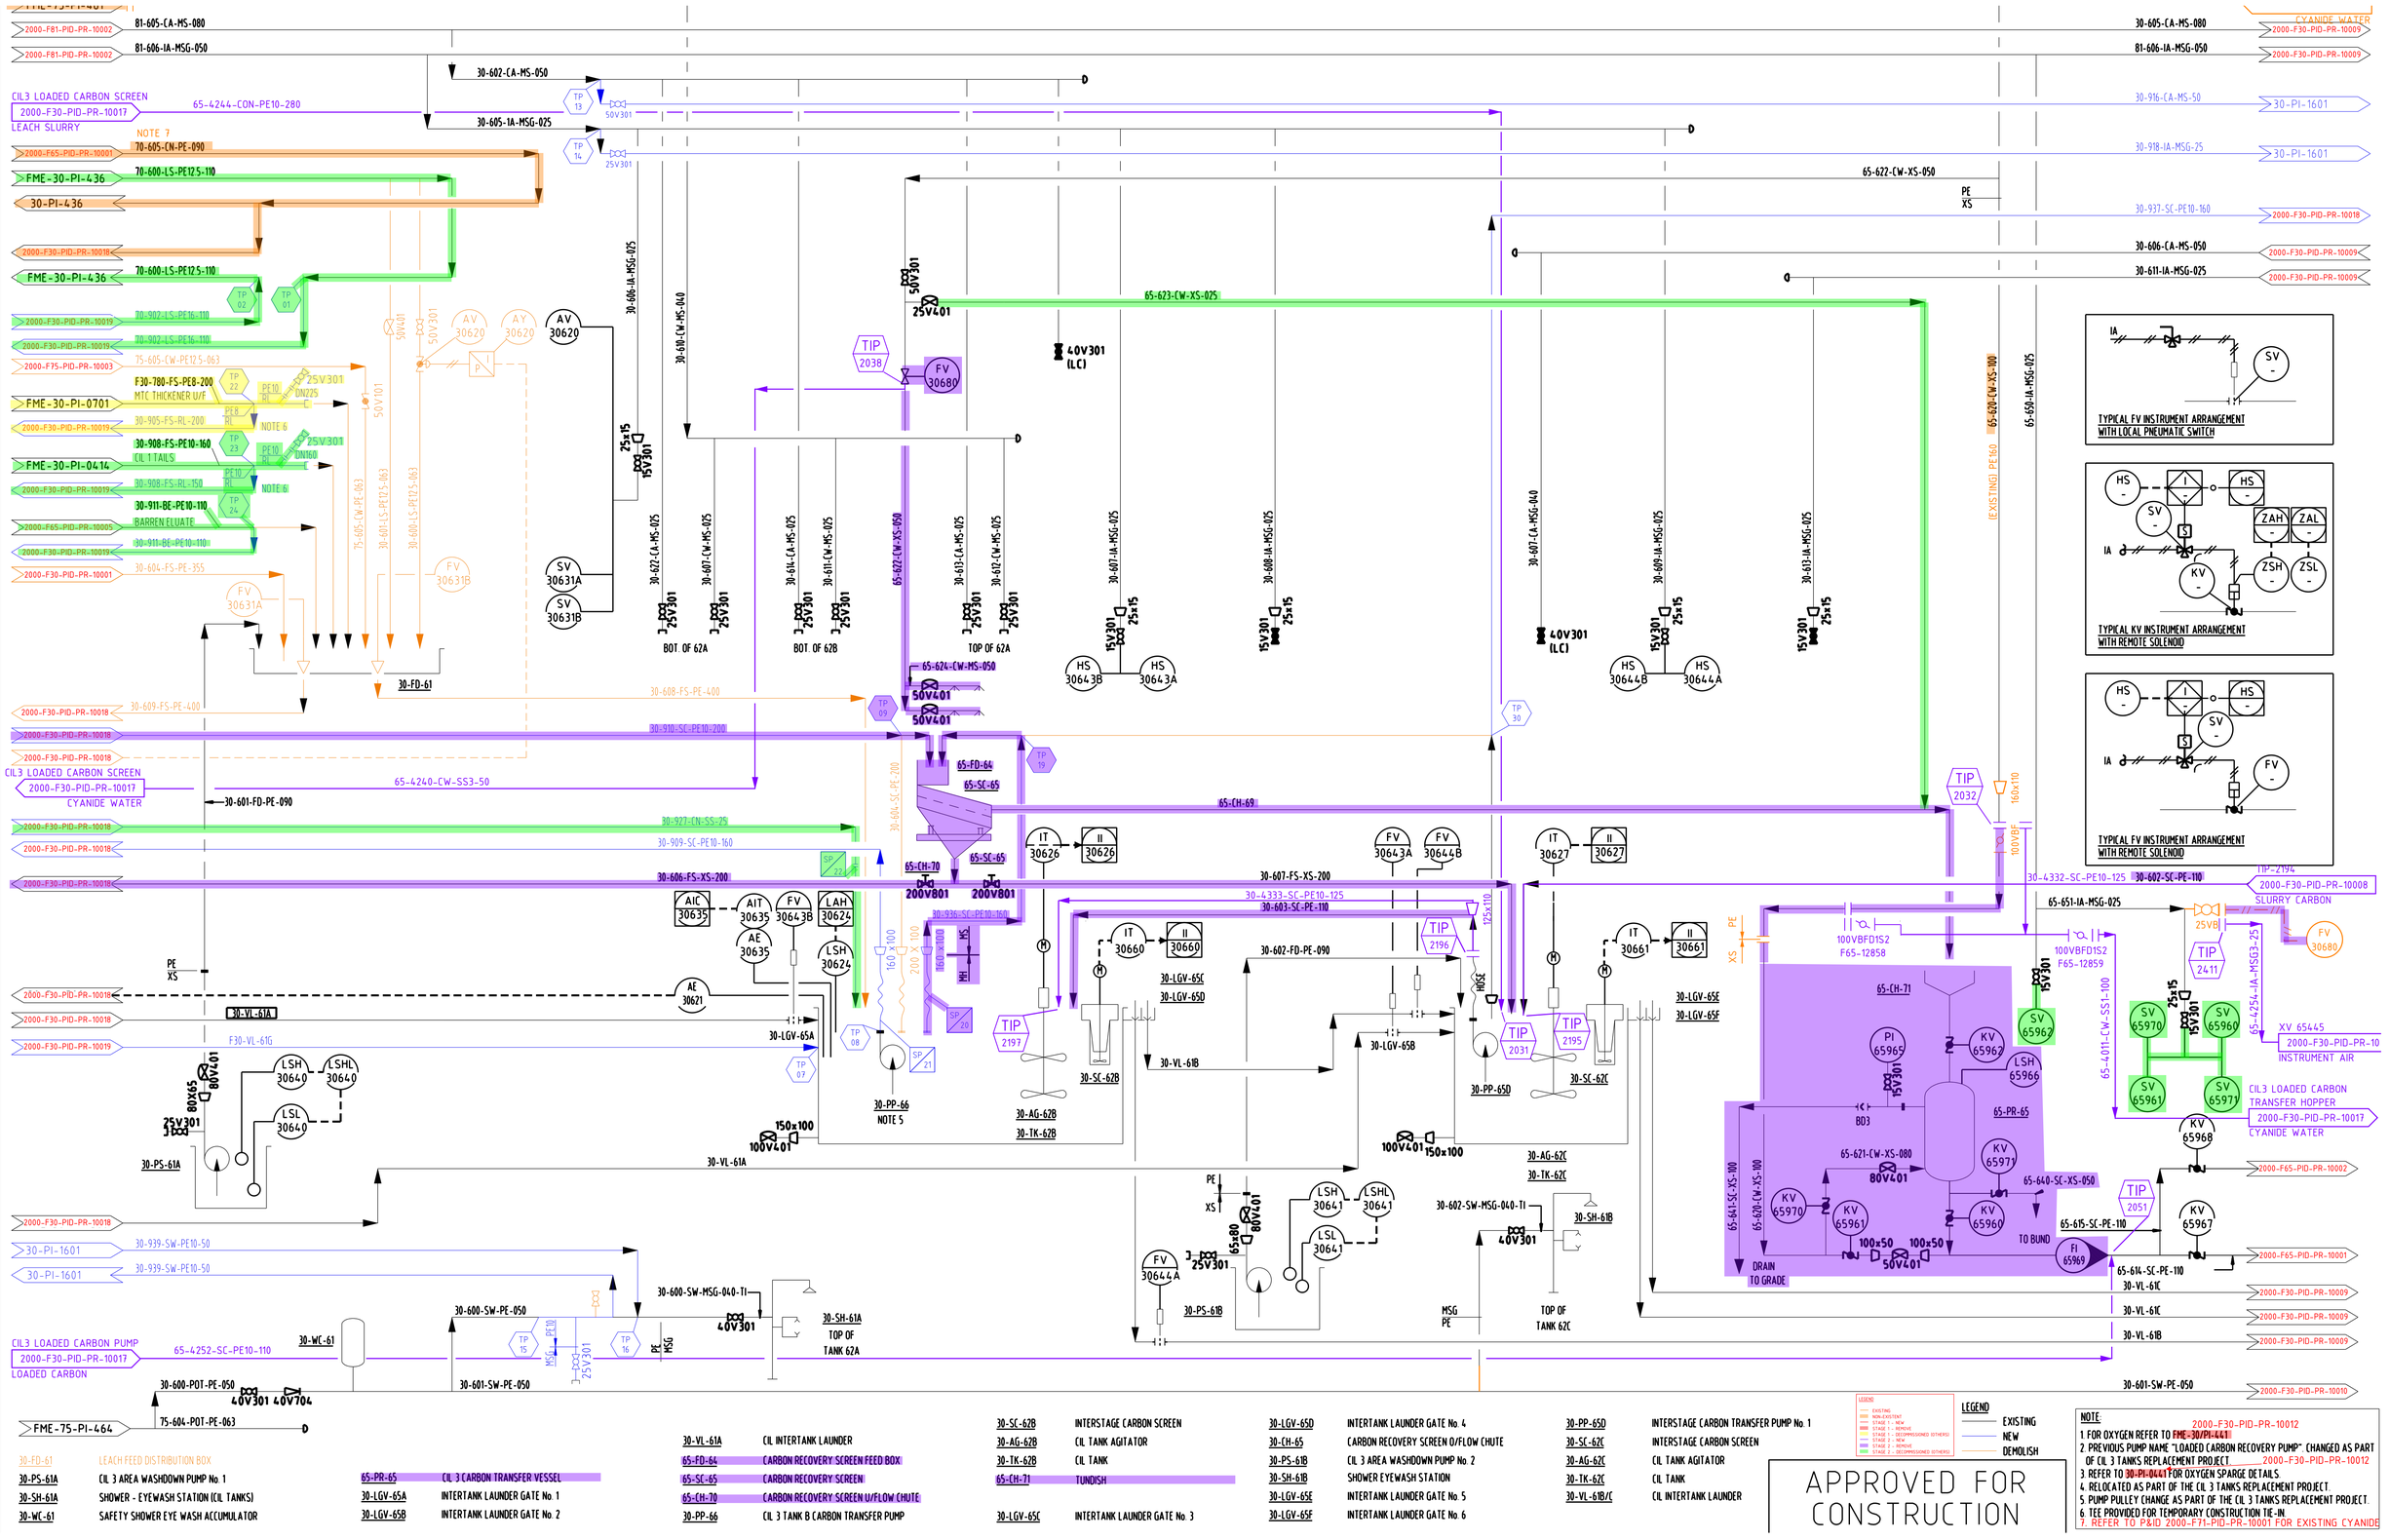


30-FD-61	LEACH FEED DISTRIBUTION BOX
30-PS-61A	CIL 3 AREA WASHDOWN PUMP No. 1
30-SH-61A	SHOWER - EYEWASH STATION (CIL TANKS)
30-WC-61	SAFETY SHOWER EYE WASH ACCUMULATOR

65-PR-65	CIL 3 CARBON TRANSFER VESSEL
30-LGV-65A	INTERTANK LAUNDER GATE No. 1
30-LGV-65B	INTERTANK LAUNDER GATE No. 2

30-VL-61A	CIL INTERTANK LAUNDER
65-FD-64	CARBON RECOVERY SCREEN FEED BOX
65-SC-65	CARBON RECOVERY SCREEN
65-CH-70	CARBON RECOVERY SCREEN U/FLOW CHUTE
30-PP-66	CIL 3 TANK B CARBON TRANSFER PUMP

30-SC-62B	INTERSTAGE CARBON SCREEN
30-AG-62B	CIL TANK AGITATOR
30-TK-62B	CIL TANK
65-CH-71	TUNDISH
30-LGV-65C	INTERTANK LAUNDER GATE No. 3

30-LGV-65D	INTERTANK LAUNDER GATE No. 4
30-CH-65	CARBON RECOVERY SCREEN D/FLOW CHUTE
30-PS-61B	CIL 3 AREA WASHDOWN PUMP No. 2
30-SH-61B	SHOWER EYEWASH STATION
30-LGV-65E	INTERTANK LAUNDER GATE No. 5
30-LGV-65F	INTERTANK LAUNDER GATE No. 6

30-PP-65D	INTERSTAGE CARBON TRANSFER PUMP No. 1
30-SC-62C	INTERSTAGE CARBON SCREEN
30-AG-62C	CIL TANK AGITATOR
30-TK-62C	CIL TANK
30-VL-61B/C	CIL INTERTANK LAUNDER

LEGEND
EXISTING
NEW
DEMOLISH

APPROVED FOR CONSTRUCTION

NOTE:
1. FOR OXYGEN REFER TO FME-30-PI-441 2000-F30-PID-PR-10012
2. PREVIOUS PUMP NAME "LOADED CARBON RECOVERY PUMP" CHANGED AS PART OF CIL 3 TANKS REPLACEMENT PROJECT. 2000-F30-PID-PR-10012
3. REFER TO 30-PI-0441 FOR OXYGEN SPARGE DETAILS.
4. RELOCATED AS PART OF THE CIL 3 TANKS REPLACEMENT PROJECT.
5. PUMP PULLEY CHANGE AS PART OF THE CIL 3 TANKS REPLACEMENT PROJECT.
6. TEE PROVIDED FOR TEMPORARY CONSTRUCTION TIE-IN
7. REFER TO P&ID 2000-F71-PID-PR-10001 FOR EXISTING CYANIDE