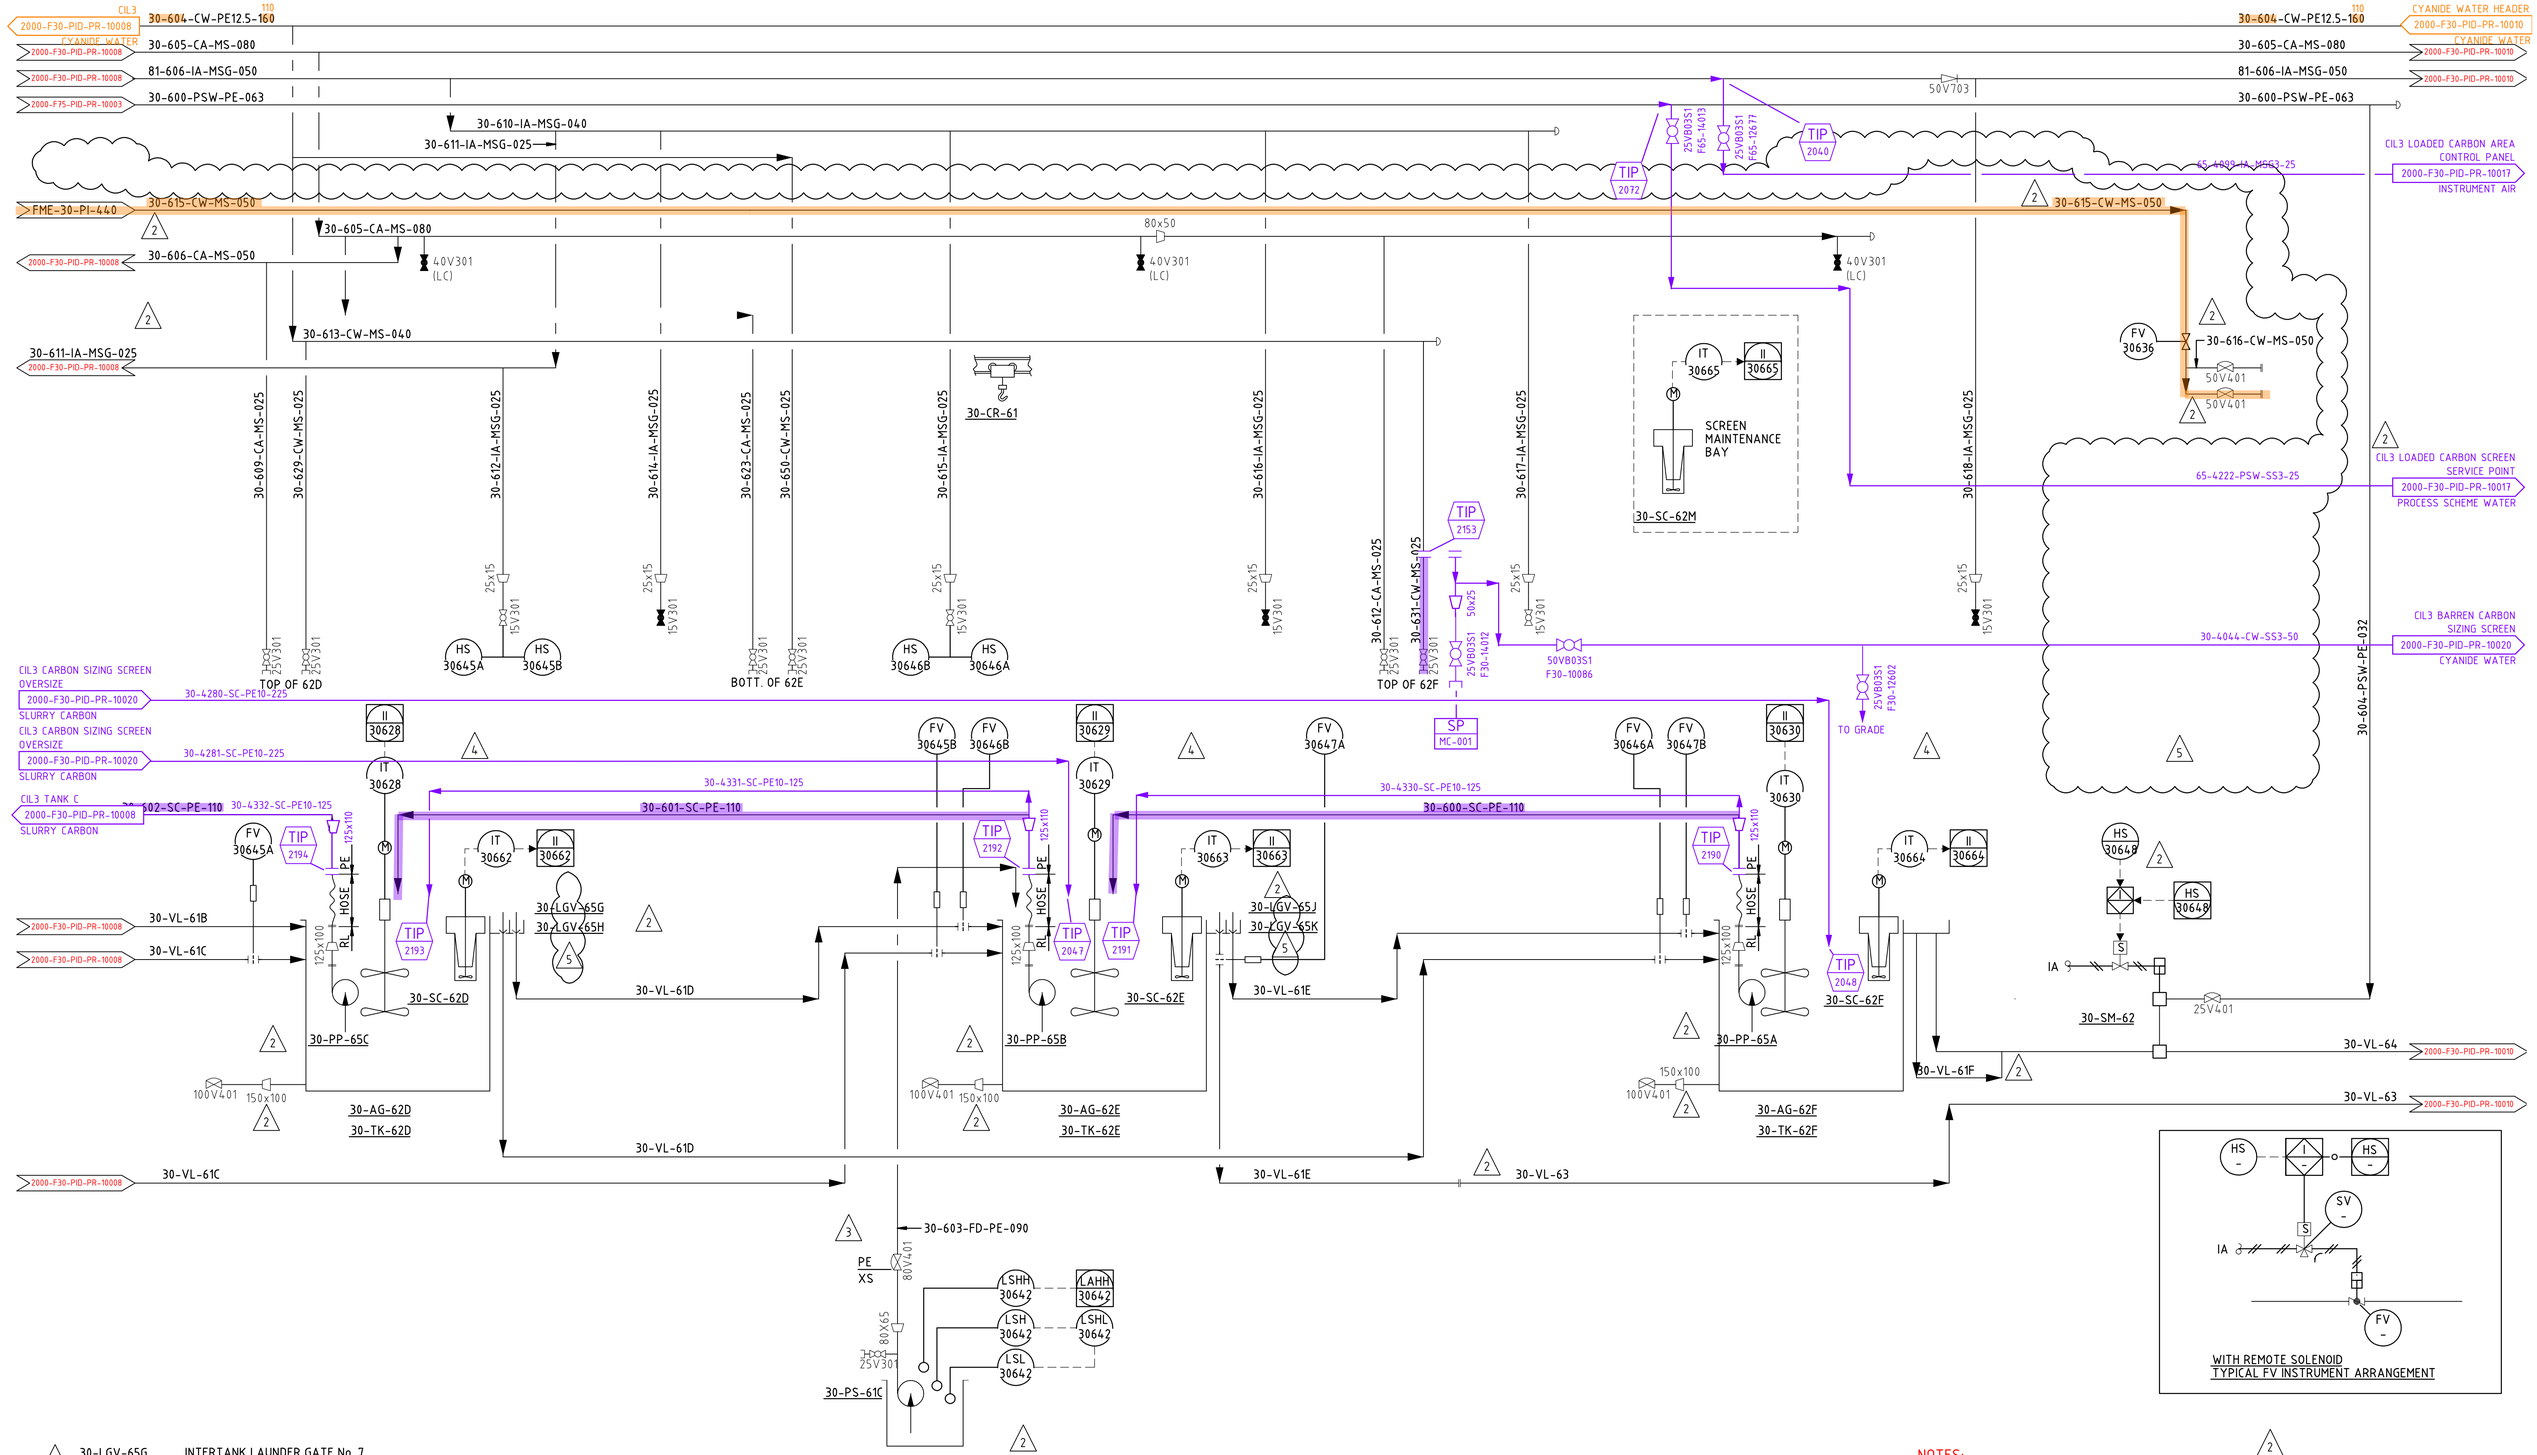


30-LGV-65G	INTERTANK LAUNDER GATE No. 7	
30-LGV-65H	INTERTANK LAUNDER GATE No. 8	
30-SC-62D	INTERSTAGE CARBON SCREEN	
30-PP-65B	INTERSTAGE CARBON TRANSFER PUMP No. 2	
30-AG-62D	CIL TANK AGITATOR	
30-TK-62D	CIL TANK	
30-CR-61	CIL 3 OVERHEAD GANTRY CRANE	
30-PS-61C	CIL 3 AREA WASHDOWN PUMP No. 3	

30-LGV-65J	INTERTANK LAUNDER GATE No. 9	
30-LGV-65K	INTERTANK LAUNDER GATE No. 10 - TO TAILS	
30-SC-62E	INTERSTAGE CARBON SCREEN	
30-PP-65C	INTERSTAGE CARBON TRANSFER PUMP No. 3	
30-VL-61D	CIL INTERTANK LAUNDER	
30-AG-62E	CIL TANK AGITATOR	
30-TK-62E	CIL TANK	

30-SM-62	SAMPLER	
30-SC-62F	INTERSTAGE CARBON SCREEN	
30-PP-65D	INTERSTAGE CARBON TRANSFER PUMP No. 4	
30-VL-61E/F	CIL INTERTANK LAUNDER	
30-AG-62F	CIL TANK AGITATOR	
30-TK-62F	CIL TANK	
30-SC-62G	SPARE INTERSTAGE SCREEN	

30-VL-63/64 CIL TAILINGS LAUNDER No. 2 & 3

NOTES:

1. FOR OXYGEN REFER TO 2000-F30-PID-10012

LEGEND

- STAGE 1 - NEW
- STAGE 1 - REMOVE
- STAGE 1 - DECOMMISSIONED (OTHERS)
- STAGE 2 - NEW
- STAGE 2 - REMOVE
- STAGE 2 - DECOMMISSIONED (OTHERS)