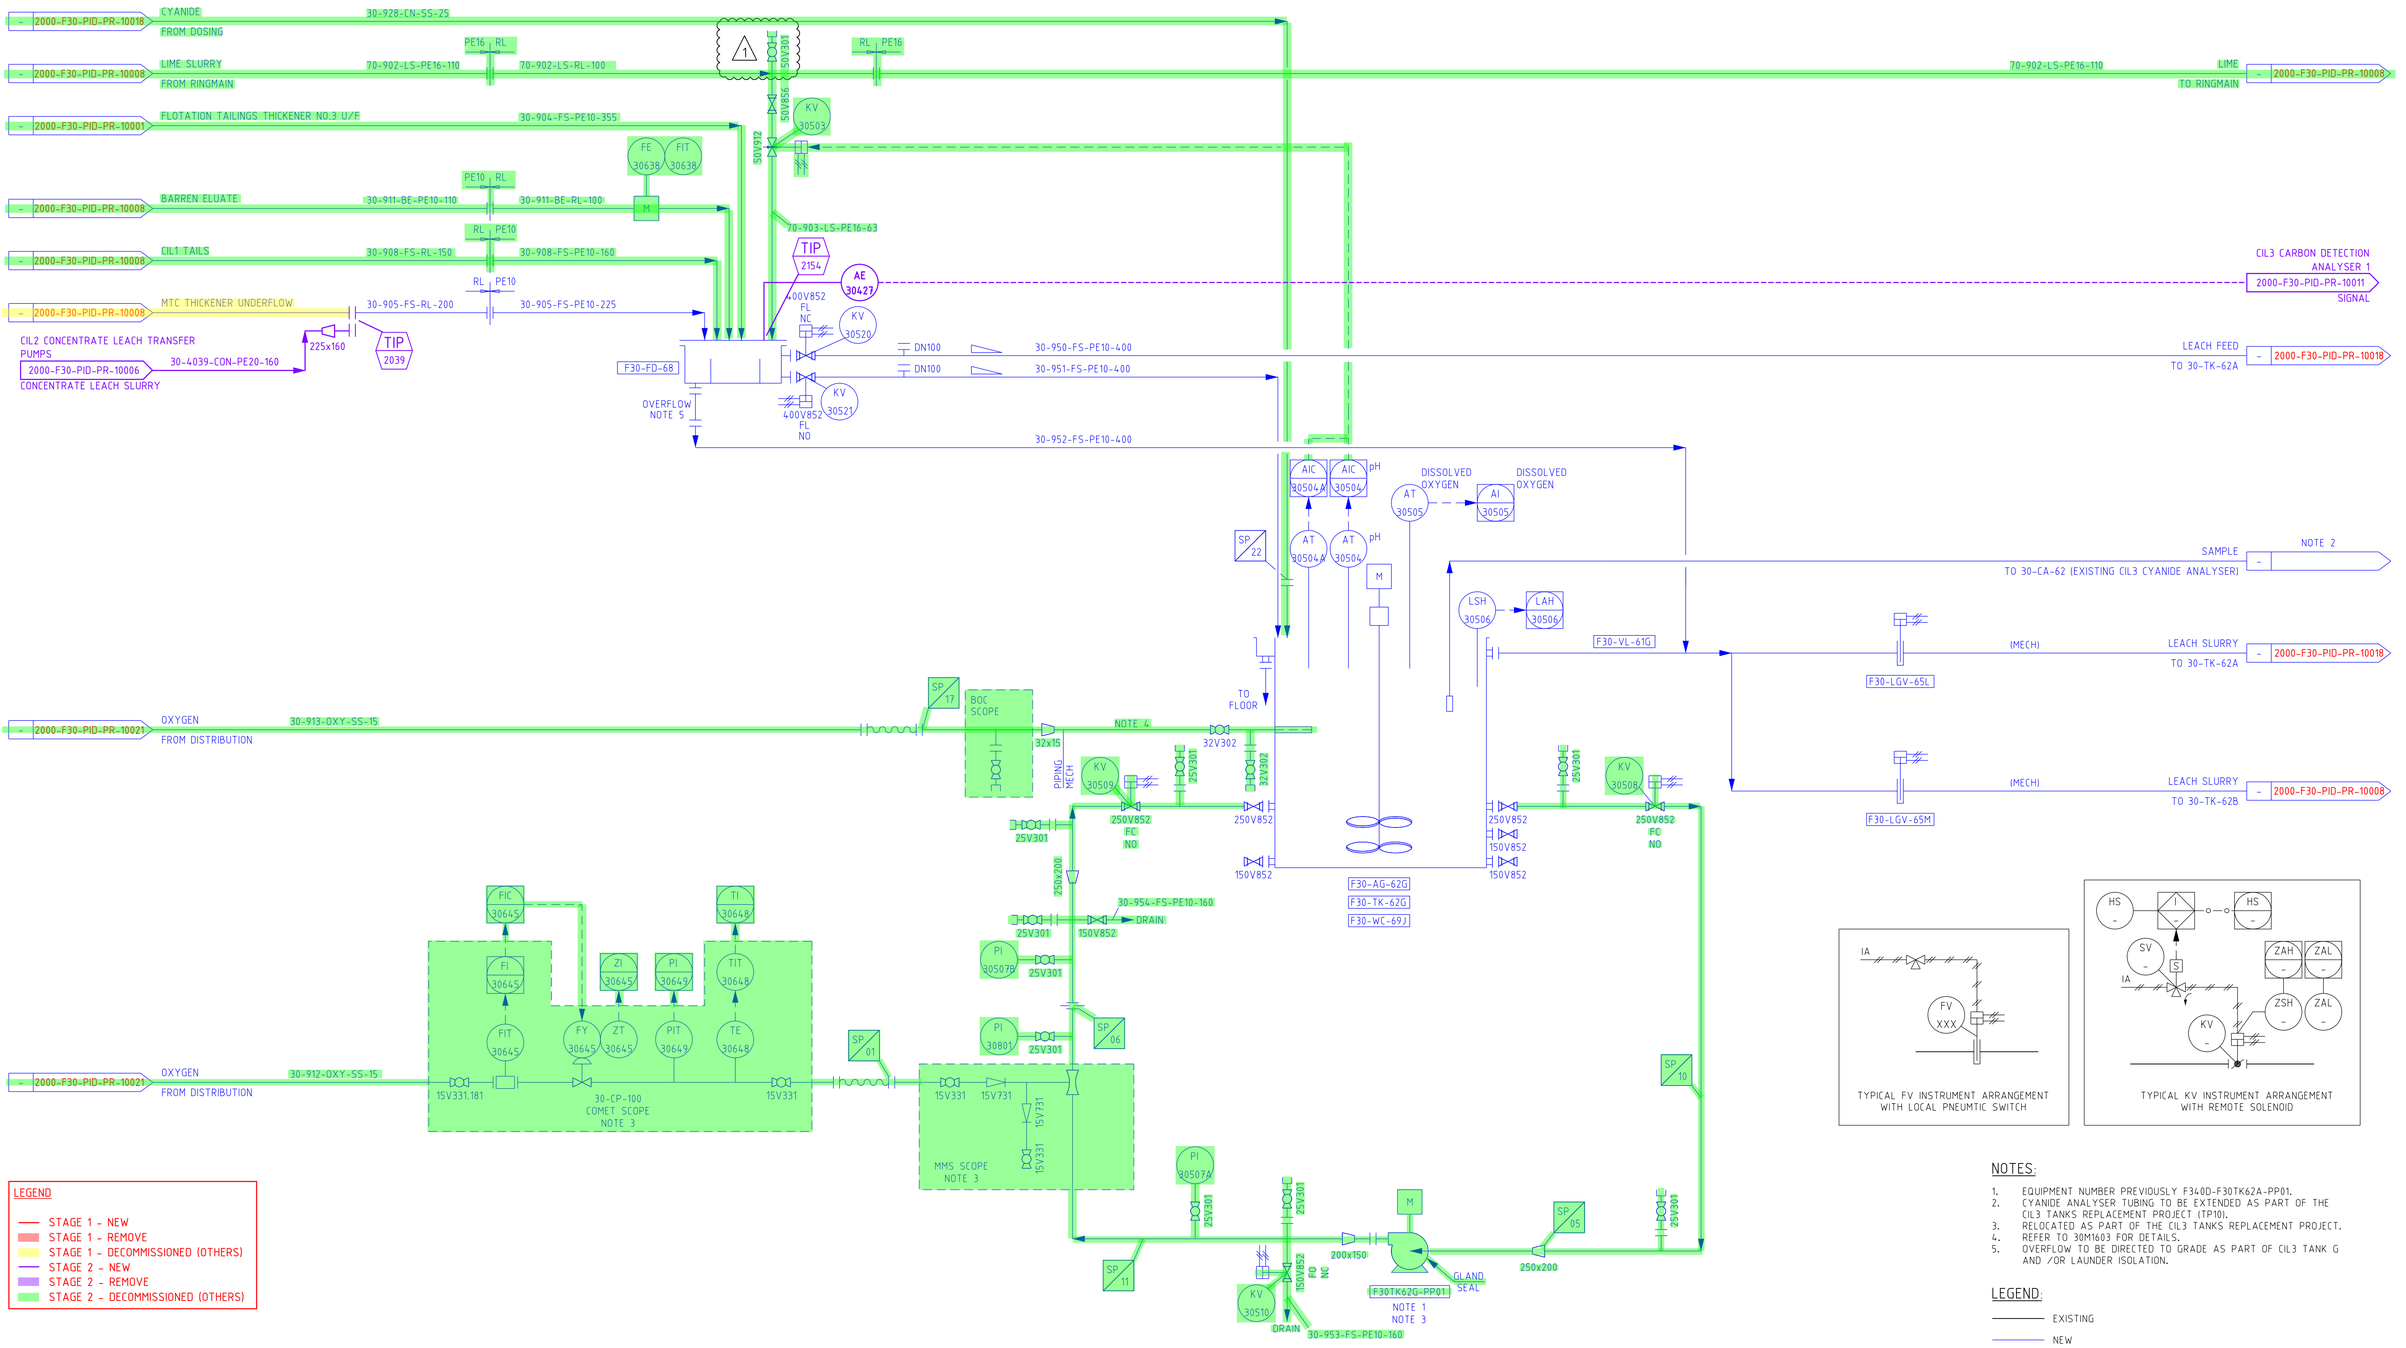


NOTES:

1. EQUIPMENT NUMBER PREVIOUSLY F340D-F30TK62A-PP01.
2. CYANIDE ANALYSER TUBING TO BE EXTENDED AS PART OF THE CIL3 TANKS REPLACEMENT PROJECT (TP10).
3. RELOCATED AS PART OF THE CIL3 TANKS REPLACEMENT PROJECT.
4. REFER TO 30M1603 FOR DETAILS.
5. OVERFLOW TO BE DIRECTED TO GRADE AS PART OF CIL3 TANK G AND /OR LAUNDER ISOLATION.

LEGEND:

EXISTING
NEW
DEMOLISH

CIL3 TANK G AGITATOR	CIL3 TANK A/G FEED BOX	CIL3 TANK G INTERTANK ISOLATION GATE A	CIL3 TANK G INTERTANK ISOLATION GATE B	CIL3 OXYGEN INJECTION PUMP	CIL3 TANK G	CIL3 TANK G DISCHARGE LAUNDER	CIL3 TANK G OXYGEN INJECTION SPARGE
F30-AG-62G	F30-FD-68	F30-LGV-65L	F30-LGV-65M	F30TK62G-PP01	F30-TK-62G	F30-VL-61G	F30-WC-69J

APPROVED FOR CONSTRUCTION