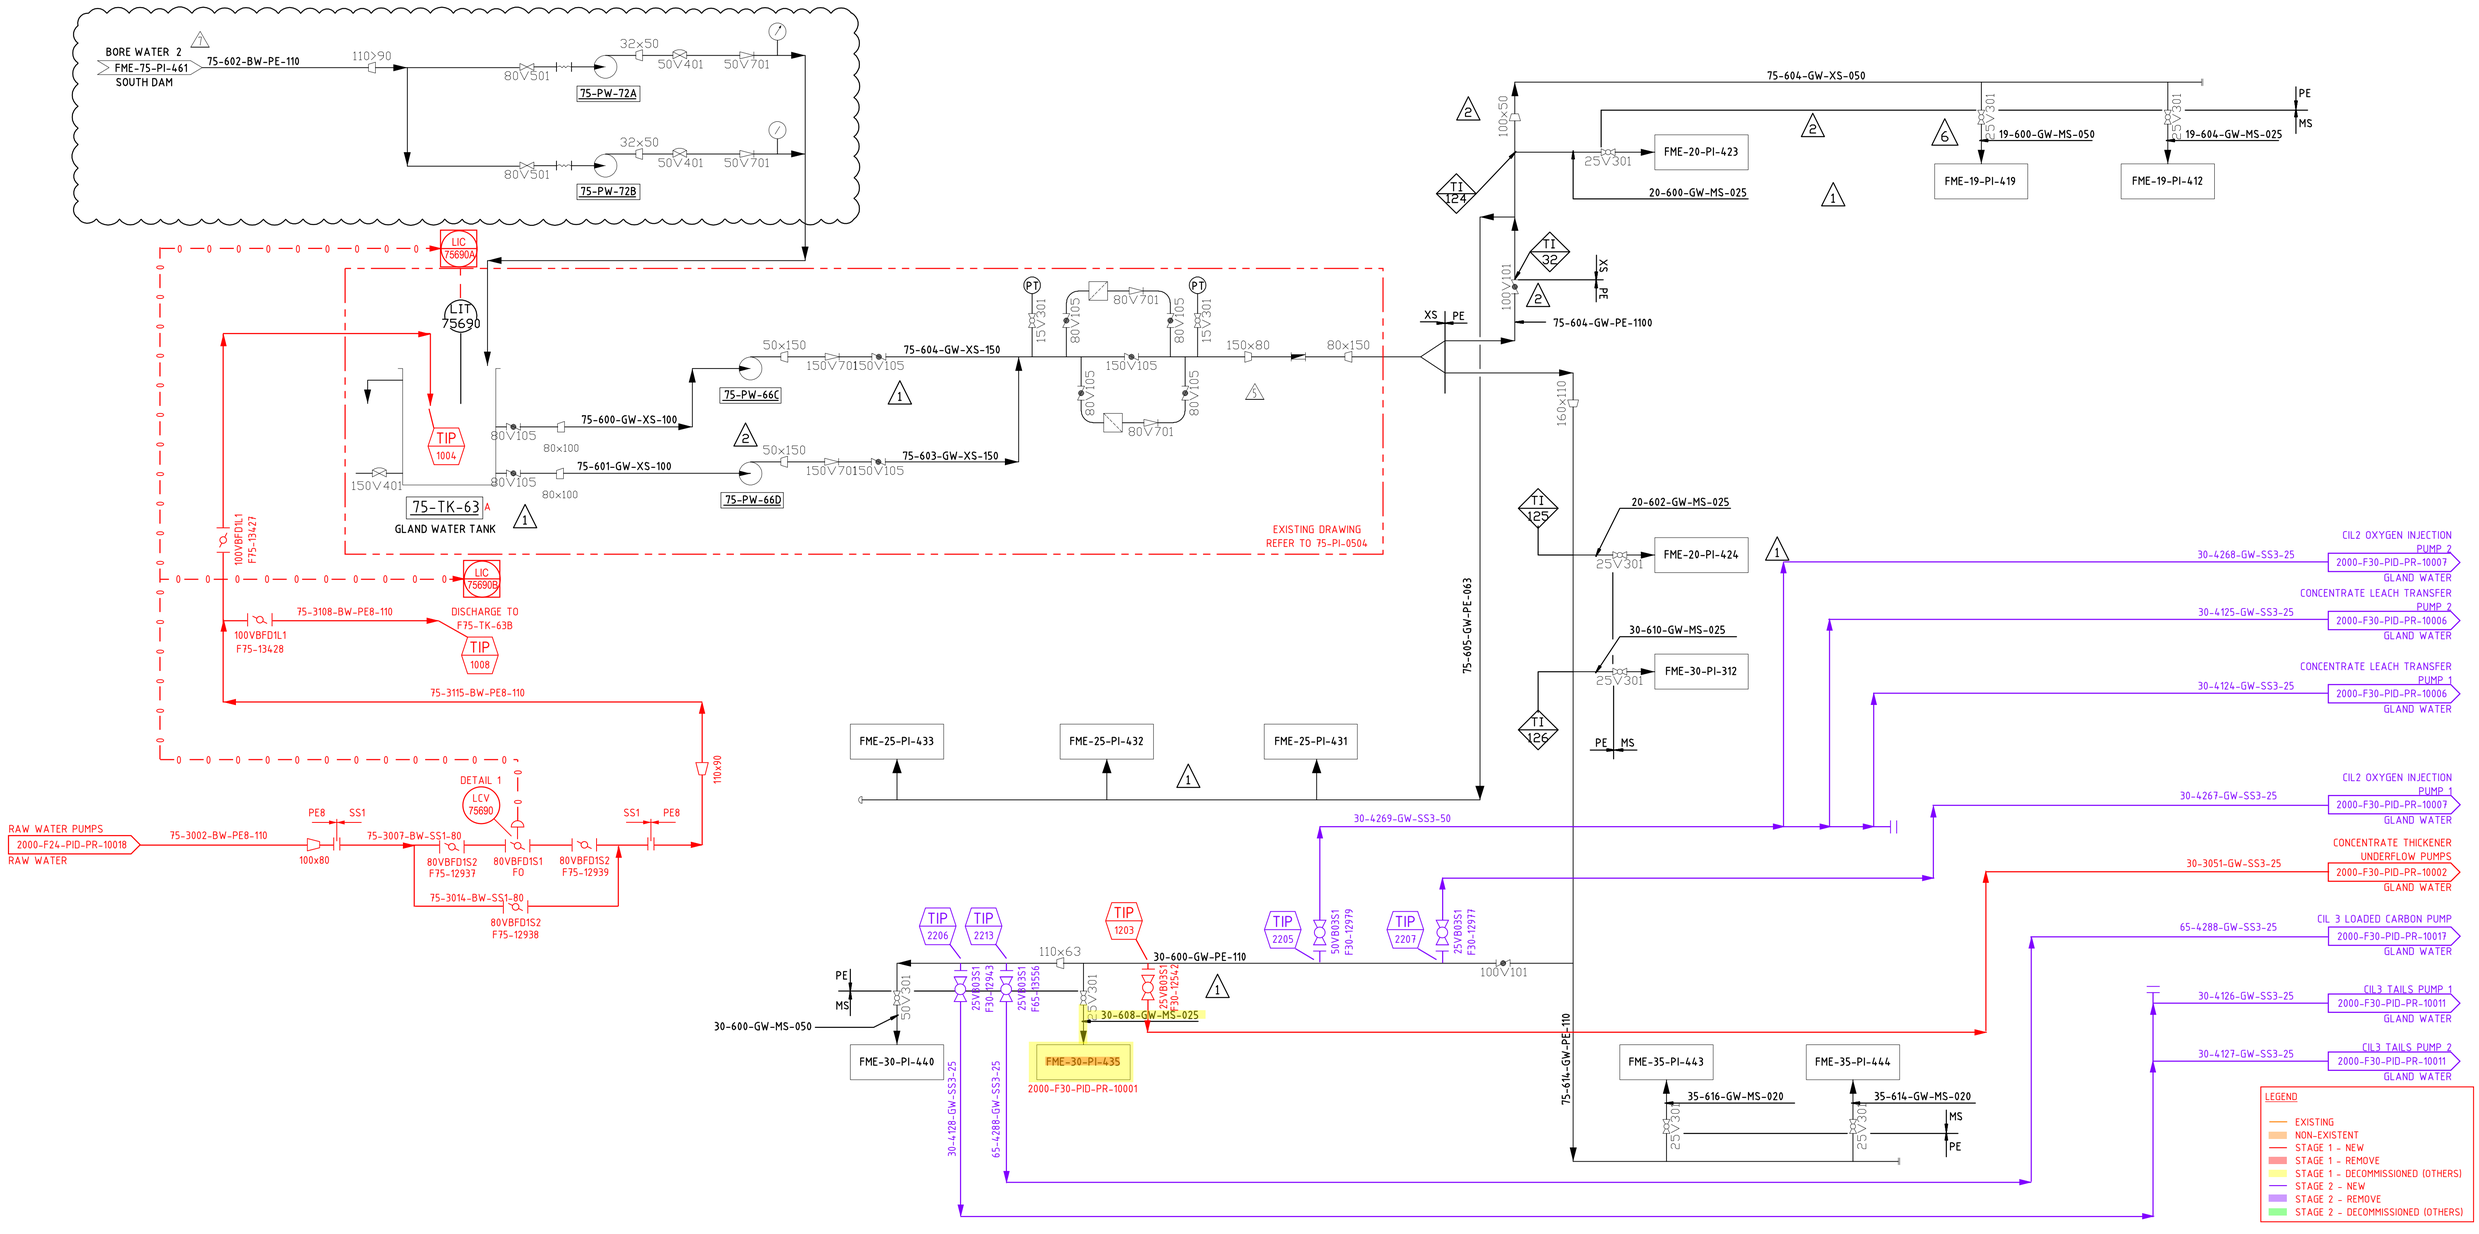


75-PW-72 A/B GLANDWATER PUMP

75-TK-63 GLAND WATER STORAGE TANK

75-PW-66 C/D GLAND WATER PUMP No. 1/2

NOTES:

1. THIS DRAWING TO BE READ IN CONJUNCTION WITH P&ID 75-PI-0504
2. PUMPS REQUIRING GLAND WATER THAT ARE WITHIN BROWNFIELDS SCOPE ARE TO TIE IN TO THE EXISTING GLAND WATER CIRCUIT. REFER TO 2000-F2[redacted] AND 2000-F24-PID-PR-10035 FOR BROWNFIELDS [redacted] DETAIL

NOTE GLAND WATER POLYETHYLENE PIPES TO BE PE 80 TYPE B PN10