LEGEND:

- EXISTING
- NEW
- FUTURE
- DECOMMISSIONED

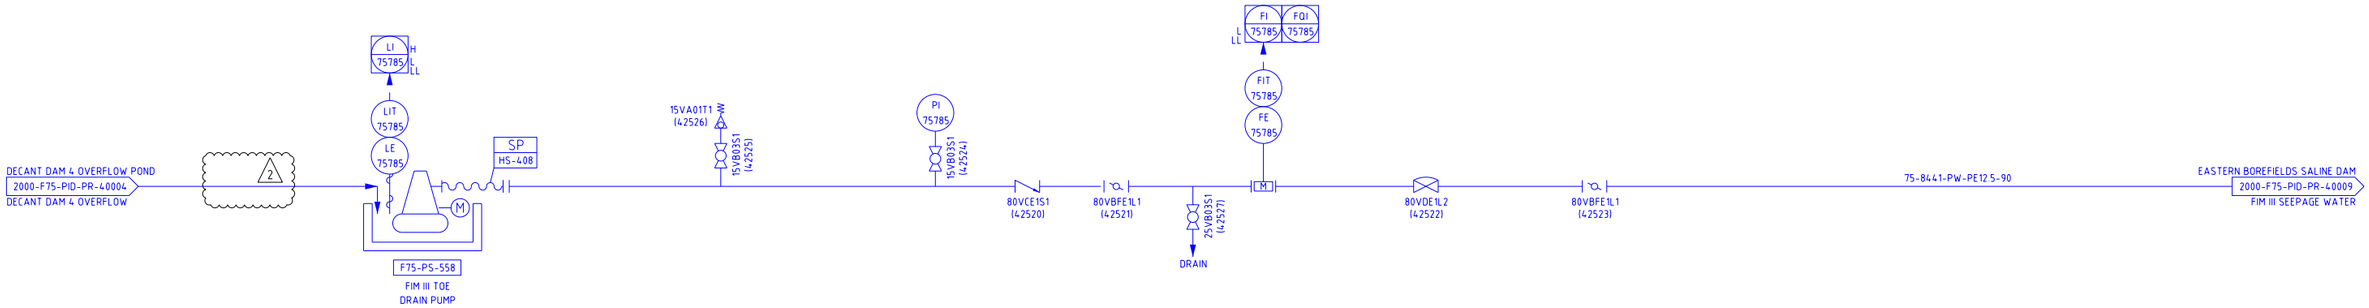

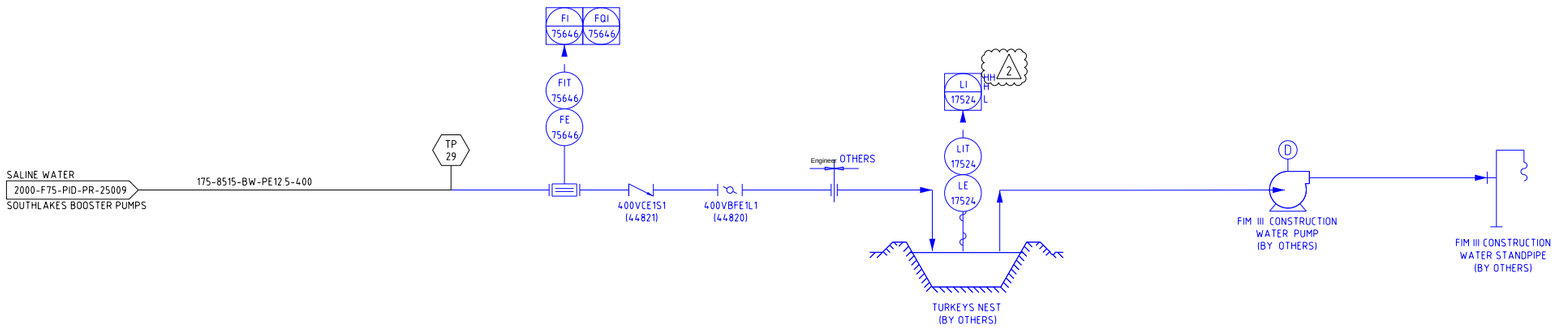

APPROVED FOR CONSTRUCTION