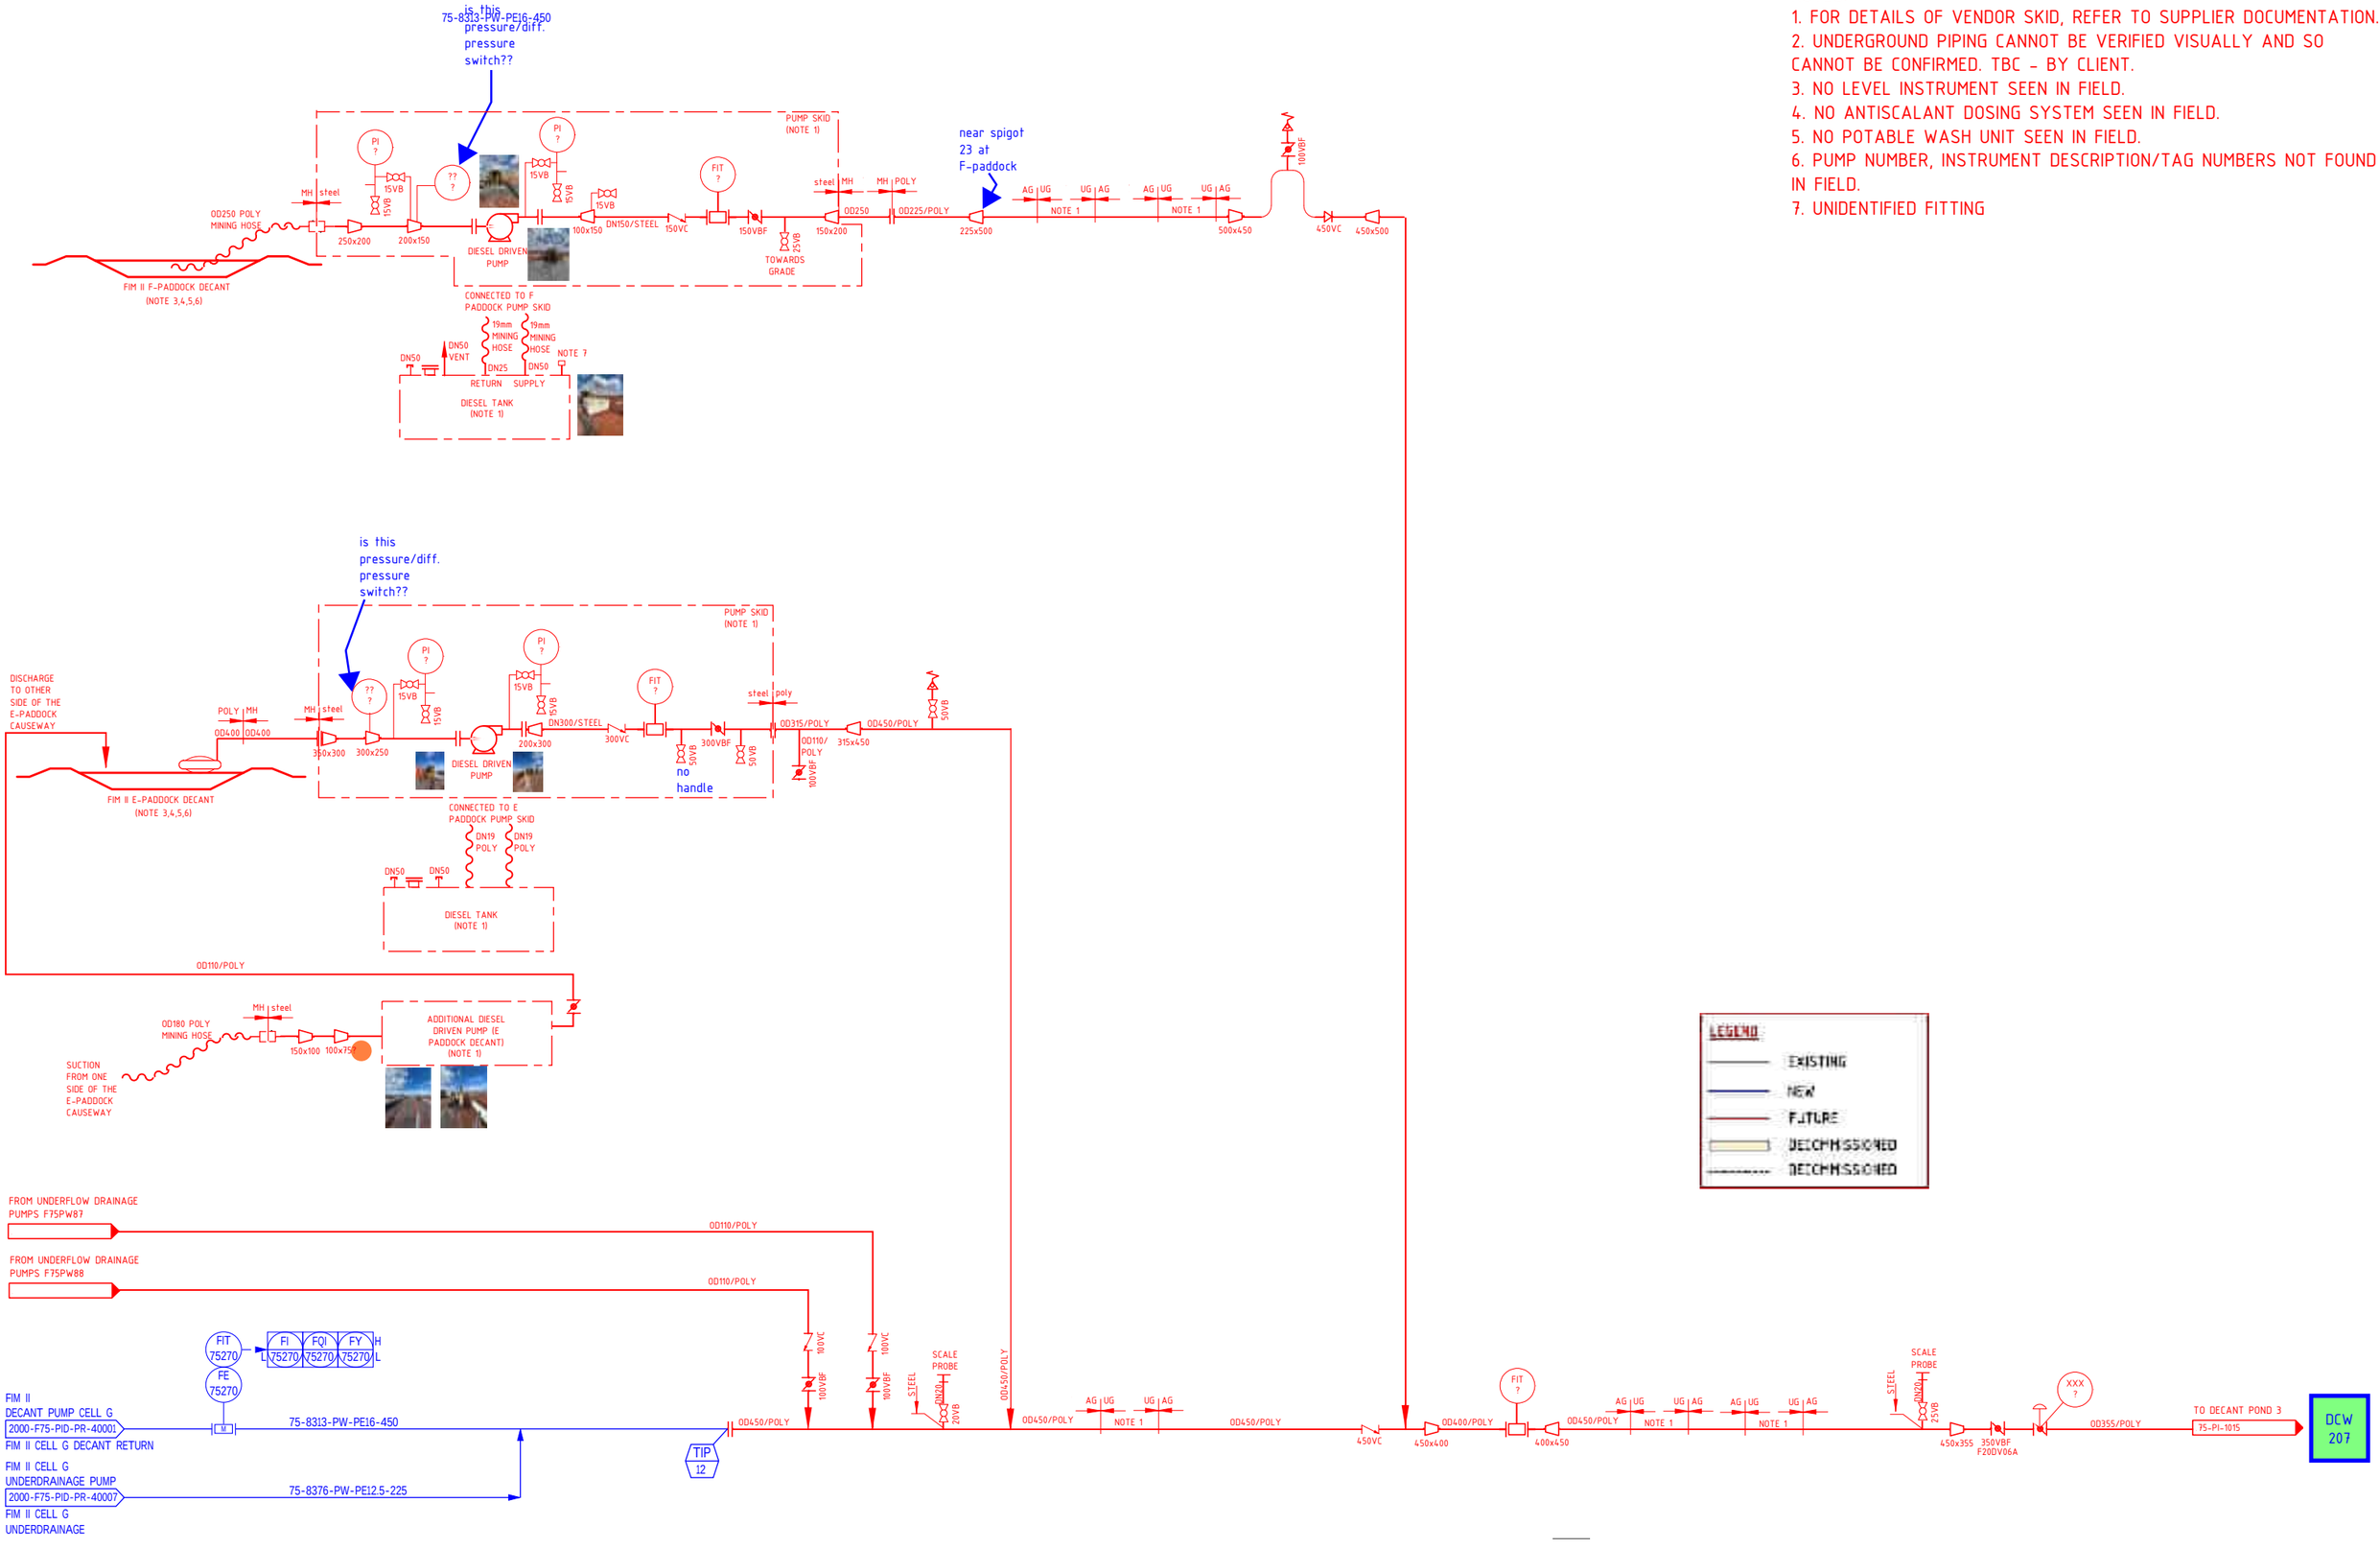


NOTES:

1. FOR DETAILS OF VENDOR SKID, REFER TO SUPPLIER DOCUMENTATION.
2. UNDERGROUND PIPING CANNOT BE VERIFIED VISUALLY AND SO CANNOT BE CONFIRMED. TBC - BY CLIENT.
3. NO LEVEL INSTRUMENT SEEN IN FIELD.
4. NO ANTISCALANT DOSING SYSTEM SEEN IN FIELD.
5. NO POTABLE WASH UNIT SEEN IN FIELD.
6. PUMP NUMBER, INSTRUMENT DESCRIPTION/TAG NUMBERS NOT FOUND IN FIELD.
7. UNIDENTIFIED FITTING