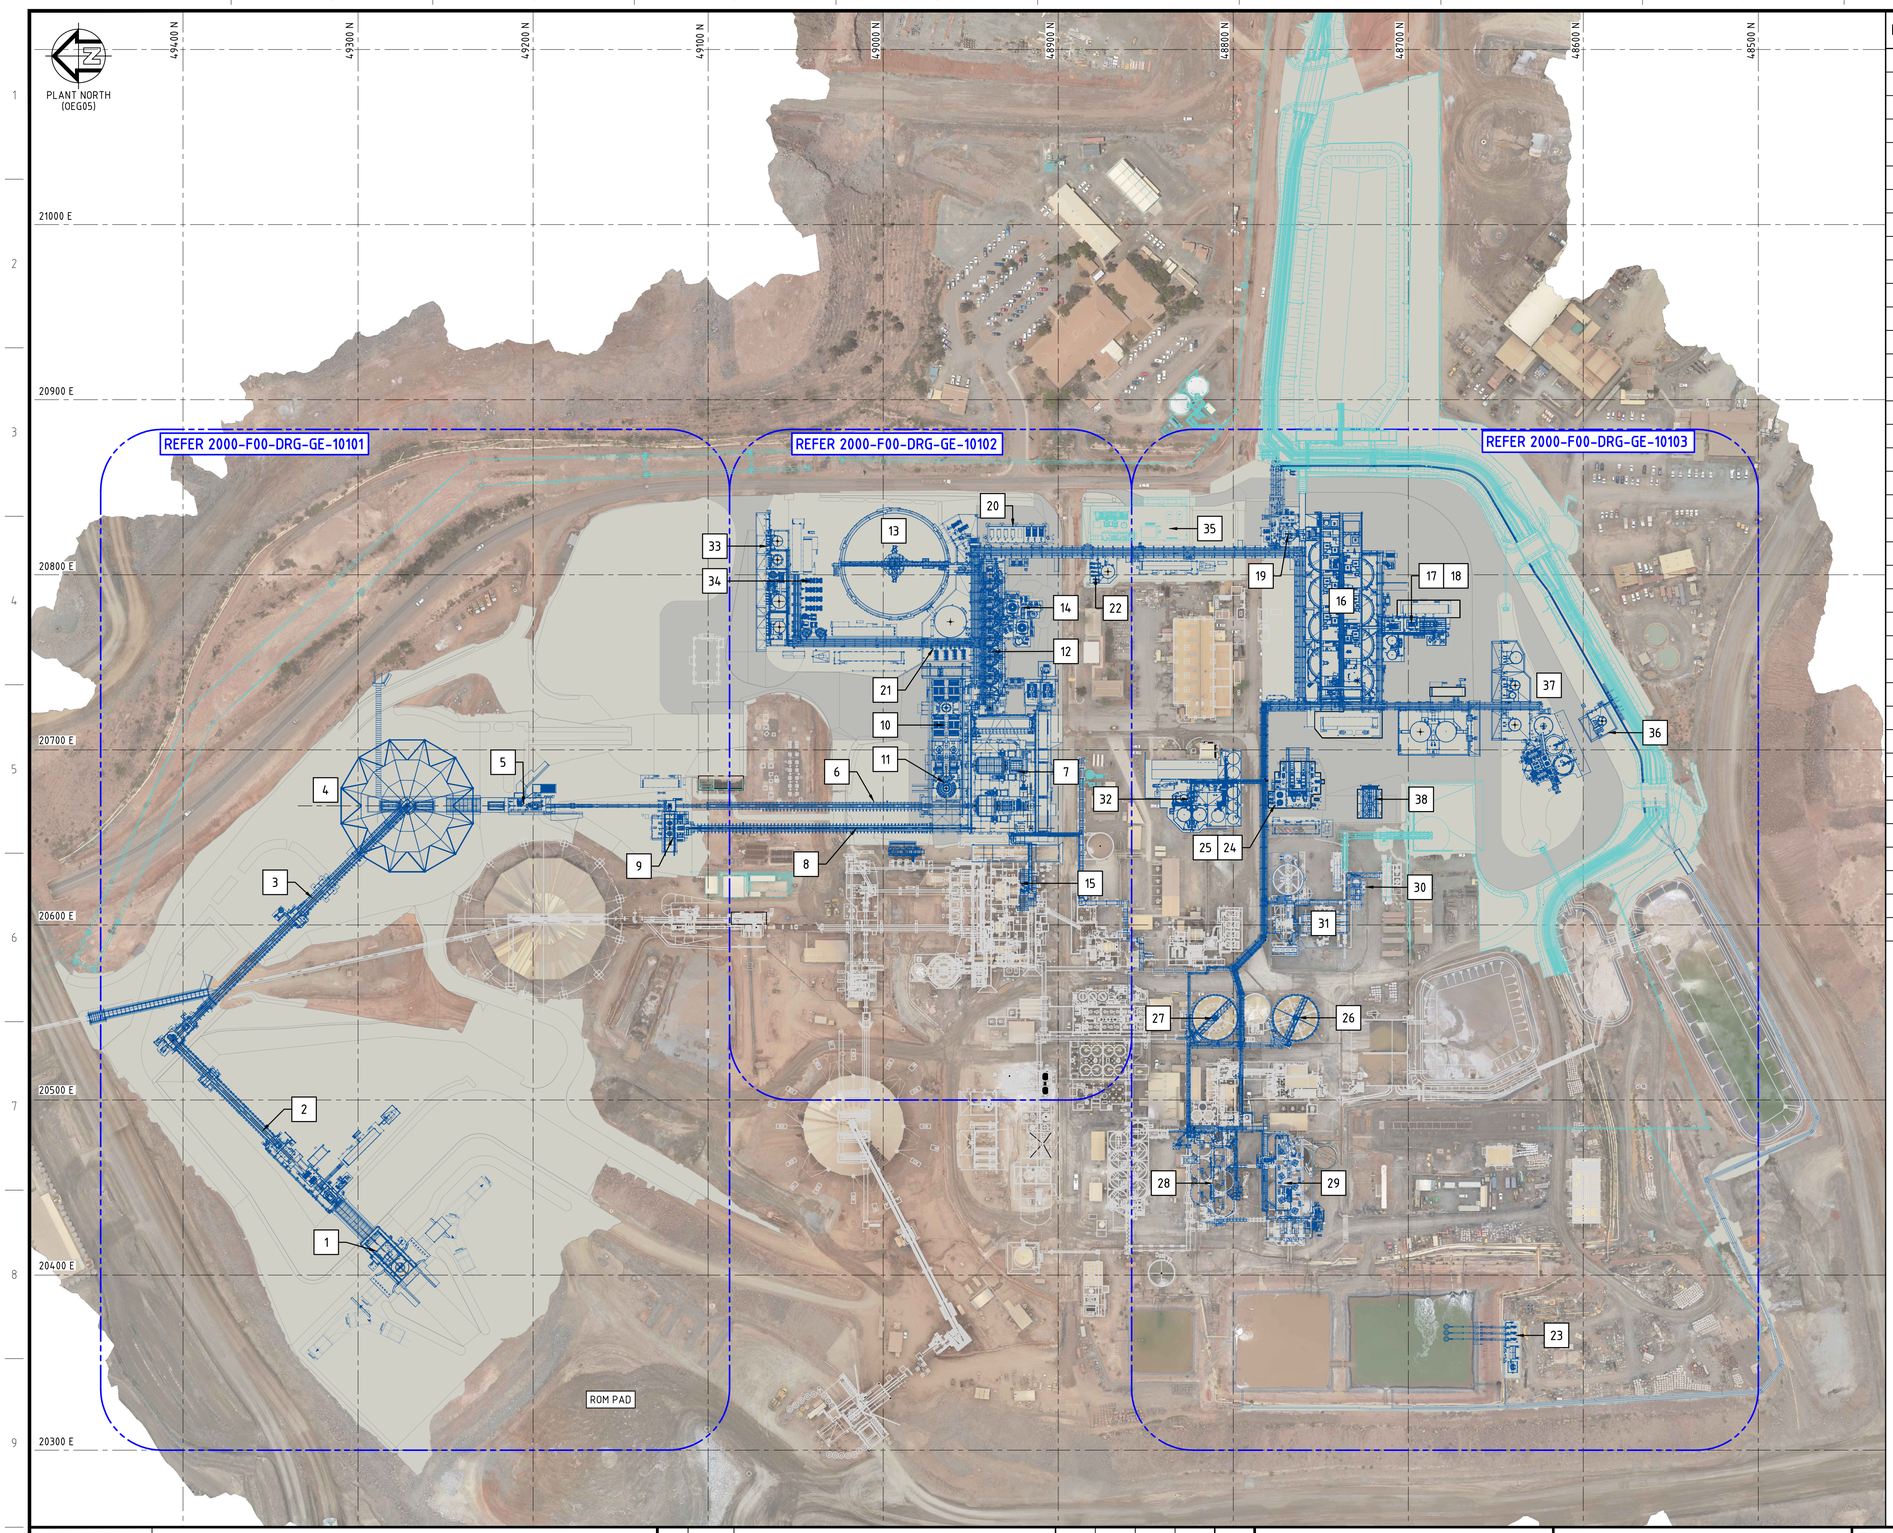


ITEM	AREA	DESCRIPTION	DRAWING No.
1	F12	PRIMARY CRUSHING	2000-F12-DRG-ME-10200
2	F12	CV-401 - PRIMARY CRUSHING DISCHARGE CONVEYOR	2000-F12-DRG-ME-10405
3	F12	CV-402 - STOCKPILE FEED CONVEYOR	2000-F12-DRG-ME-10455
4	F12	COARSE ORE STOCKPILE	2000-F12-DRG-ST-10300
5	F13	STOCKPILE RECLAIM	2000-F13-DRG-ME-10200
6	F13	CV-403 - SAG MILL FEED CONVEYOR	2000-F13-DRG-ME-10605
7	F13	MILLING AND CLASSIFICATION	2000-F13-DRG-ME-10300
8	F13	CV-405 PEBBLE CRUSHING FEED CONVEYOR 2	2000-F13-DRG-ME-10655
9	F13	PEBBLE CRUSHING	2000-F13-DRG-ME-10400
10	F13	TRASH SCREENING	2000-F13-DRG-ME-10300
11	F14	GRAVITY CIRCUIT AND INTENSIVE LEACHING	2000-F13-DRG-ME-10300
12	F16	ROUGHER AND SCAVENGER FLOTATION	2000-F16-DRG-ME-10200
13	F17	FLOTATION TAILINGS THICKENING	2000-F17-DRG-ME-10200
14	F18	CLEANER AND CLEANER SCAVENGER FLOTATION	2000-F18-DRG-ME-10200
15	F19	EXISTING MILLING A - FIMISTON SAG	2000-F19-DRG-ME-10005
16	F21	FLOTATION TAILINGS CIL 4 (STAGE 2)	2000-F21-DRG-ME-10200
17	F22	CIL4 - CARBON TREATMENT (STAGE 2)	2000-F22-DRG-ME-10200
18	F22	CIL4 -ELUTION (STAGE 2)	2000-F22-DRG-ME-10200
19	F23	FINAL TAILINGS HANDLING AND STORAGE	2000-F23-DRG-ME-10200
20	F24	AIR AND WATER SERVICES - AIR COMPRESSORS	2000-F24-DRG-ME-10600
21	F24	AIR AND WATER SERVICES - PROCESS WATER	2000-F24-DRG-ME-10200
22	F24	AIR AND WATER SERVICES - RAW WATER	2000-F24-DRG-ME-10400
23	F75	AIR AND WATER SERVICES - SALINE WATER	2000-F75-DRG-ME-10200
24	F28	ULTRA FINE GRINDING 2	2000-F28-DRG-ME-10200
25	F28	ULTRA FINE GRINDING 3 (STAGE 2)	2000-F28-DRG-ME-10200
26	F30	CONCENTRATE THICKENING	2000-F30-DRG-ME-10400
27	F30	CONCENTRATE PRE-LEACH THICKENING	2000-F30-DRG-ME-10200
28	F30	CIL 2 - EXISTING	2000-F30-DRG-ME-10300
29	F30	CIL 3 - EXISTING	2000-F30-DRG-ME-10325
30	F34	ULTRA FINE GRINDING 1 - EXISTING	2000-F34-DRG-ME-10200
31	F35	CONCENTRATE HANDLING AND FILTRATION - EXISTING	2000-F35-DRG-ME-10250
32	F66	ELECTROWINNING AND GOLDROOM	2000-F66-DRG-ME-10100
33	F72	REAGENTS - FROTHER, FLOCCULENT, COPPER SULPHATE, PAX	2000-F72-DRG-ME-10100
34	F24	AIR AND WATER SERVICES - COOLING WATER	2000-F24-DRG-ME-10800
35	F72	REAGENTS - OXYGEN PLANT	2000-S021-B02-20001
36	F72	REAGENTS - HYDROGEN PEROXIDE	2000-F72-DRG-ME-10120
37	F72	REAGENTS - LIME, CYANIDE, CAUSTIC, LEAD NITRATE, HYDROCHLORIC ACID	2000-F72-DRG-ME-10120
38	F72	REAGENTS - GRINDING MEDIA AND ANTI-SCALANT STORAGE	2000-F72-DRG-ME-10800

NOTES:

1. THIS DRAWING SHALL BE READ IN CONJUNCTION WITH 2000-F00-DRG-GE-20001 (BY OTHERS)
2. FOR SETOUT POINT DESCRIPTIONS AND COORDINATES REFER 2000-F00-DRG-CC-10100
3. FOR COMBINED BURIED SERVICES AND FIRE HYDRANT LOCATIONS REFER 2000-F00-DRG-GE-10300 AND 2000-F00-DRG-GE-10301
4. PRIMERO SCOPE OF WORKS DENOTED THUS:
5. WORKS BY OTHERS (ENABLING WORKS) DENOTED THUS:

DRG No.	REFERENCES
2000-F00-DRG-GE-20001	FIMISTON PROCESS PLANT - OVERALL PLANT LAYOUT - PLAN (BY OTHERS)
2000-F00-DRG-ST-10400	GENERAL FIMISTON SITE - PIPERACKS - OVERALL STRUCTURAL ARRANGEMENT
2000-F00-DRG-GE-10301	GENERAL FIMISTON SITE - BURIED SERVICES - KEY PLAN
2000-F00-DRG-GE-10300	GENERAL FIMISTON SITE - BURIED SERVICES - FIRE HYDRANT LOCATION PLAN
2000-F00-DRG-CC-10100	GENERAL FIMISTON SITE - OVERALL PLANT - CONCRETE ARRANGEMENT
2000-F00-DRG-GE-10103	GENERAL FIMISTON SITE - GENERAL ARRANGEMENT - PLAN SHEET 3
2000-F00-DRG-GE-10102	GENERAL FIMISTON SITE - GENERAL ARRANGEMENT - PLAN SHEET 2
2000-F00-DRG-GE-10101	GENERAL FIMISTON SITE - GENERAL ARRANGEMENT - PLAN SHEET 1

REV	DATE	DESCRIPTION	DRAW	CHECK	DESIGN	TECH APP	PROJ APP
0	14OCT25	APPROVED FOR CONSTRUCTION	[redacted]				

NORTHERN STAR RESOURCES LIMITED

PRIMERO
primero.com.au | DESIGN | CONSTRUCT | OPERATE

PRIMERO PROJECT NUMBER: 23517

INFORMATION AND REPRESENTATIONS ON THIS DRAWING ARE THE INTELLECTUAL PROPERTY OF PRIMERO UNLESS SPECIFICALLY IDENTIFIED OTHERWISE. ALL RIGHTS INCLUDING USE RESERVED

PROJECT: NORTHERN STAR RESOURCES LTD
KCGM GROWTH PROJECT

TITLE: GENERAL FIMISTON SITE
GENERAL ARRANGEMENT
LAYOUT PLAN

SHEET	SCALE	DRG No.	REVISION
A1	1:1750	2000-F00-DRG-GE-10100	0

O:\CAD PROJECTS\235 NORTHERN STAR RESOURCES LTD\235177 KCGM GROWTH PROJECT\03 DELIVERABLES\GE\2000-F00-DRG-GE-10100.DWG 14OCT25 11:47AM JULIAN KNOX