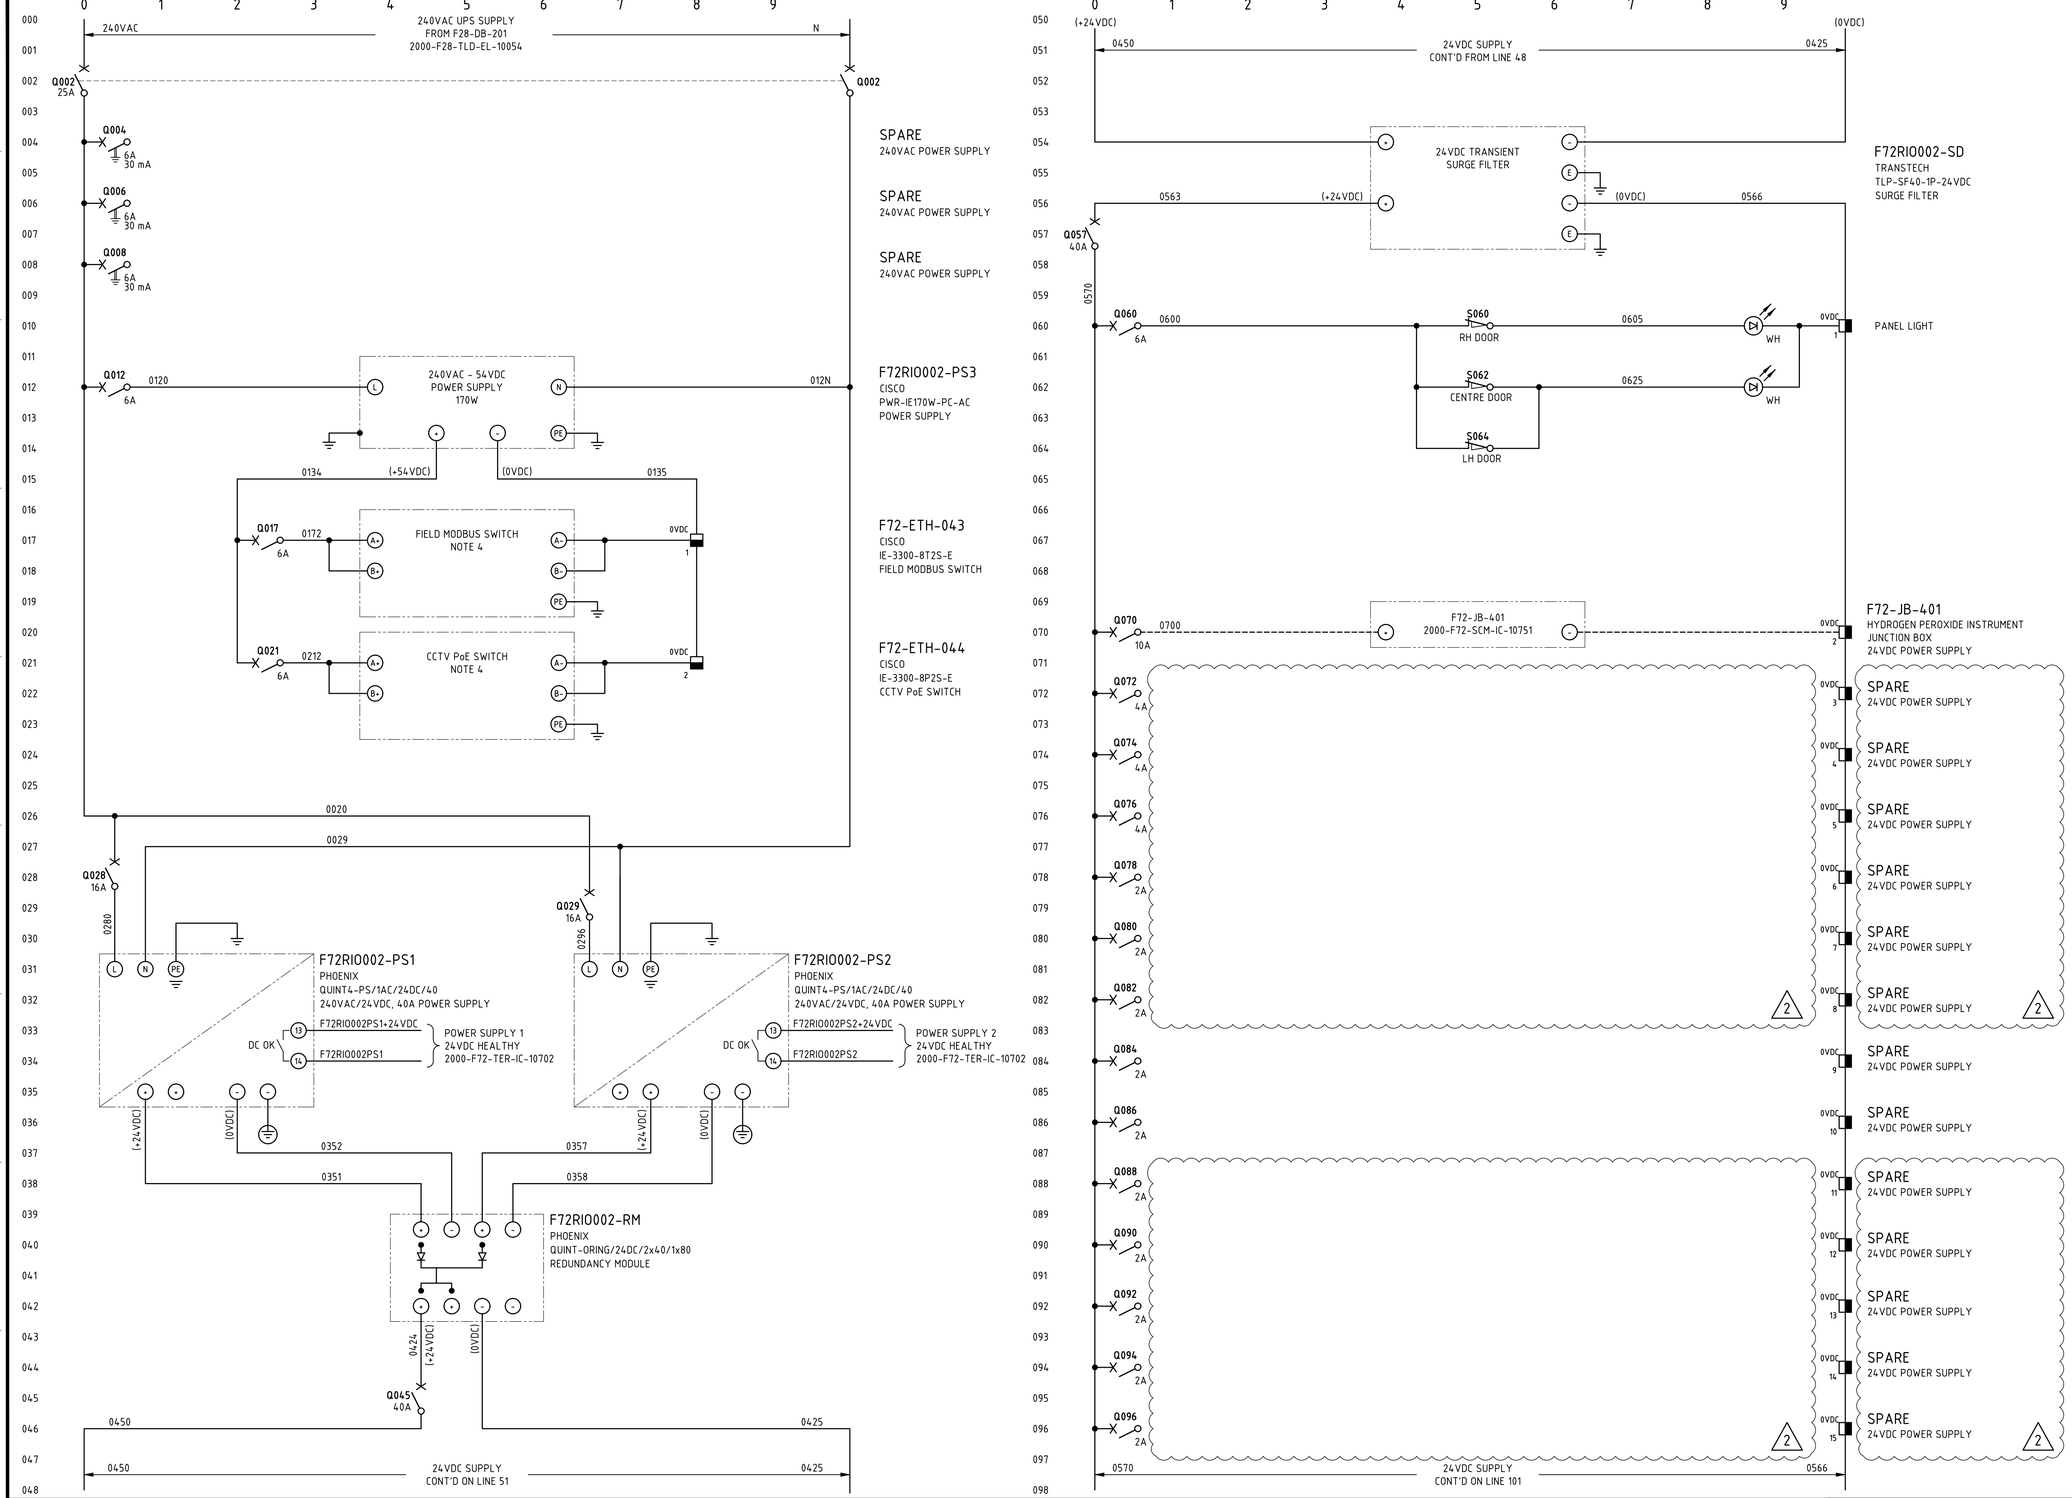


NOTES

1. TERMINALS ON TERMINAL STRIPS ABOVE 50VAC SHALL HAVE A SEPARATE PERSPEX SHROUD AND SHALL BE LABELLED "DANGER xxxVAC".
2. WIRE NUMBER FERRULES ON TERMINAL STRIP SHALL BE PREFIXED WITH EQUIPMENT NUMBER e.g. F72RIO002-xxxx.
3. EACH WIRE SHALL BE IDENTIFIED AT BOTH ENDS WITH FERRULES.
4. FOR NETWORK CONNECTION & BUS CABLING DETAILS REFER TO RIO PANEL COMMUNICATIONS TERMINATION DIAGRAMS.

LEGEND

- FIELD TERMINAL
- DCS OR I/O TERMINAL
- 0VDC TERMINAL FOR 24VDC
- 0VDC TERMINAL FOR 54VDC
- DEVICE TERMINAL
- INDICATION LAMP (cc = COLOUR)
- EARTH BAR
- INSTRUMENT EARTH BAR

DRG No.	REFERENCES
2000-F28-TLD-EL-10054	F28-DB-201 SWITCHROOM 240V UPS DB THREE LINE DIAGRAM
2000-F72-DRG-IC-10701	F72-RIO-002 FIELD N-IO PANEL GENERAL ARRANGEMENT
2000-F72-SCM-IC-10702	F72-RIO-002 FIELD N-IO PANEL SCHEMATIC DIAGRAM SHEET 2
2000-F72-TER-IC-10700	F72-RIO-002 FIELD N-IO PANEL COMMUNICATIONS TERMINATION DIAGRAMS SHEET 1 (TO SHEET 2 - 10701)
2000-F72-TER-IC-10702	F72-RIO-002 FIELD N-IO PANEL TERMINATION DIAGRAMS SHEET 1 (TO SHEET 13 - 10714)
2000-F00-STD-EL-10001	GENERAL NOTES AND STANDARD DRAWINGS INDEX

REV	DATE	DESCRIPTION	DRAW	CHECK	DESIGN	TECH APP	PROJ APP
2	03OCT25	DELETED INSTRUMENTS					
1	16APR25	DELETED INSTRUMENTS					
0	28MAR25	APPROVED FOR CONSTRUCTION					

NORTHERN STAR RESOURCES LIMITED

PRIMERO
primero.com.au | DESIGN | CONSTRUCT | OPERATE

PRIMERO PROJECT NUMBER: 23517

INFORMATION AND REPRESENTATIONS ON THIS DRAWING ARE THE INTELLECTUAL PROPERTY OF PRIMERO UNLESS SPECIFICALLY IDENTIFIED OTHERWISE. ALL RIGHTS INCLUDING USE RESERVED

PROJECT: NORTHERN STAR RESOURCES LTD
KCGM GROWTH PROJECT

TITLE: REAGENTS MIXING & STORAGE - ACID
F72-RIO-002 REAGENTS FIELD N-IO PANEL
SCHEMATIC DIAGRAM SHEET 1

SHEET	SCALE	DRG No.	REVISION
A1	NONE	2000-F72-SCM-IC-10701	2

O:\CAD PROJECTS\235 NORTHERN STAR RESOURCES LTD\23517 KCGM GROWTH PROJECT\03 DELIVERABLES\IC\F72 - REAGENTS MIXING & STORAGE\2000-F72-SCM-IC-10701.DWG 10OCT25 3:09PM HOTSEAT04