


- LEGEND:
- EXISTING
 - NEW
 - INTERMITTENT
 - DECOMMISSIONED
 - HIGH CYANIDE TRANSFER

- NOTES:
- FUTURE WORKS, NOT CURRENTLY SHOWN ON THE RELEVANT P&ID (2000-F75-PID-PR-25009).

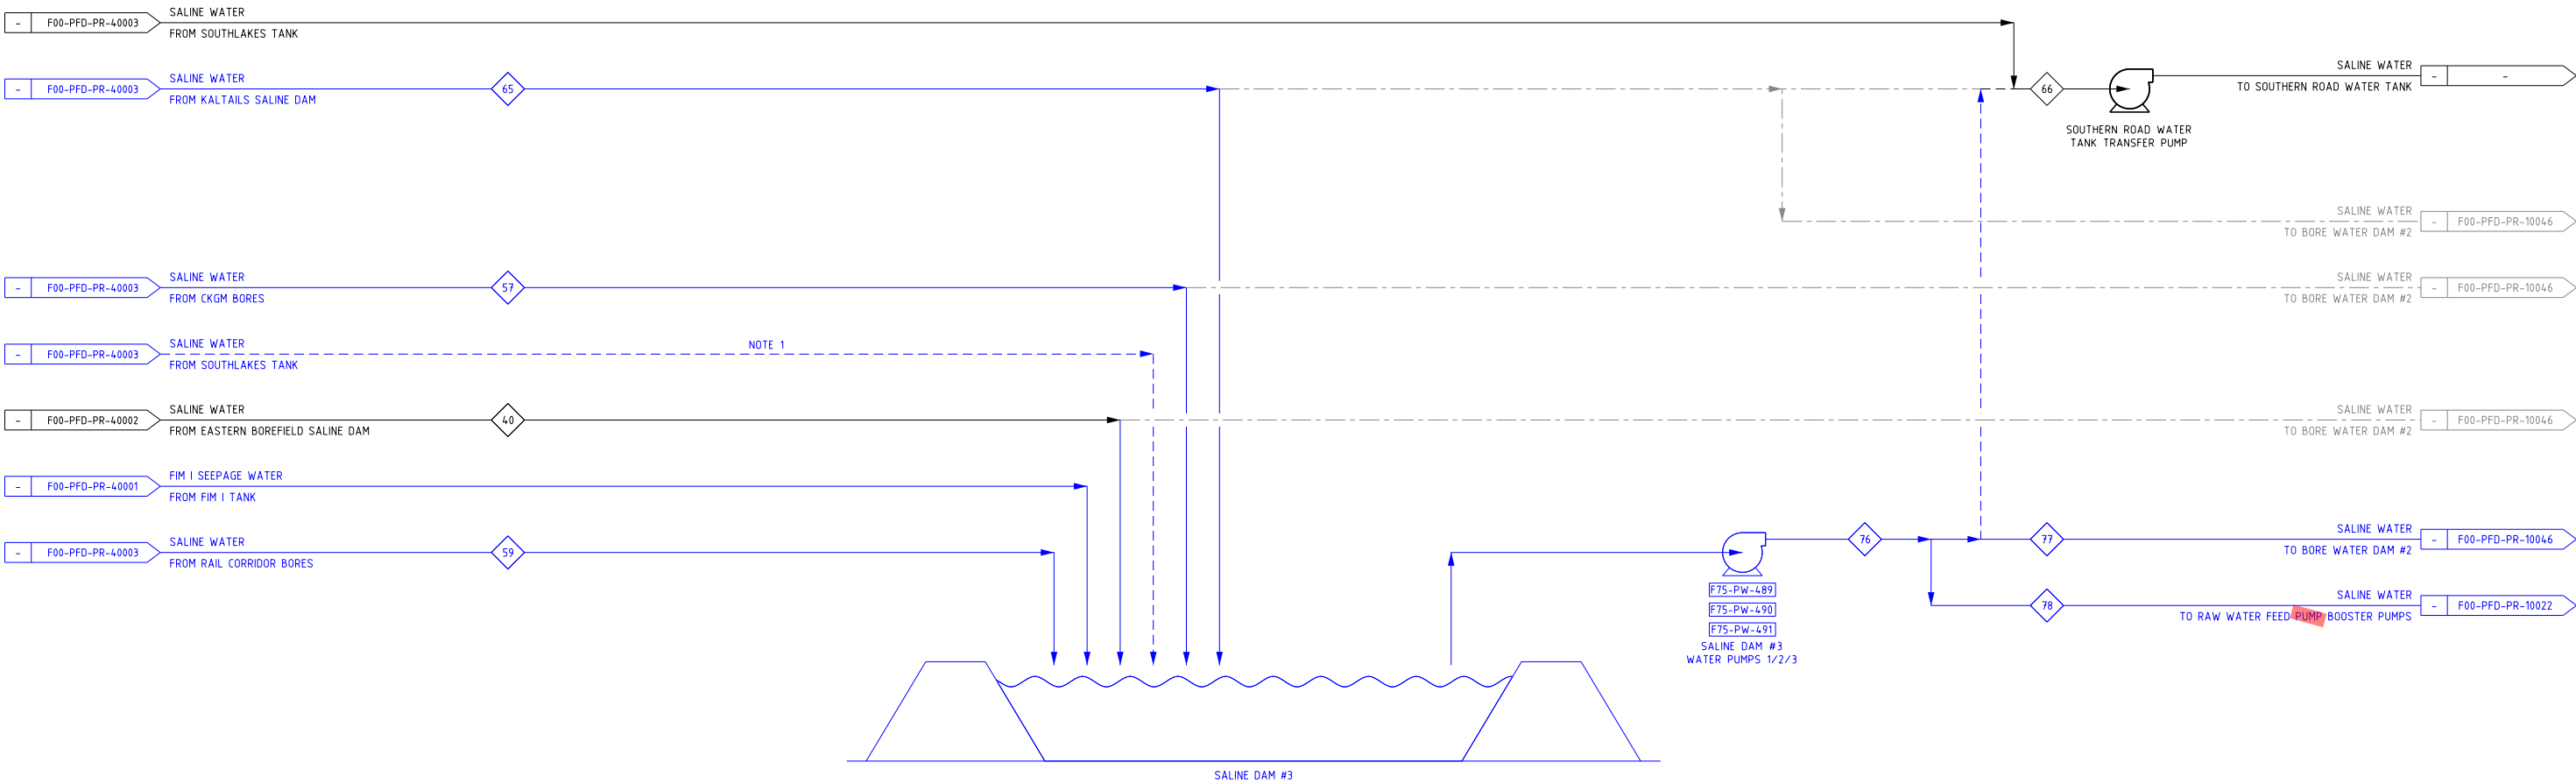

ISSUED FOR
USE