


D:\CAD PROJECTS\235 NORTHERN STAR RESOURCES LTD\23517 KCGM GROWTH PROJECT\03 DELIVERABLES\EL\F28 - ULTRAFINE GRINDING 2 & 3\2000-F28-SLD-EL-10051.DWG 29SEP26 7:27AM ROBIN LAW

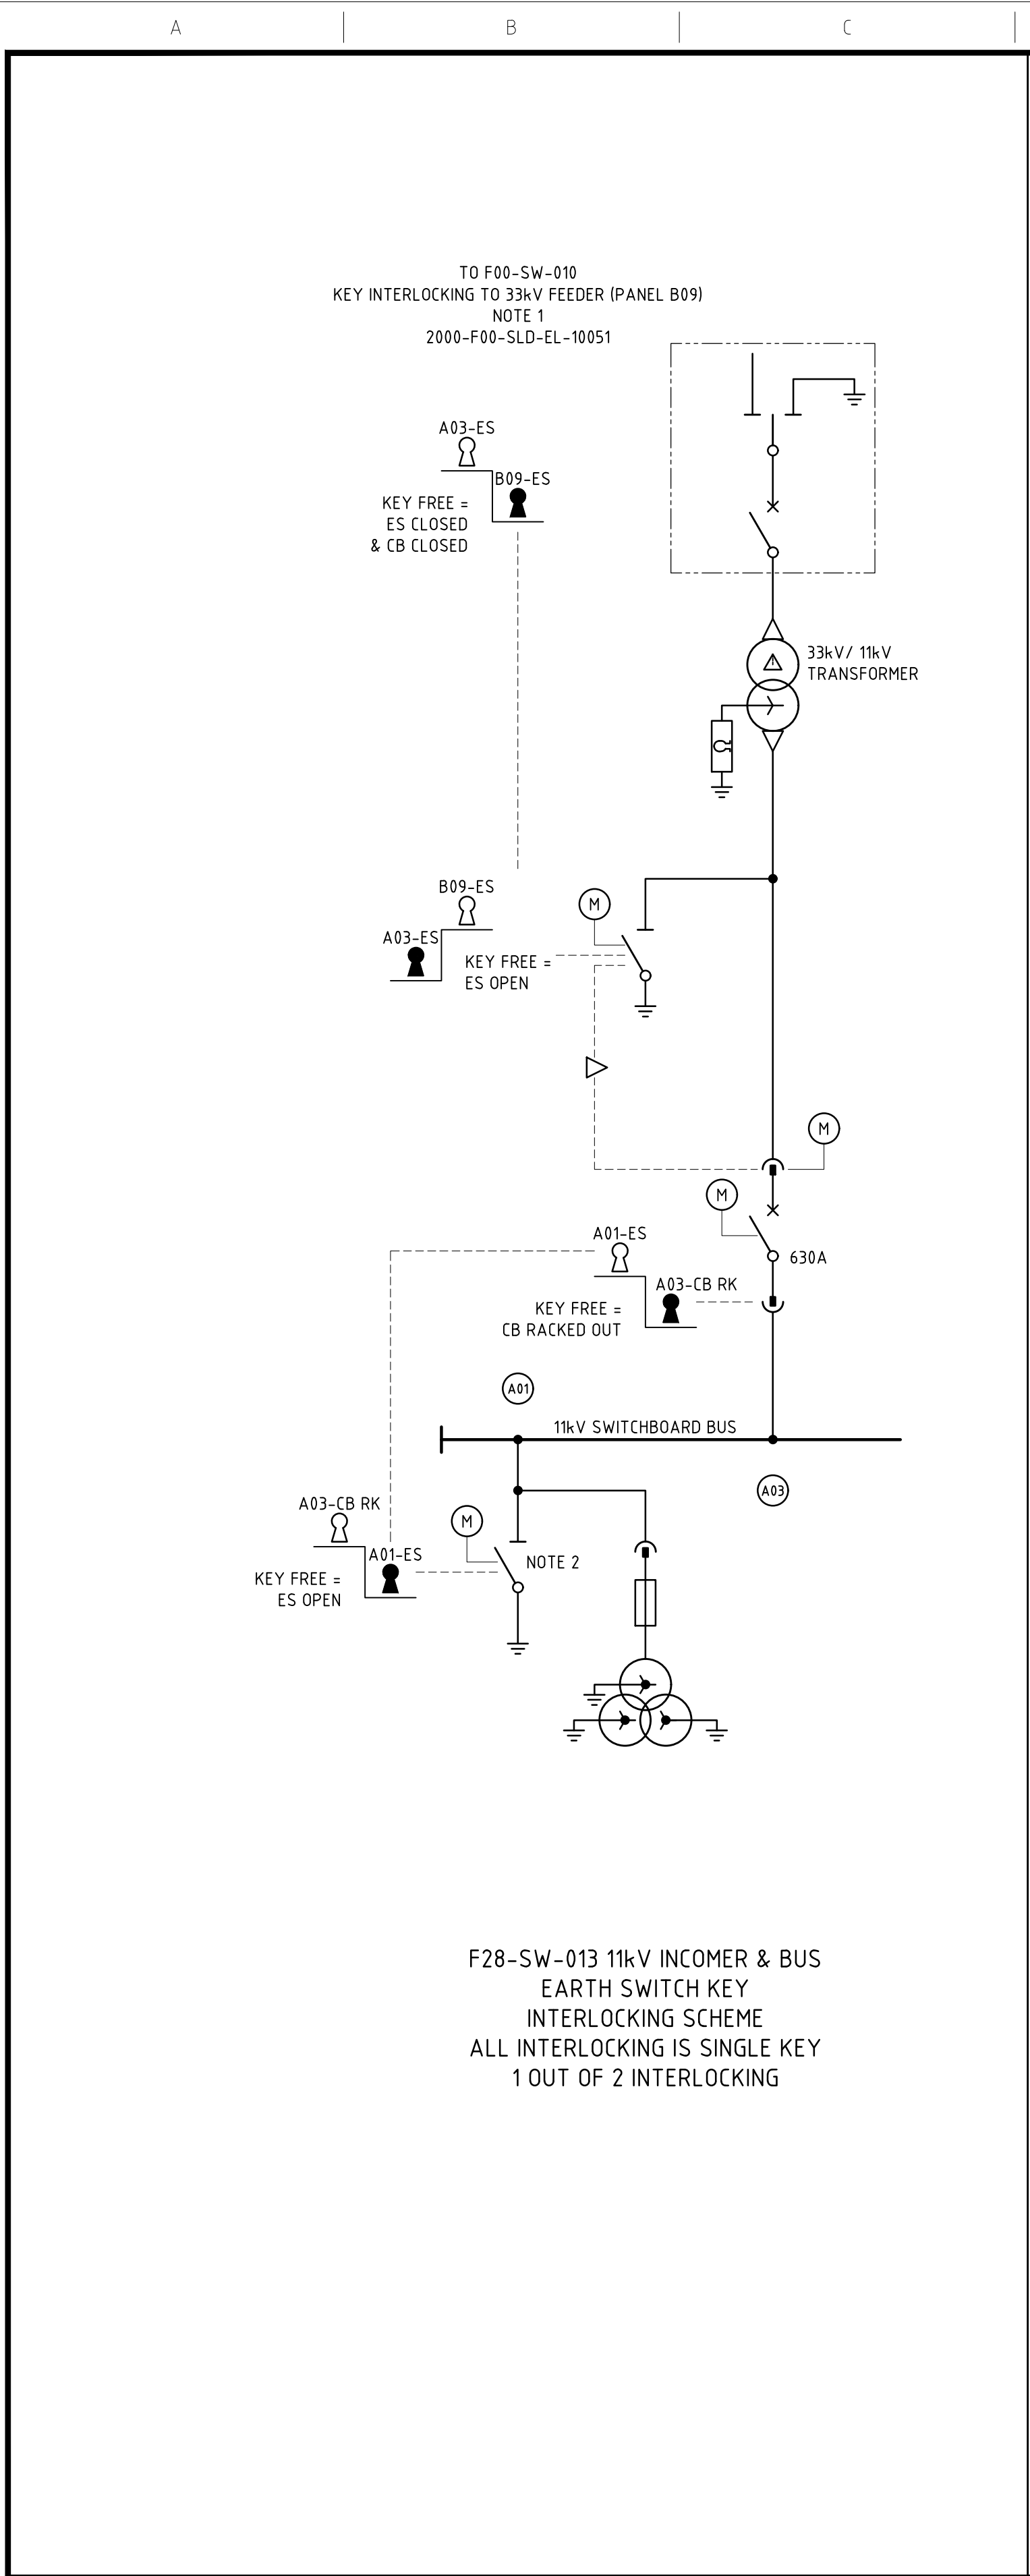

NOTES

- UPSTREAM 33kV FEEDER 3 POSITION SWITCH KEY INTERLOCKED WITH THE 11kV SWITCHBOARD INCOMER EARTH SWITCH SUCH THAT THE UPSTREAM 3 POSITION SWITCH MUST BE CLOSED IN THE EARTH POSITION AND THE FEEDER CIRCUIT BREAKER CLOSED WHEN THE 11kV INCOMER EARTH SWITCH IS CLOSED.
- BUS EARTH SWITCH AND INCOMER CIRCUIT BREAKER SHALL BE KEY INTERLOCKED SUCH THAT BUS EARTH SWITCH CANNOT BE CLOSED WHILE INCOMER CIRCUIT BREAKER IS RACKED IN.

LEGEND

- ▽--- MECHANICAL OR ELECTRICAL INTERLOCK DEVICE
- ⬮ KEY FREE
- ⬮ KEY CAPTIVE

2000-F00-LST-EL-11004	ELECTRICAL INTERLOCKING SCHEDULE								
2000-F28-DRG-EL-10001	F28-SR-001 11kV ULTRAFINE GRINDING TAILS SWITCHROOM ELECTRICAL EQUIPMENT LAYOUT								
2000-F28-SLD-EL-10001	F28-SW-013 ULTRAFINE GRINDING 2/3 11kV SWITCHBOARD SINGLE LINE DIAGRAM								
2000-F00-SLD-EL-10001	OVERALL SITEWIDE SINGLE LINE DIAGRAM								
2000-F00-STD-EL-10001	GENERAL NOTES AND STANDARD DRAWINGS INDEX								
DRG No.	REFERENCES	REV	DATE	DESCRIPTION	DRAW	CHECK	DESIGN	TECH APP	PROJ APP



PRIMERO PROJECT NUMBER:
23517

INFORMATION AND REPRESENTATIONS ON THIS DRAWING ARE THE INTELLECTUAL PROPERTY OF PRIMERO UNLESS SPECIFICALLY IDENTIFIED OTHERWISE. ALL RIGHTS INCLUDING USE RESERVED

PROJECT:	NORTHERN STAR RESOURCES LTD KCGM GROWTH PROJECT		
TITLE:	ULTRA FINE GRINDING 2/3 F28-SW-013 11kV SWITCHBOARD KEY INTERLOCKING SINGLE LINE DIAGRAM		
SHEET A1	SCALE NONE	DRG No. 2000-F28-SLD-EL-10051	REVISION 2