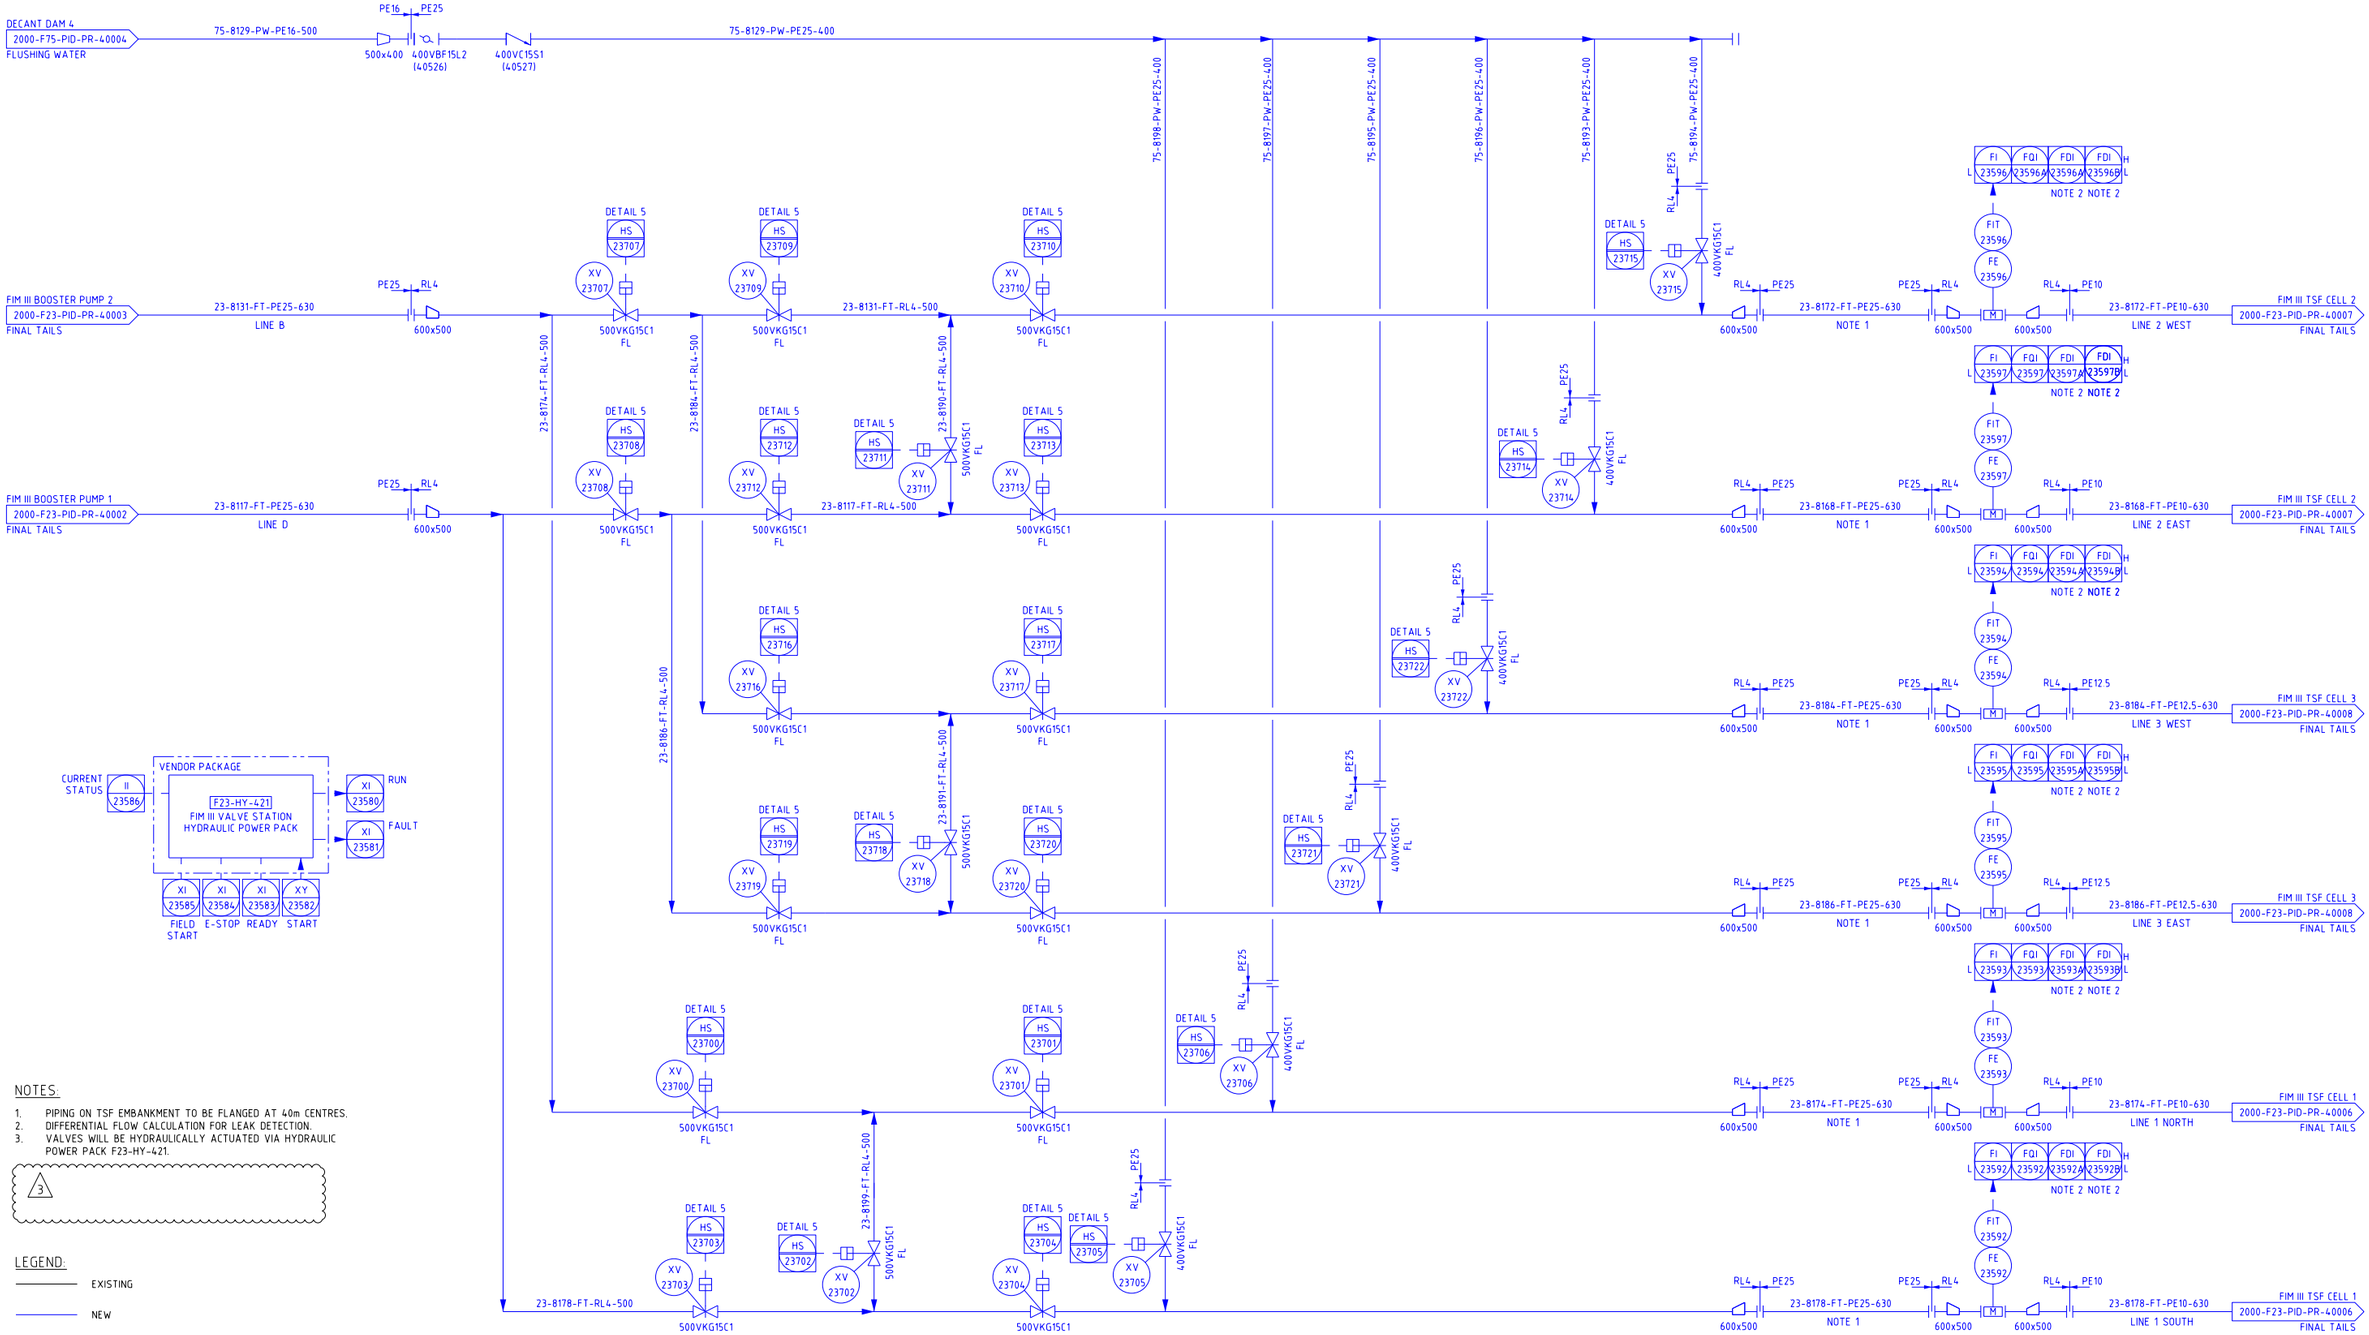



NOTES:

1. PIPING ON TSF EMBANKMENT TO BE FLANGED AT 40m CENTRES.
2. DIFFERENTIAL FLOW CALCULATION FOR LEAK DETECTION.
3. VALVES WILL BE HYDRAULICALLY ACTUATED VIA HYDRAULIC POWER PACK F23-HY-421.

△3

LEGEND:

- EXISTING
- NEW
- FUTURE
- DECOMMISSIONED

APPROVED FOR CONSTRUCTION