


LEGEND:

— EXISTING
— NEW
— FUTURE
- - - - - DECOMMISSIONED

NOTES:

1. VALVE TO BE INSTALLED WITHOUT A HANDLE.
2. MANUAL OPERATED VALVE WITH PROXIMITY SWITCHES.

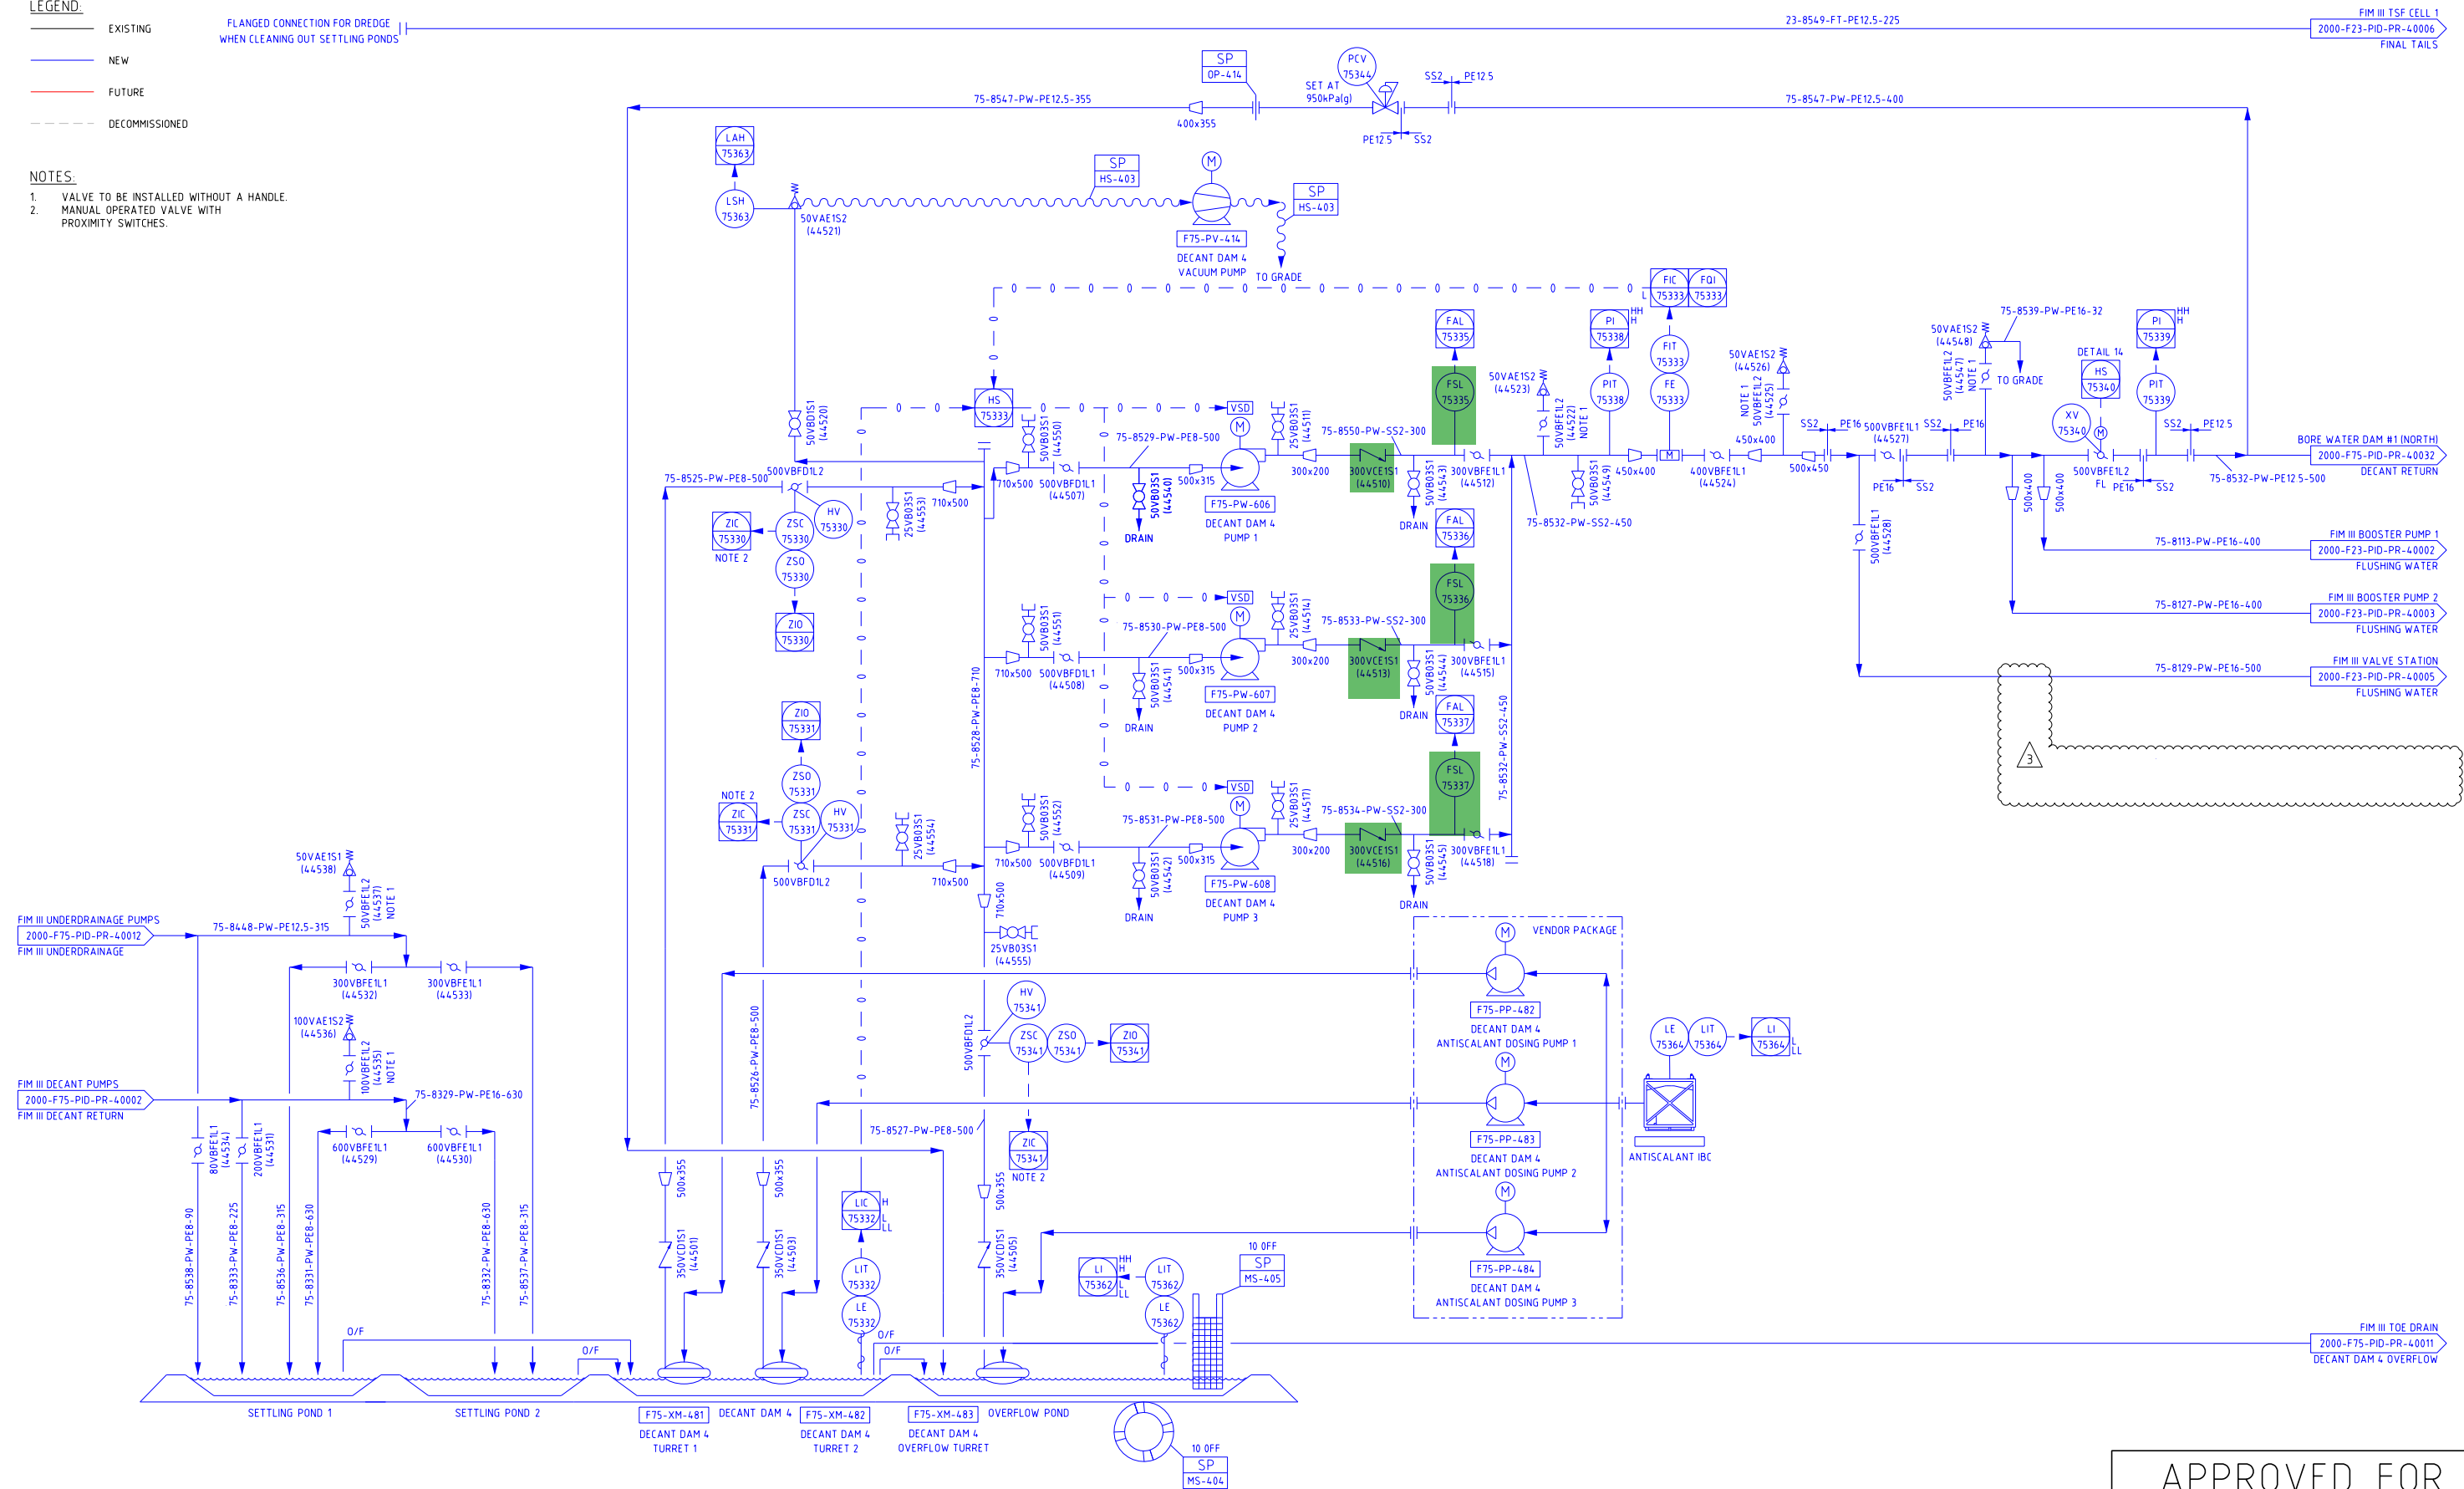

APPROVED FOR
CONSTRUCTION