

LEGEND:

EXISTING


NEW

FUTURE

DECOMMISSIONED

NOTES:

1. SEEPAGE WATER HEADER HAS BEEN SIZED FOR A MAXIMUM OF 20 FUTURE SEEPAGE BORE PUMPS ACCORDING TO HYDROGEOLOGY REPORT 2000-T00-REP-GE-40001 FOR FIM II CELL G.

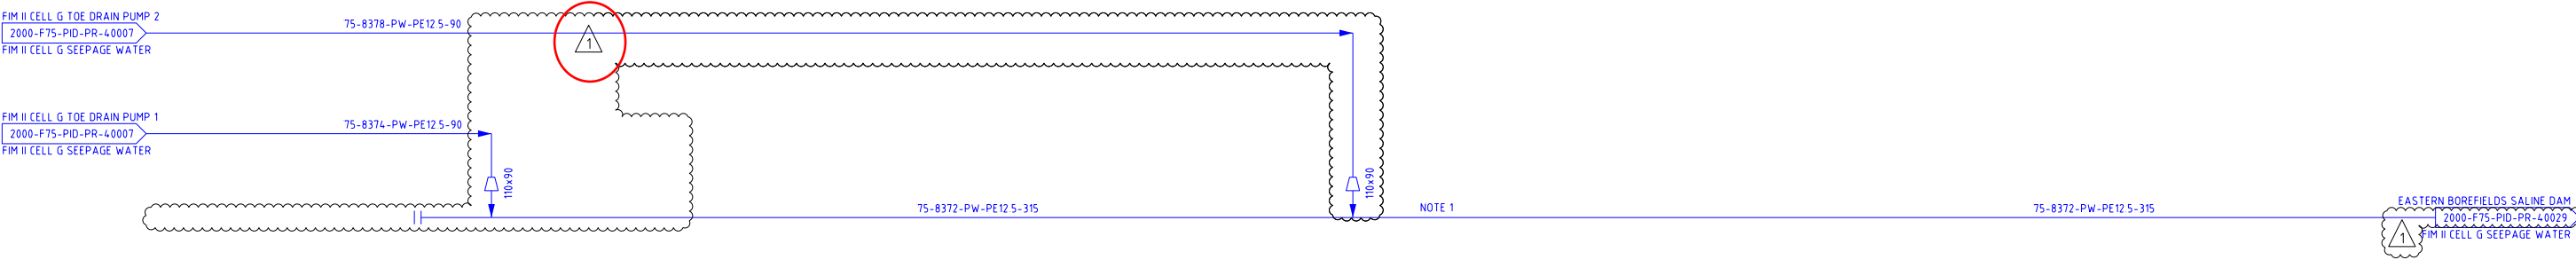

APPROVED FOR
CONSTRUCTION