


- LEGEND:
- EXISTING
 - NEW
 - FUTURE
 - DECOMMISSIONED

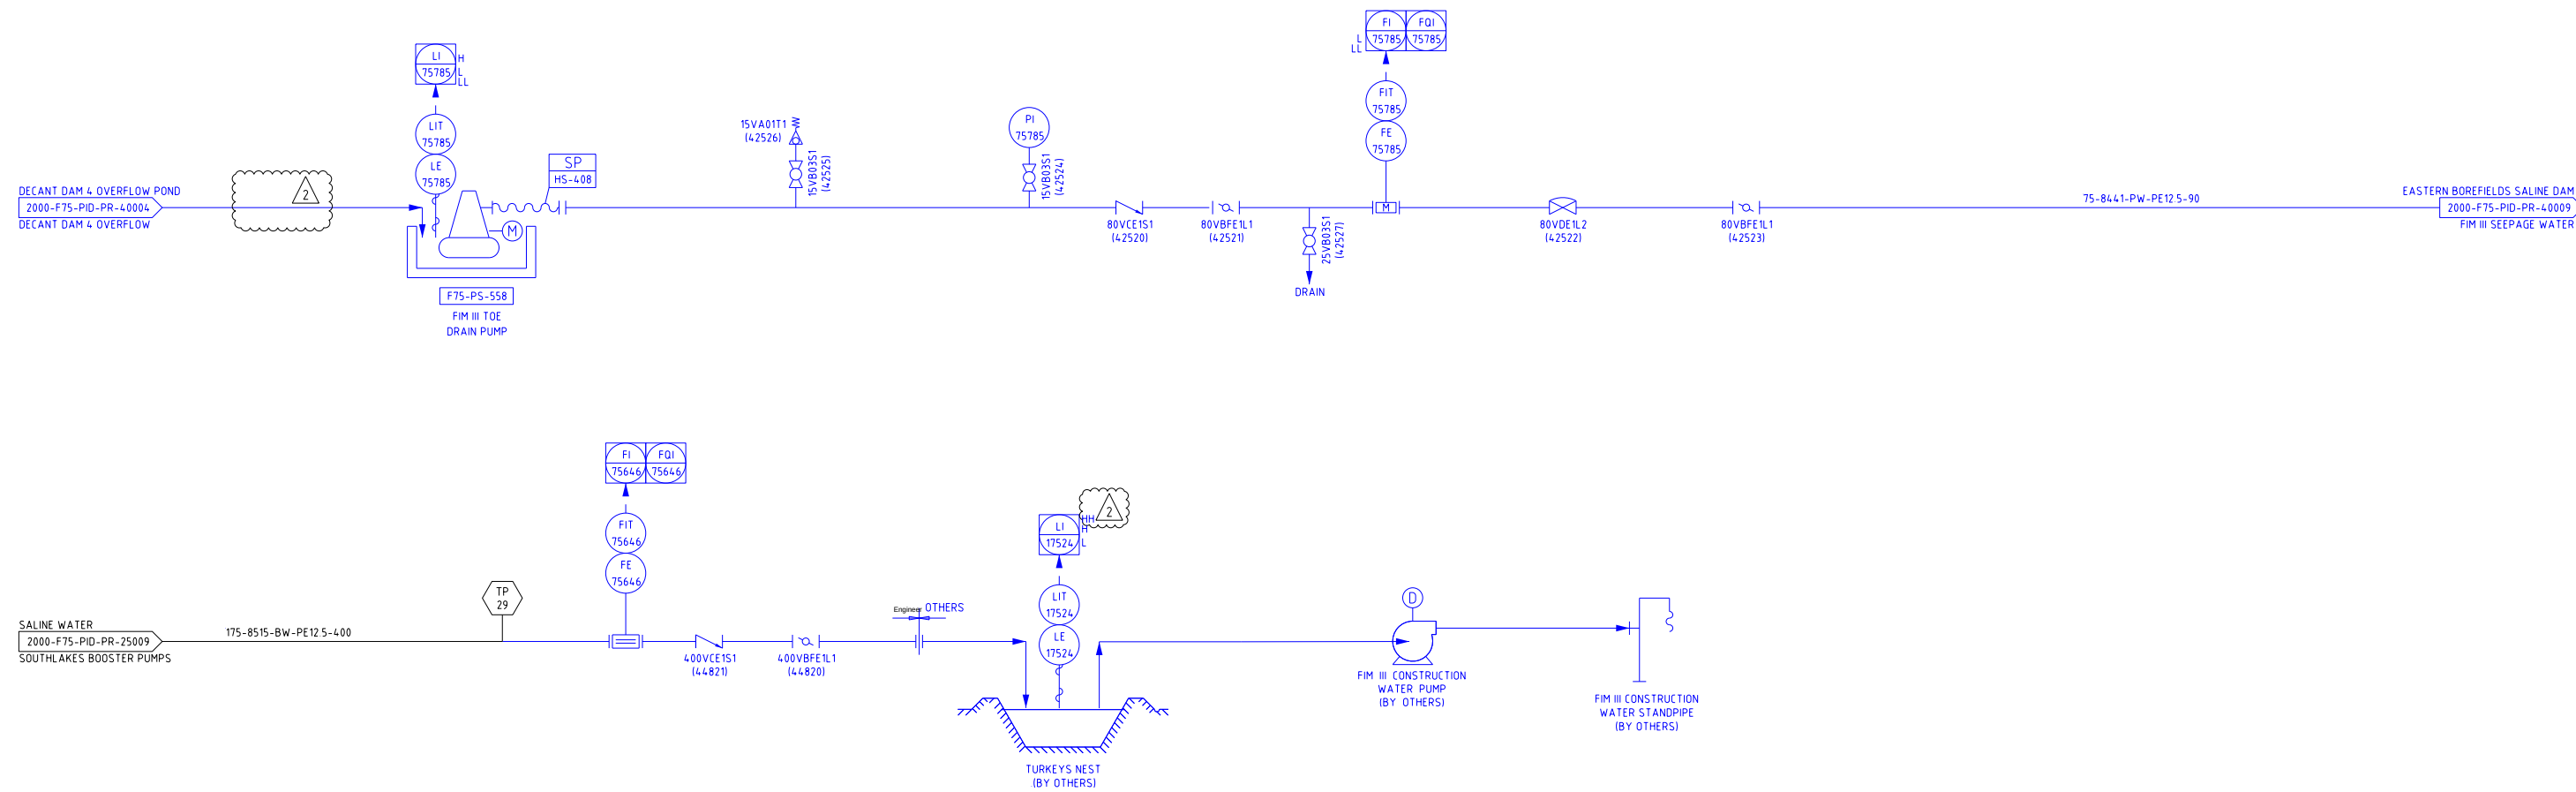

APPROVED FOR
CONSTRUCTION