
F13-SR-001
415V SAG MILL SWITCHROOM

F13-SW-002
SAG MILL 415V MOTOR CONTROL CENTRE

CONTINUED ON SHT 2
2000-F13-SLD-EL-10302

CONTINUED ON SHT 4
2000-F13-SLD-EL-10304

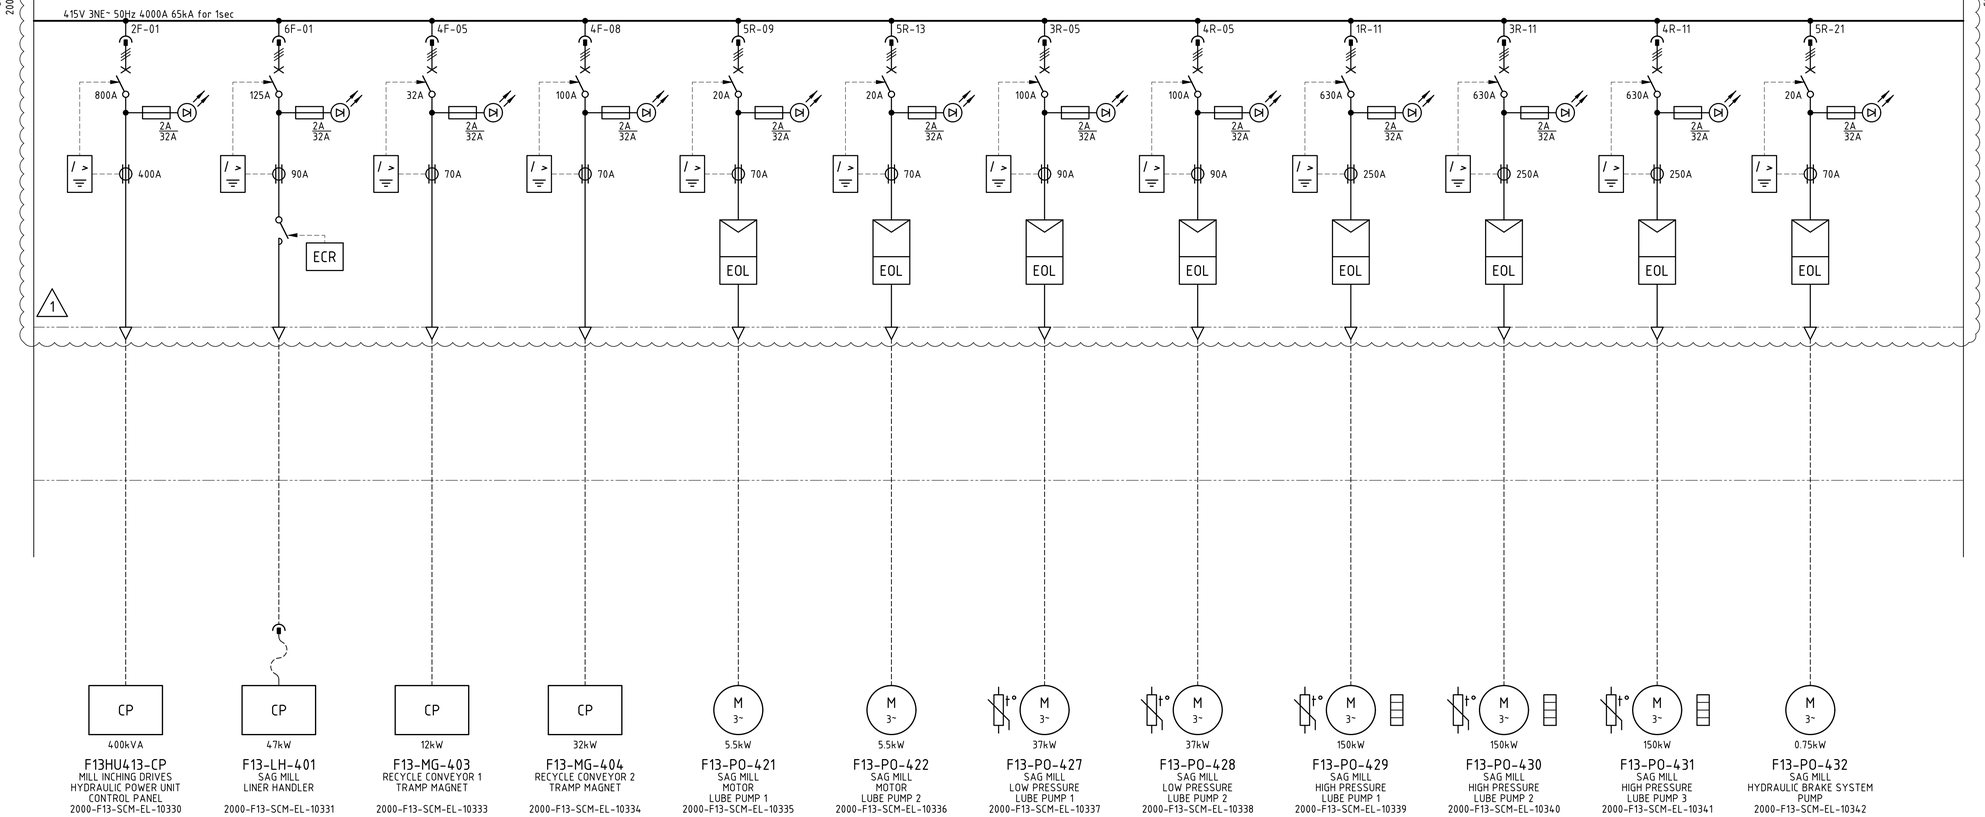


## NOTES

1. REFER TO SHEET 1.

## LEGEND

1. REFER TO SHEET 1.

NORTHERN STAR RESOURCES LIMITED

| | |
|---|---|
| Approved | X |
| Approved as Noted | |
| Not Approved | |
| For Information Only | |

ACCEPTANCE DOES NOT RELIEVE THE SUPPLIER / CONTRACTOR OF ITS RESPONSIBILITY OR LIABILITIES UNDER THE PURCHASE ORDER / CONTRACT

# 2000-F13-SLD-EL-10303_Rev1

SAG mill F13-SW-002 415V MCC single line diagram sheet 3

O:\CAD PROJECTS\235 NORTHERN STAR RESOURCES LTD\235TI KCGM GROWTH PROJECT\03 DELIVERABLES\ELV\F13 - MILLING & CLASSIFICATION\2000-F13-SLD-EL-10303.DWG 27AUG25 7:51AM HOTSEAT04