
F21-SR-001
415V CIL4 SWITCHROOM

F21-SW-006
CIL4 415V MOTOR CONTROL CENTRE No.1

CONTINUED ON SHT 3
2000-F21-SLD-EL-10203

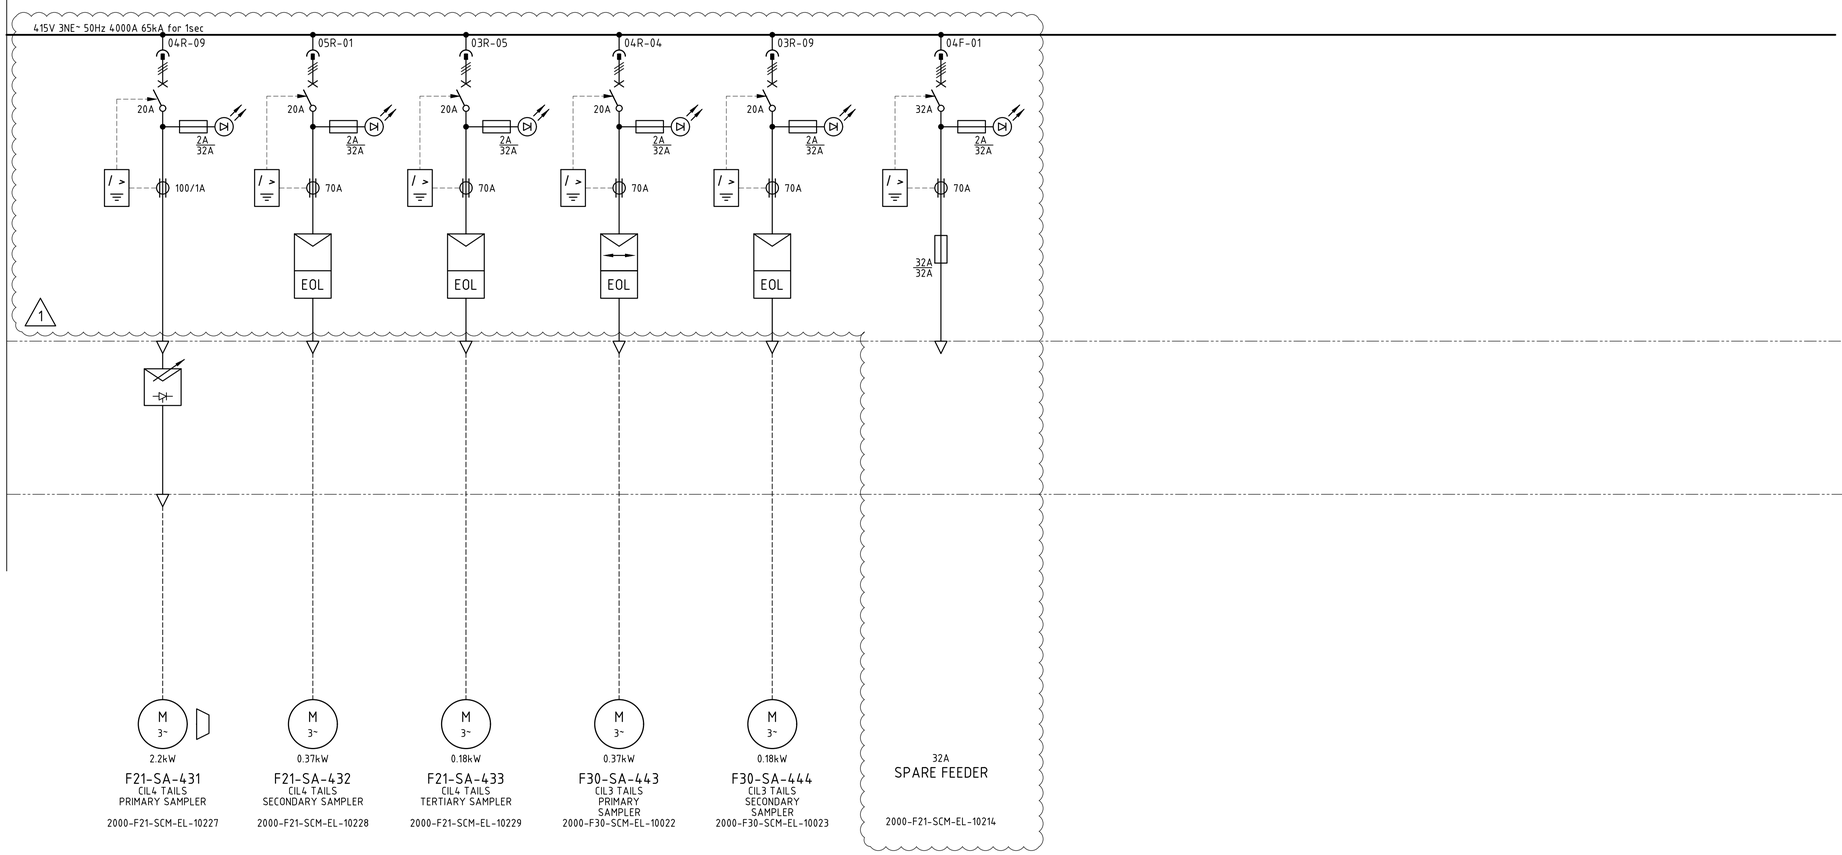

NOTES

1. REFER TO SHEET 1.

LEGEND

1. REFER TO SHEET 1.

Approved	X
Approved as Noted	
Not Approved	
For Information Only	

ACCEPTANCE DOES NOT RELIEVE THE SUPPLIER / CONTRACTOR OF ITS RESPONSIBILITY OR LIABILITIES UNDER THE PURCHASE ORDER / CONTRACT

2000-F21-SLD-EL-10204_Rev1

Flotation tailings CIL4 F21-SW-006 415V MCC single line diagram sheet 4

O:\CAD PROJECTS\235 NORTHERN STAR RESOURCES LTD\23517 KCGM GROWTH PROJECT\03 DELIVERABLES\EL\F21 - FLOTATION TAILINGS CIL 4\2000-F21-SLD-EL-10204.DWG 06NOV25 11:07AM HOTSEAT04