
F21-SR-001
415V CIL4 SWITCHROOM

F21-SW-007
CIL4 415V MOTOR CONTROL CENTRE No.2

CONTINUED ON SHT 1
2000-F21-SLD-EL-10251

CONTINUED ON SHT 3
2000-F21-SLD-EL-10253

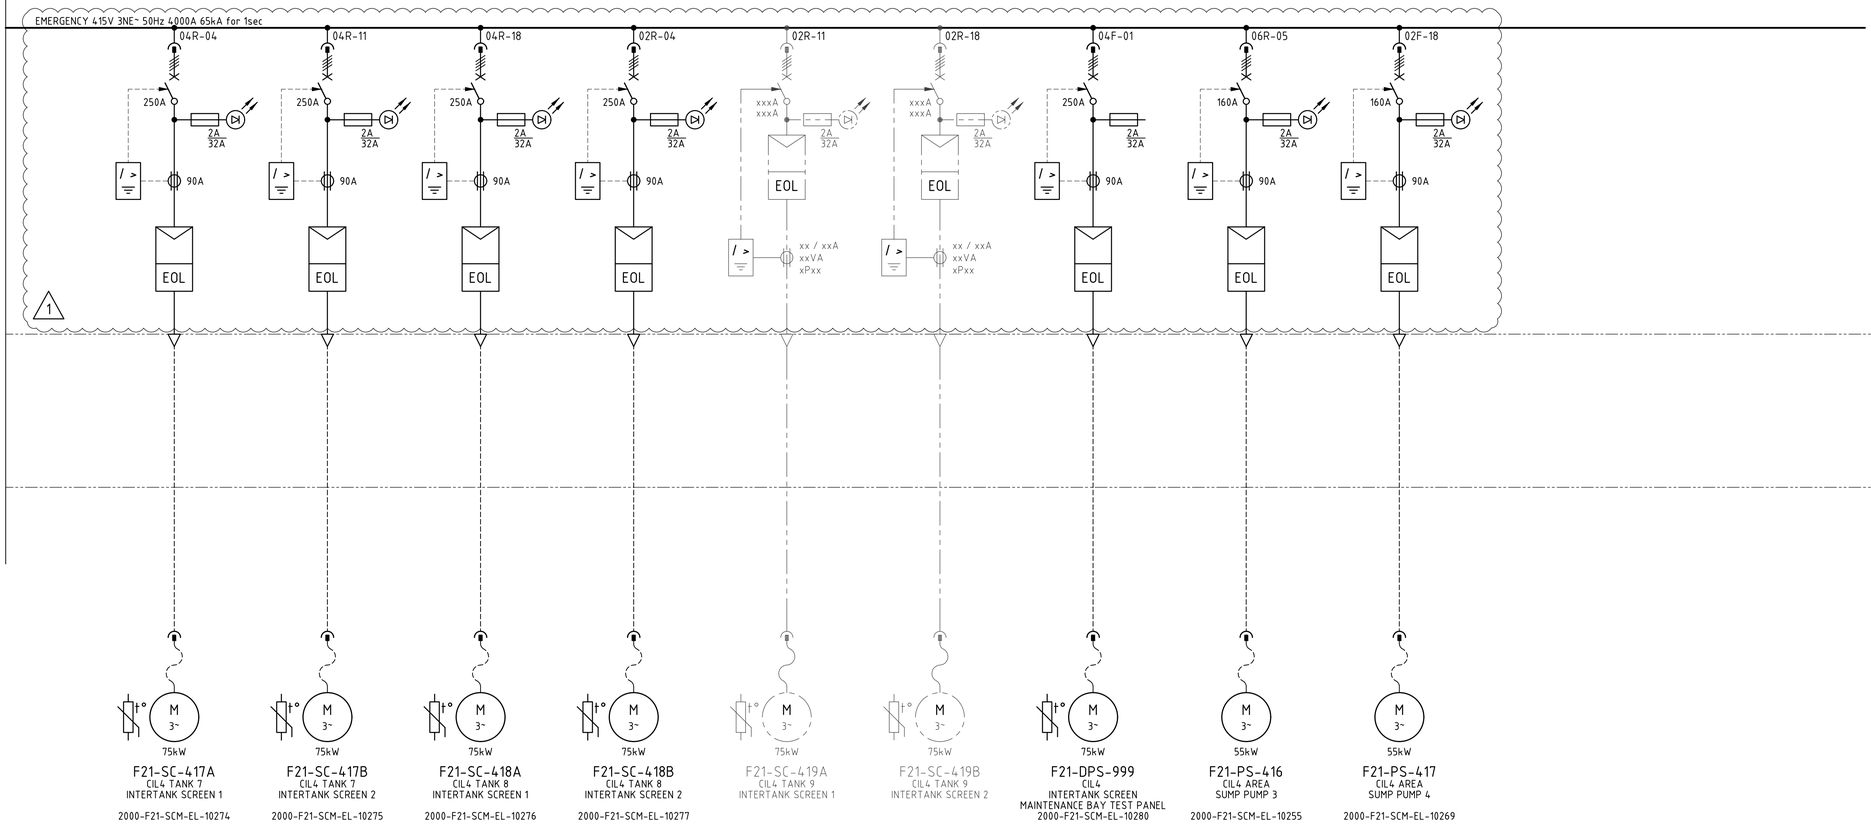

NOTES

1. REFER TO SHEET 1.

LEGEND

1. REFER TO SHEET 1.

NORTHERN STAR RESOURCES LTD

Approved	☒
Approved as Noted	☐
Not Approved	☐
For Information Only	

ACCEPTANCE DOES NOT RELIEVE THE SUPPLIER / CONTRACTOR OF ITS RESPONSIBILITY OR LIABILITIES UNDER THE PURCHASE ORDER / CONTRACT

2000-F21-SLD-EL-10252_Rev1

Flotation tailings CIL4 F21-SW-007 415V MCC single line diagram sheet 2

O:\CAD PROJECTS\235 NORTHERN STAR RESOURCES LTD\23517 KCGM GROWTH PROJECT\03 DELIVERABLES\ELEC\F21 - FLOTATION TAILINGS CIL 4\2000-F21-SLD-EL-10252.DWG 06NOV25 11:07AM HOTSEAT04