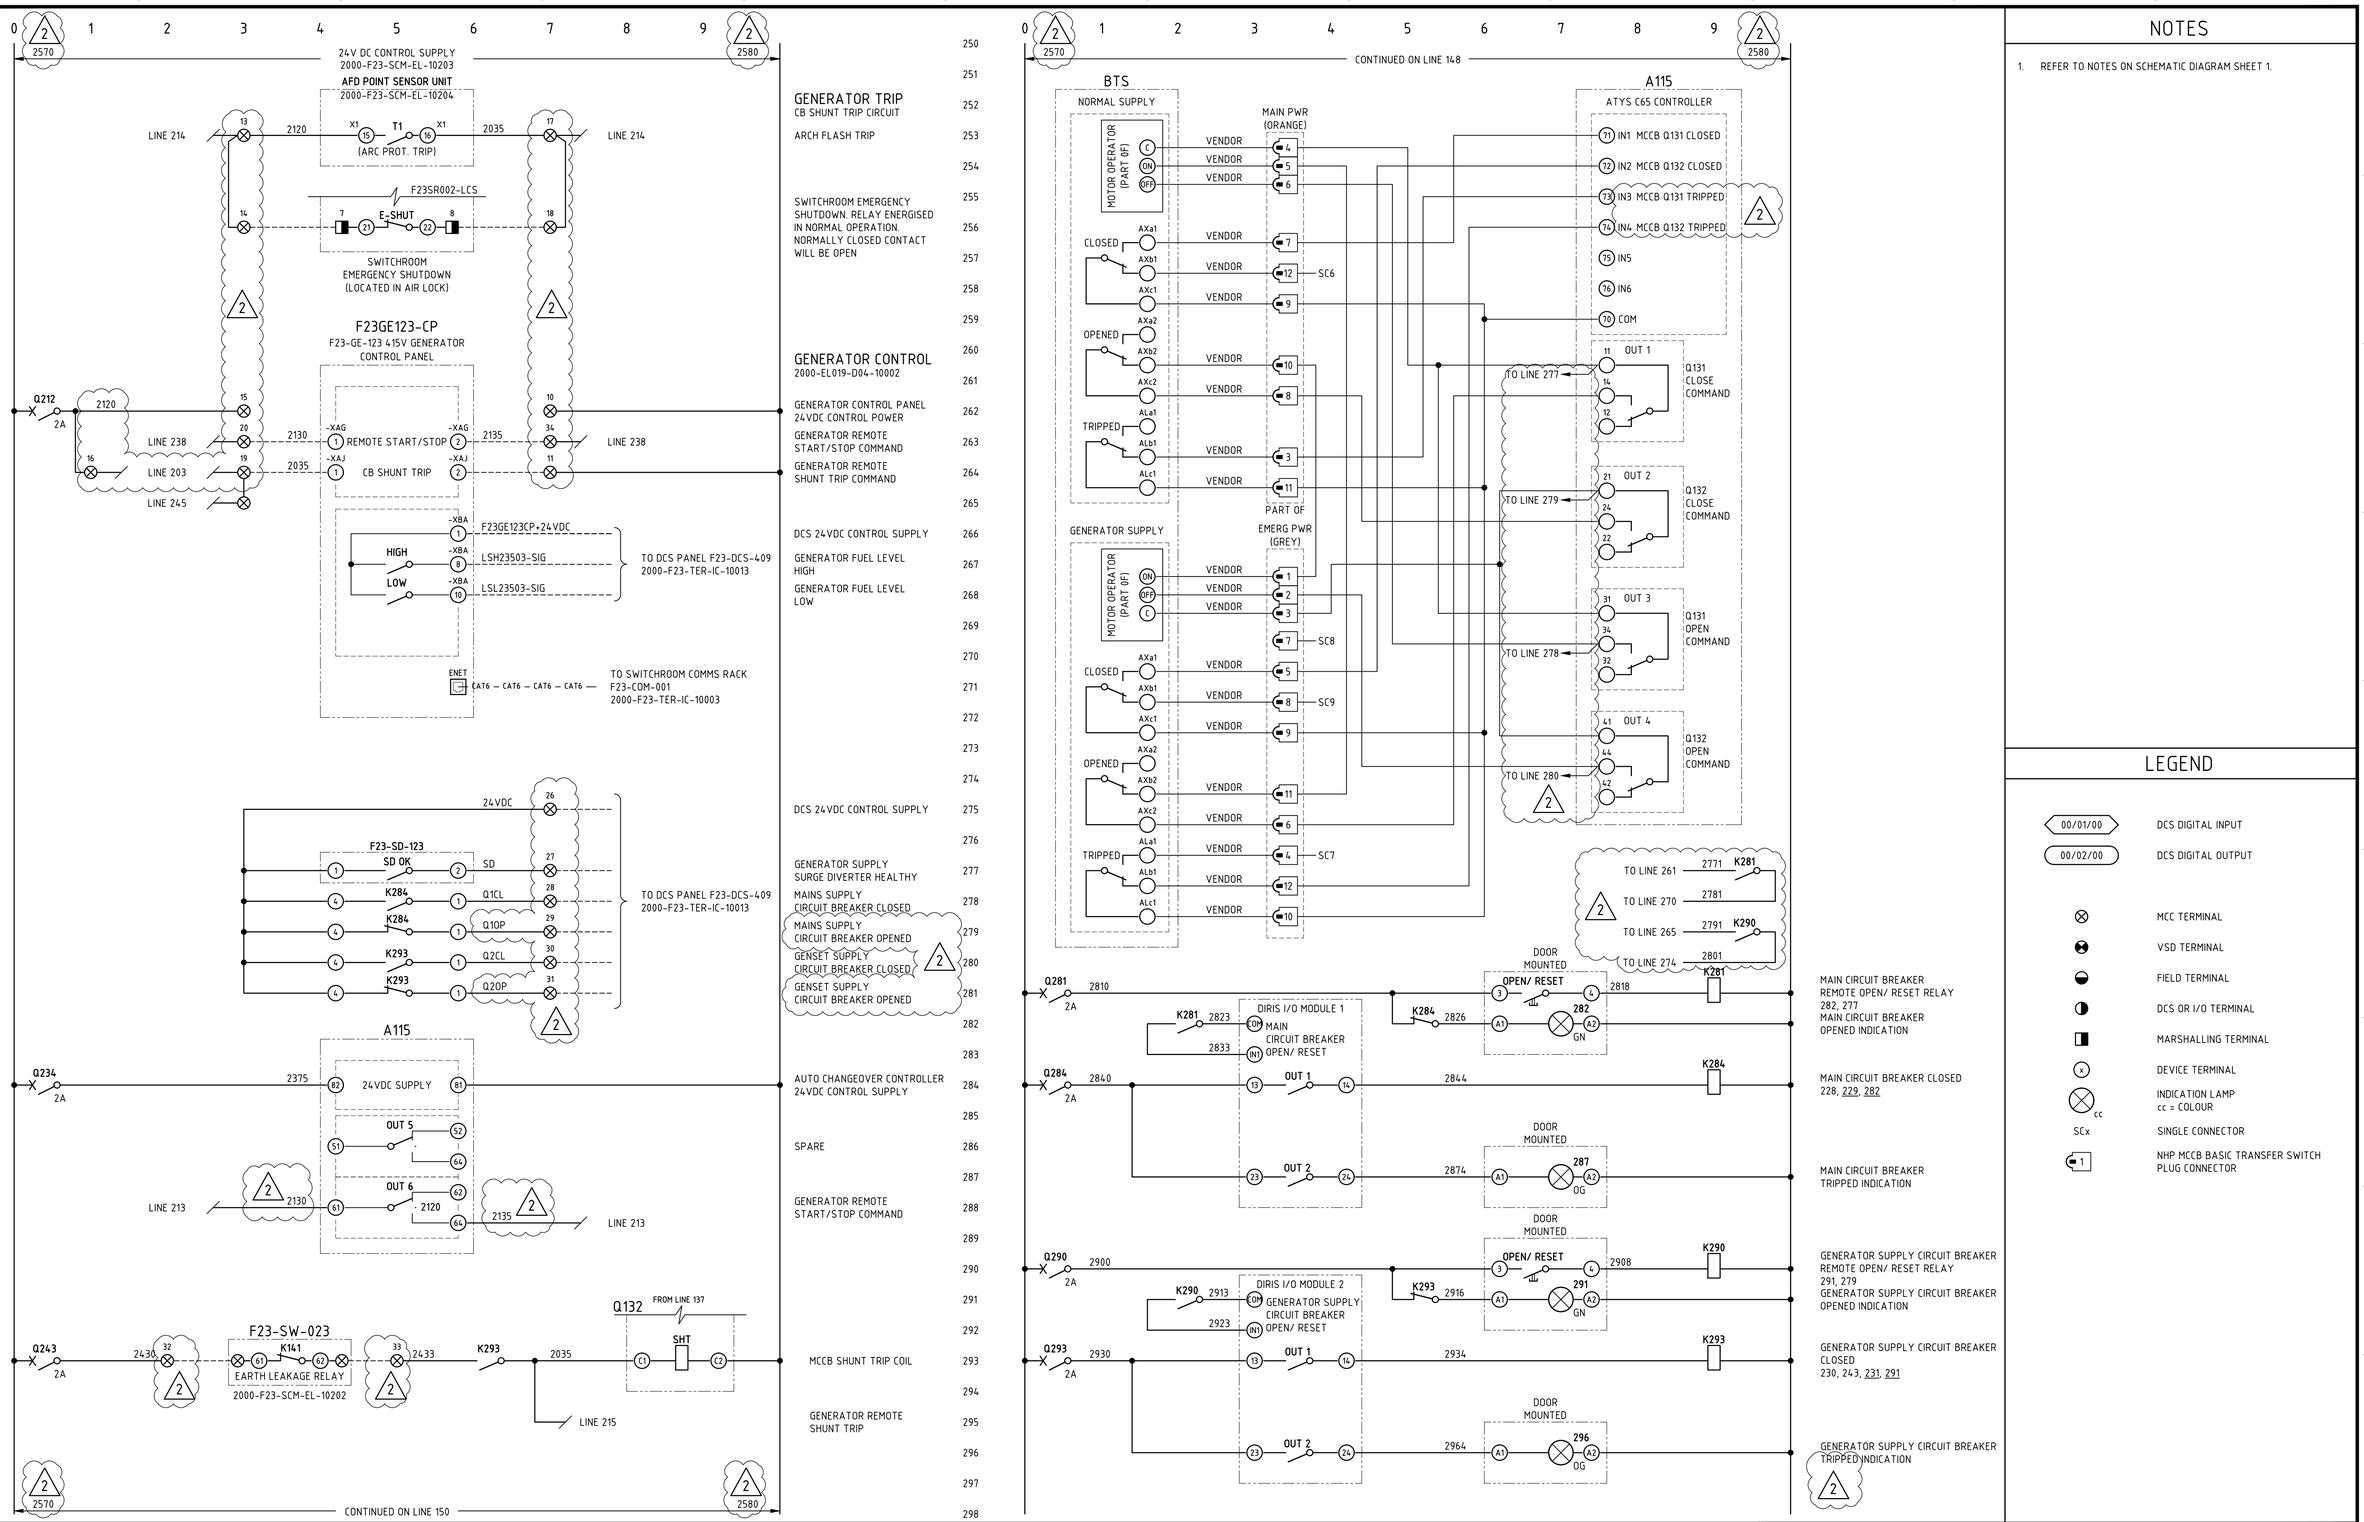


NOTES

1. REFER TO NOTES ON SCHEMATIC DIAGRAM SHEET 1.

LEGEND

- 00/01/00 — DCS DIGITAL INPUT
- 00/02/00 — DCS DIGITAL OUTPUT
- MCC TERMINAL
- VSD TERMINAL
- FIELD TERMINAL
- DCS OR I/O TERMINAL
- MARSHALLING TERMINAL
- DEVICE TERMINAL
- INDICATION LAMP (cc = COLOUR)
- SCx — SINGLE CONNECTOR
- NHP MCCB BASIC TRANSFER SWITCH PLUG CONNECTOR

2000-F23-SCM-EL-10223_Rev2

F23-SW-123 - F23-SW-023 415V emergency MCC incomer - schematic diagram sheet 2

O:\CAD PROJECTS\235 NORTHERN STAR RESOURCES LTD\235IT KCGM GROWTH PROJECT\03 DELIVERABLES\ELV\F23 - FINAL TAILINGS HANDLING & STORAGE\2000-F23-SCM-EL-10223.DWG 020CT25 9:04AM HOTSEAT04