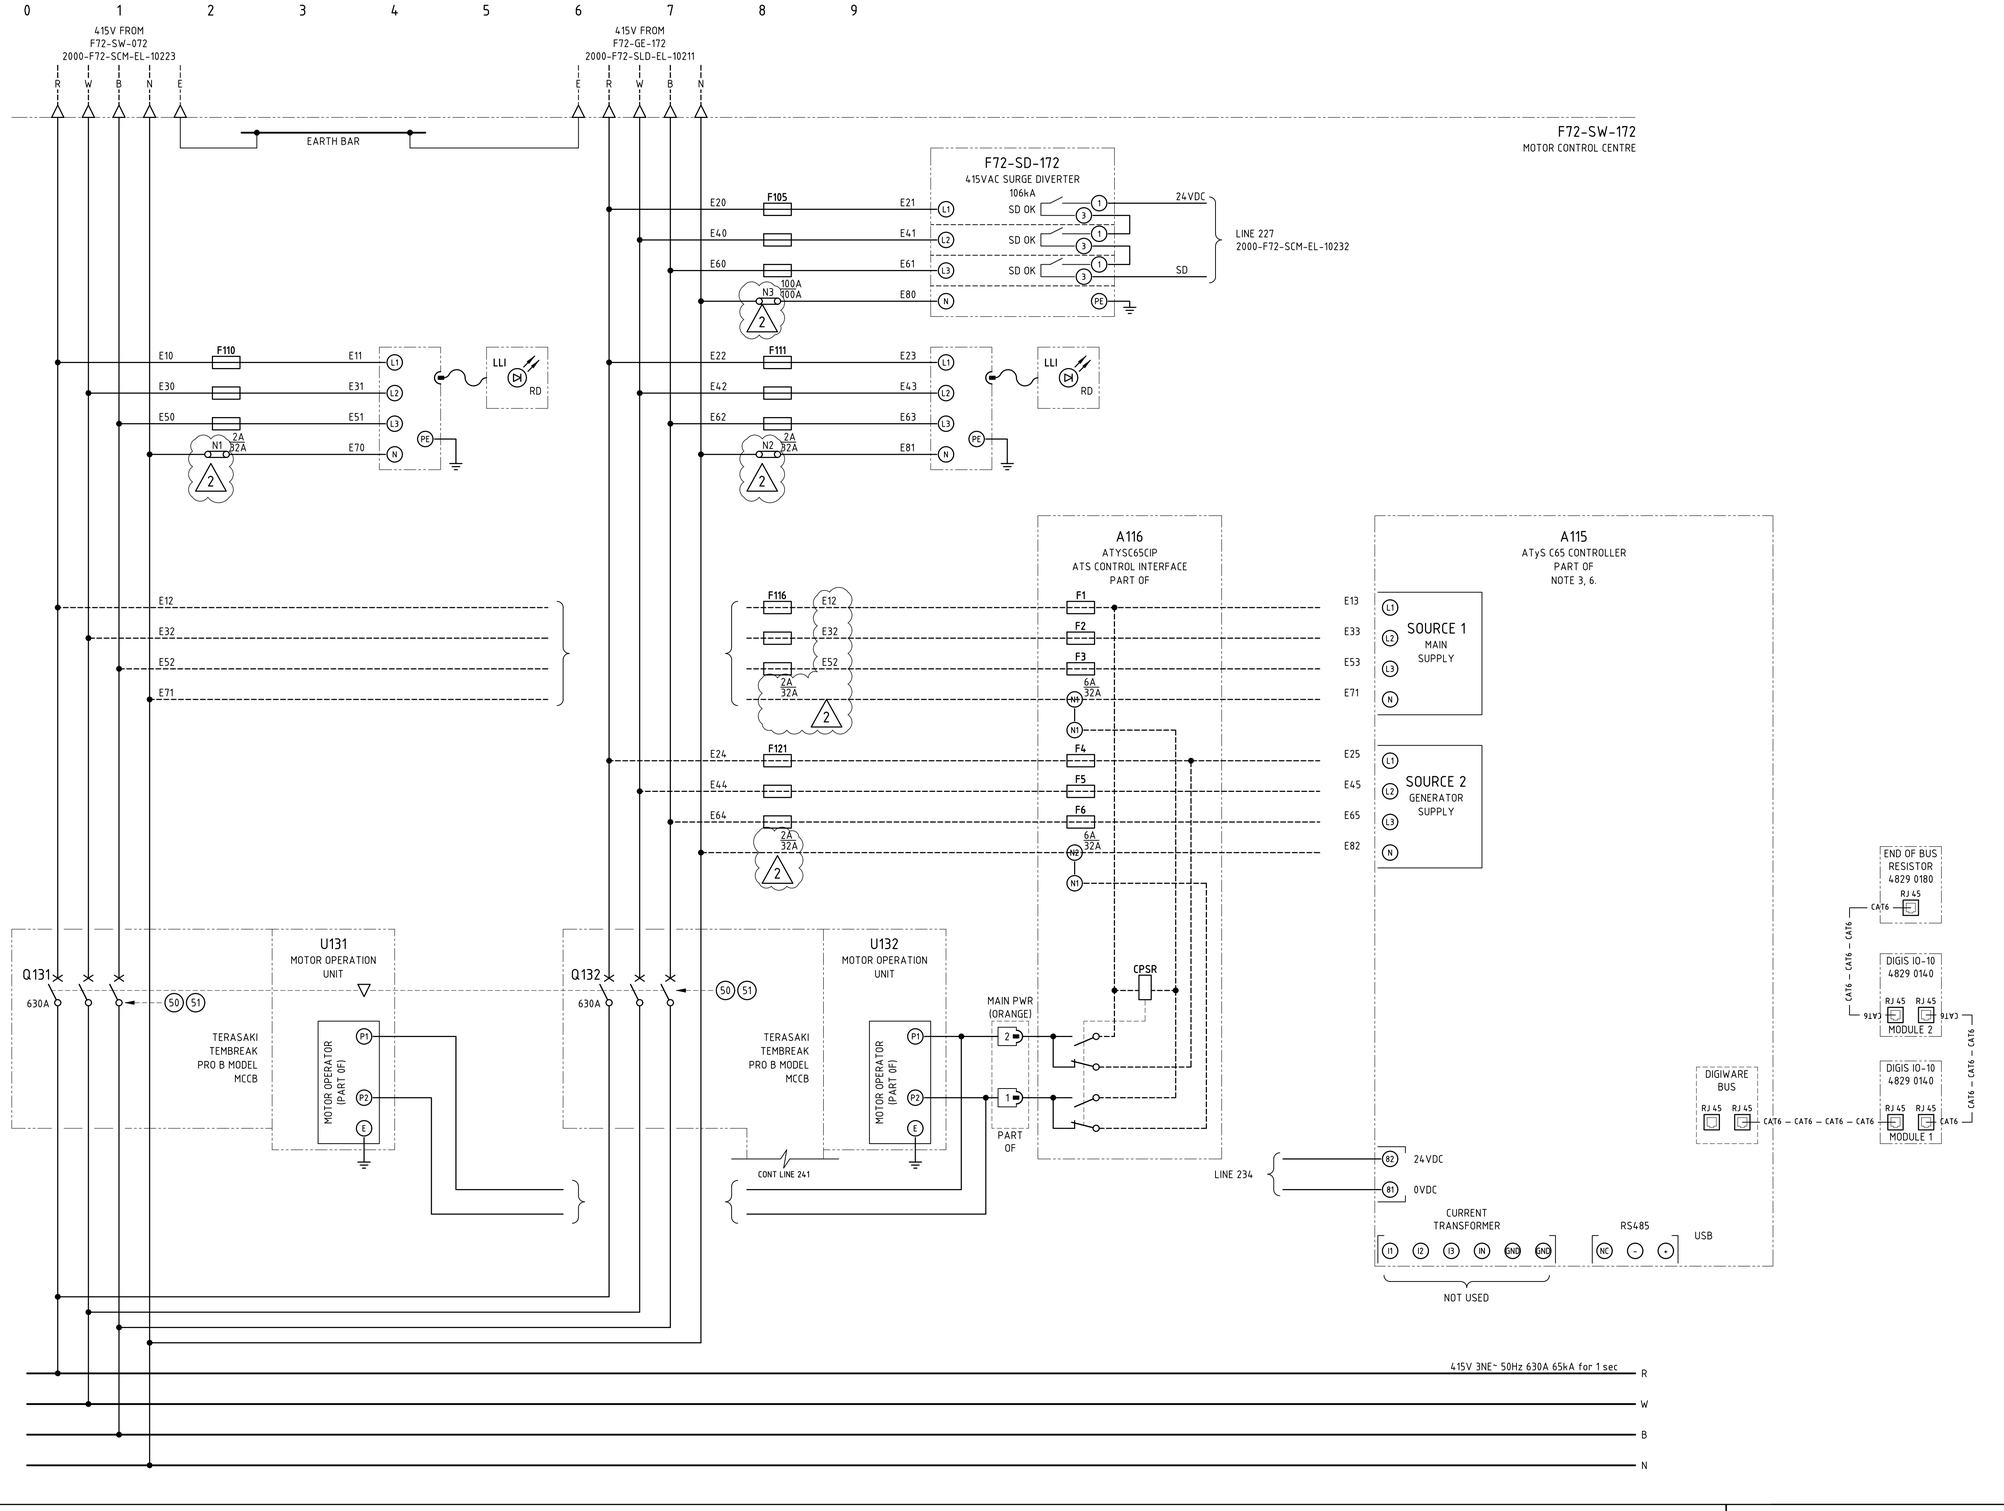


NOTES

1. SURGE DIVERTERS SHALL PROVIDE FEEDBACK TO DCS VIA VOLT-FREE CONTACTS. SURGE DIVERTER FUSES SHALL BE SIZED BY VENDOR TO SUIT DUTY.
2. MINIATURE CIRCUIT BREAKERS SHALL BE SIZED AND RATED TO SUIT ACB AND INCOMER REQUIREMENTS.
3. ALL TERMINATIONS ABOVE 50VAC SHALL BE TO IP2x OR ABOVE, IF NOT, TO HAVE A SEPARATE PERSPEX SHROUD FITTED AND SHALL BE LABELLED "DANGER xxxVAC".
4. WIRE NUMBER FERRULES ON TERMINAL STRIP SHALL BE PREFIXED WITH EQUIPMENT NUMBER e.g. F72SW172-0600 UNLESS NOTED OTHERWISE.
5. EACH WIRE SHALL BE IDENTIFIED AT BOTH ENDS WITH FERRULES.
6. ATS TO BE CONFIGURED SUCH THAT LOSS OF MAINS POWER SHALL START GENERATOR AND TRANSFER SUPPLY SOURCE. UPON DETECTION OF MAINS POWER ATS SHALL AUTO TRANSFER TO MAINS AND SHUTDOWN GENERATOR WITH A NOMINAL DELAY OF 5 MINUTES.

LEGEND

- 00/01/00 — DCS DIGITAL INPUT
- 00/02/00 — DCS DIGITAL OUTPUT
- MCC TERMINAL
- VSD TERMINAL
- FIELD TERMINAL
- DCS OR I/O TERMINAL
- MARSHALLING TERMINAL
- DEVICE TERMINAL
- INDICATION LAMP
  cc = COLOUR

2000-F72-SCM-EL-10231_Rev2

F72-SW-172 F72-SW-172 415V emergency MCC incomer schematic diagram sheet 1

"SOURCES LTD\23517 KCGM GROWTH PROJECT\03 DELIVERABLES\ELF72 - REAGENTS MIXING & STORAGE\2000-F72-SCM-EL-10231.DWG 02DEC25 12:40PM HOTSEAT04